

ПРОЕКТ ИНДИВИДУАЛЬНОГО ЖИЛОГО ДОМА

Конструктивный раздел

Подрядчик:

Заказчик:


Ведомость рабочих чертежей основного комплекта (КР)	
---	--

Лист	Наименование	Примечание
1	Ведомость рабочих чертежей основного комплекта (КР)	
2	Перспективный вид каркаса №1	
3	Перспективный вид каркаса №2	
4	Разрез каркаса 1-1. М1:30	
5	План свайного поля. М1:50	
5	План расположения элементов обвязки свайного поля. М1:50	
7	Перспективный вид обвязки фундамента	
8	План расположения элементов перекрытия 1 этажа. М1:40	
9	Перспективный вид перекрытия первого этажа	
10	Узлы монтажа элементов перекрытия	
11	Узлы монтажа элементов перекрытия	
12	План расположения элементов силового каркаса первого этажа. М1:40	
13	Узлы монтажа стен и перегородок	
14	Модуль 1	
15	План расположения элементов перекрытия Модуля 1. М1:30	
16	План расположения элементов стены. Стена 01	
17	План расположения элементов стен. Стена 02	
18	План расположения элементов стены. Стена 03	
19	Стропильная система Модуля 1	
20	Модуль 2	
21	План расположения перекрытия Модуля 2. М1:30	
22	План расположения элементов стен. Стена 04	
23	План расположения элементов стен. Стена 05	
24	План расположения элементов стен. Стена 11	
25	Стропильная система Модуля 2	
26	Модуль 3	
27	План расположения элементов перекрытия Модуля 3	
28	План расположения элементов стен. Стена 06	
29	План расположения элементов стены. Стена 07	
30	План расположения элементов стен. Стена 08	
31	План расположения элементов стен. Стена 09. Стена 10	
32	Стропильная система модуля 3	
33	Модуль 4	


Лист	Наименование	Примечание
34	План расположения элементов перекрытия Модуля 4	
35	Стропильная система Модуля 4	
36	Модуль 5	
37	План расположения элементов перекрытия Модуля 5	
38	План расположения элементов стропильной системы Модуля 5	
39	Модуль 6	
40	План расположения элементов перекрытия Модуля 6	
41	План расположения элементов стропильной системы Модуля 6	
42	Спецификация пиломатериала силового каркаса	
43	Сводные данные	

						Одноквартирный жилой дом по деревянной модульной технологии			
Изм.	Кол.уч.	Лист	№Док.	Подп.	Дата		Стадия	Лист	Листов
Разработал							КР	1	43
Проверил						Ведомость рабочих чертежей основного комплекта (КР)			
Проверил									
Директор									


Перспективный вид каркаса №1

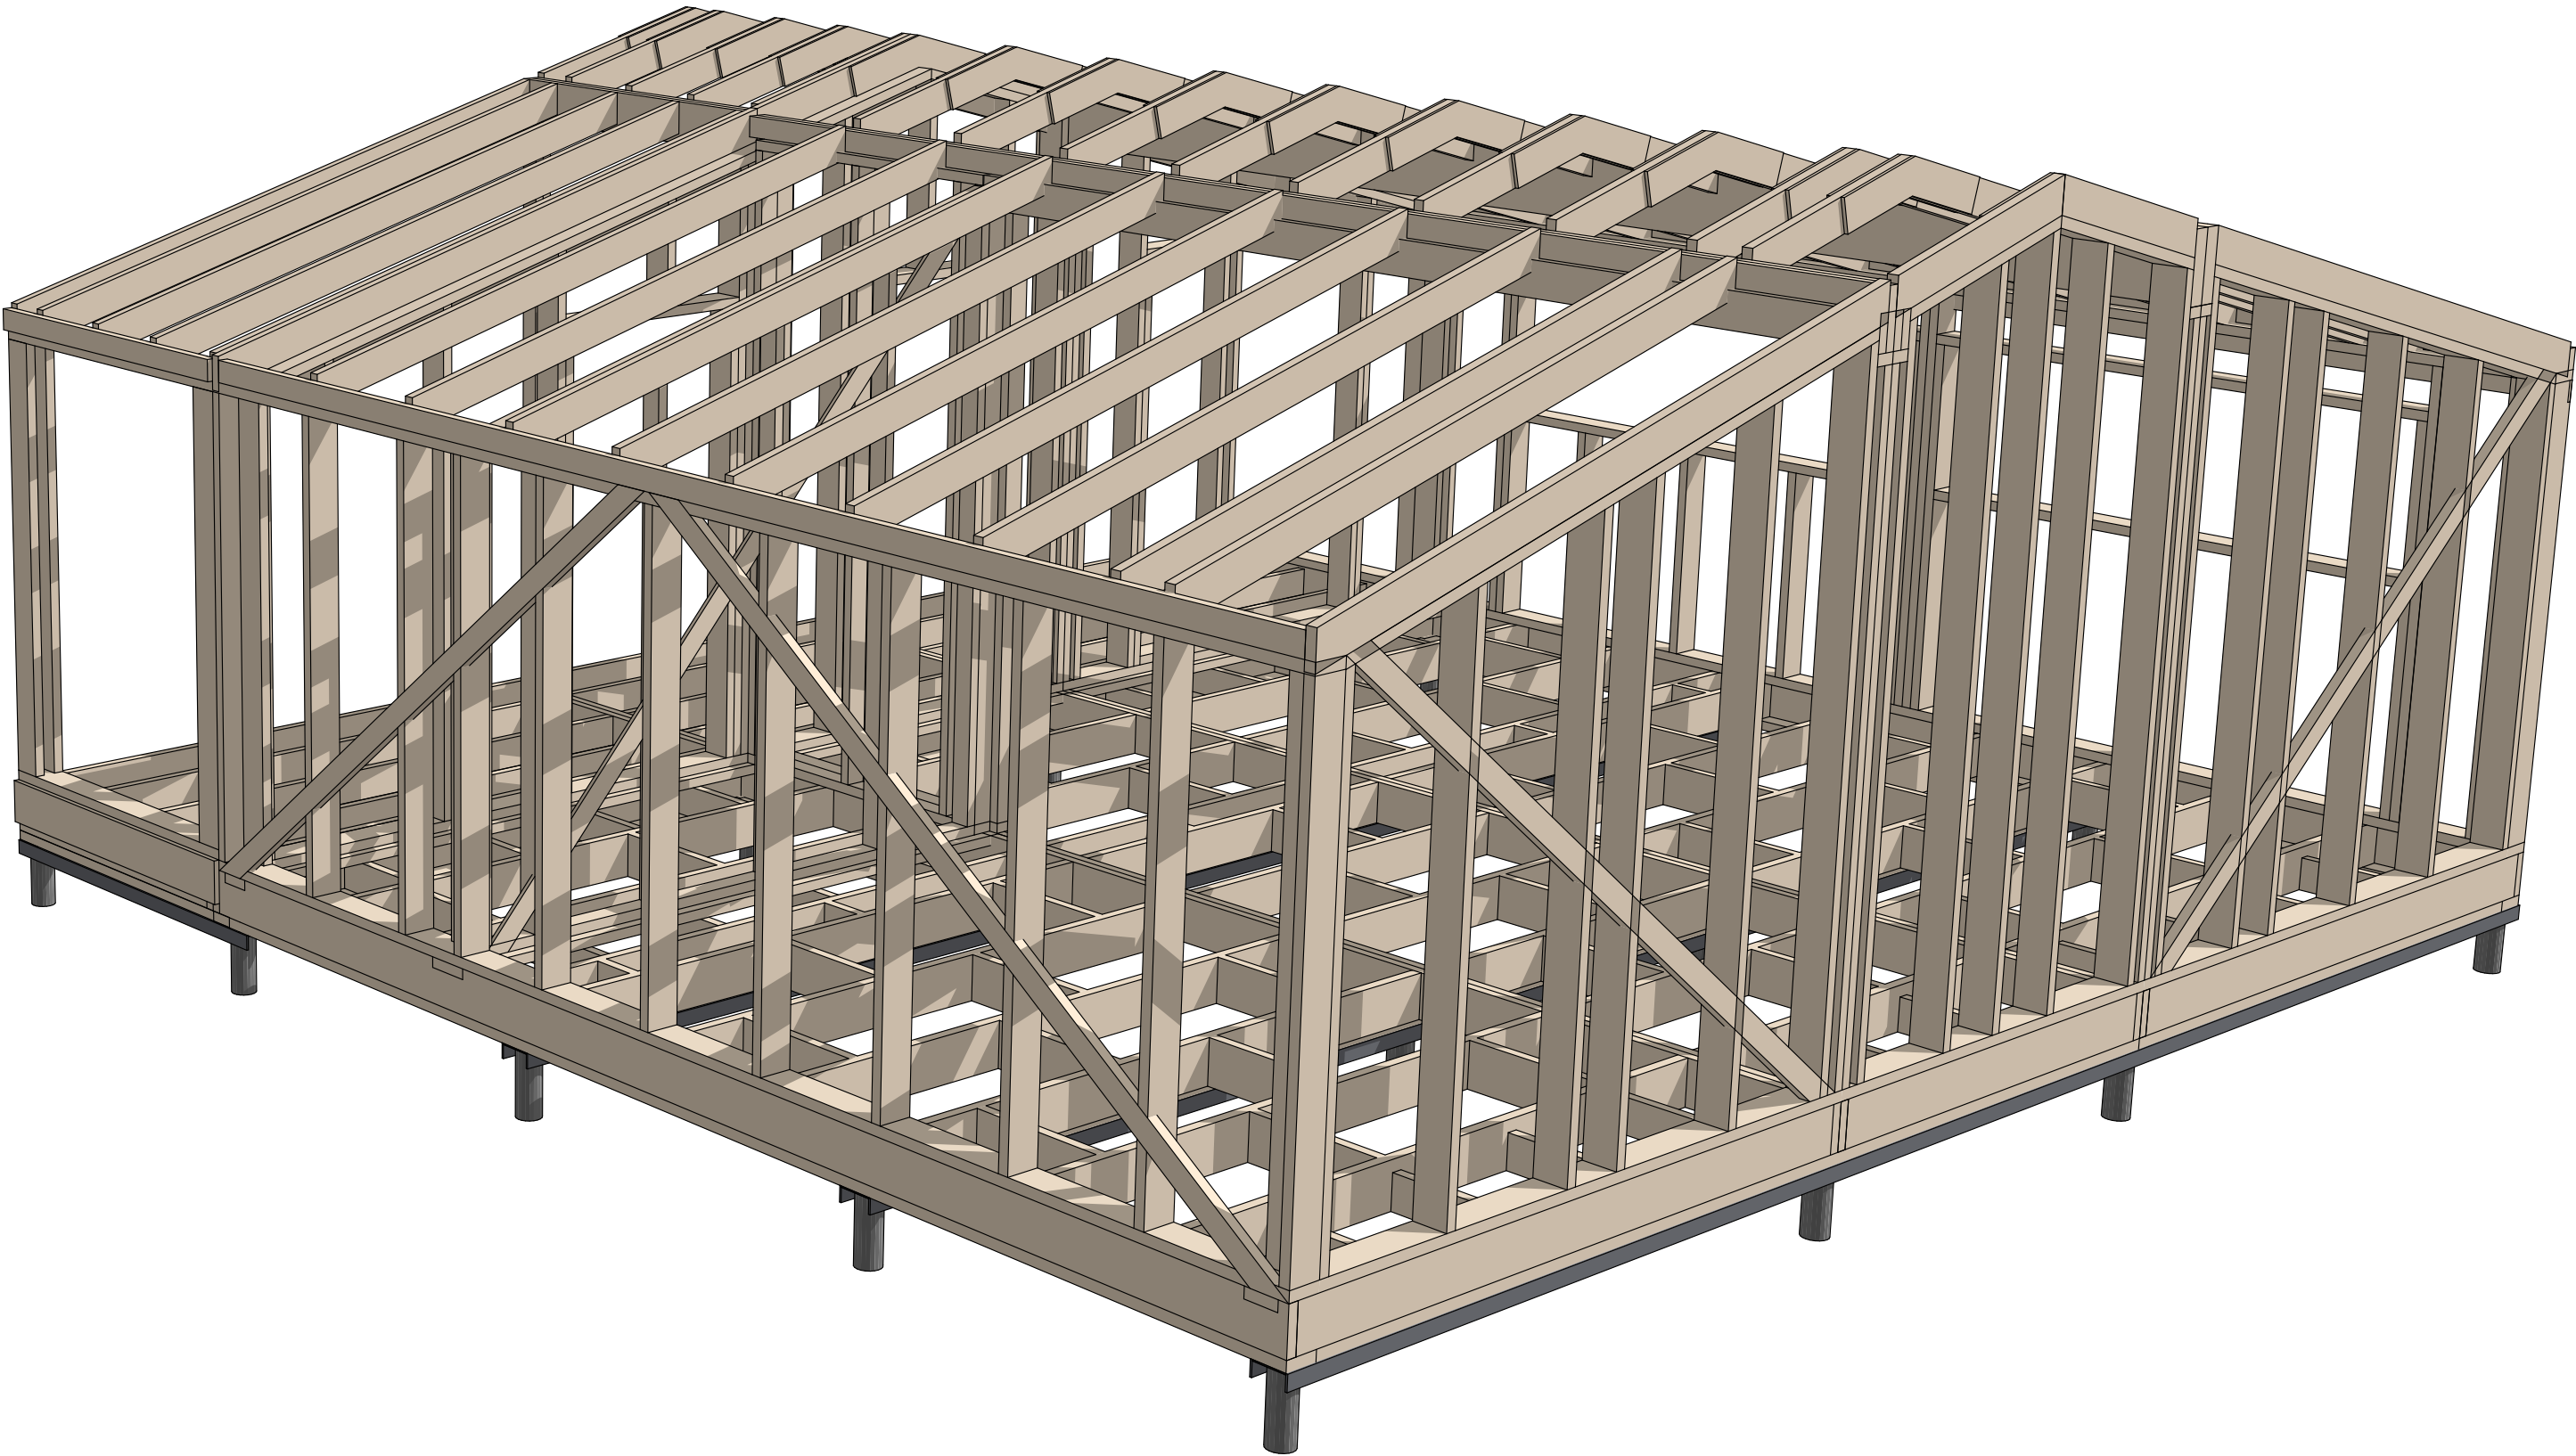


Перспективный вид каркаса №2

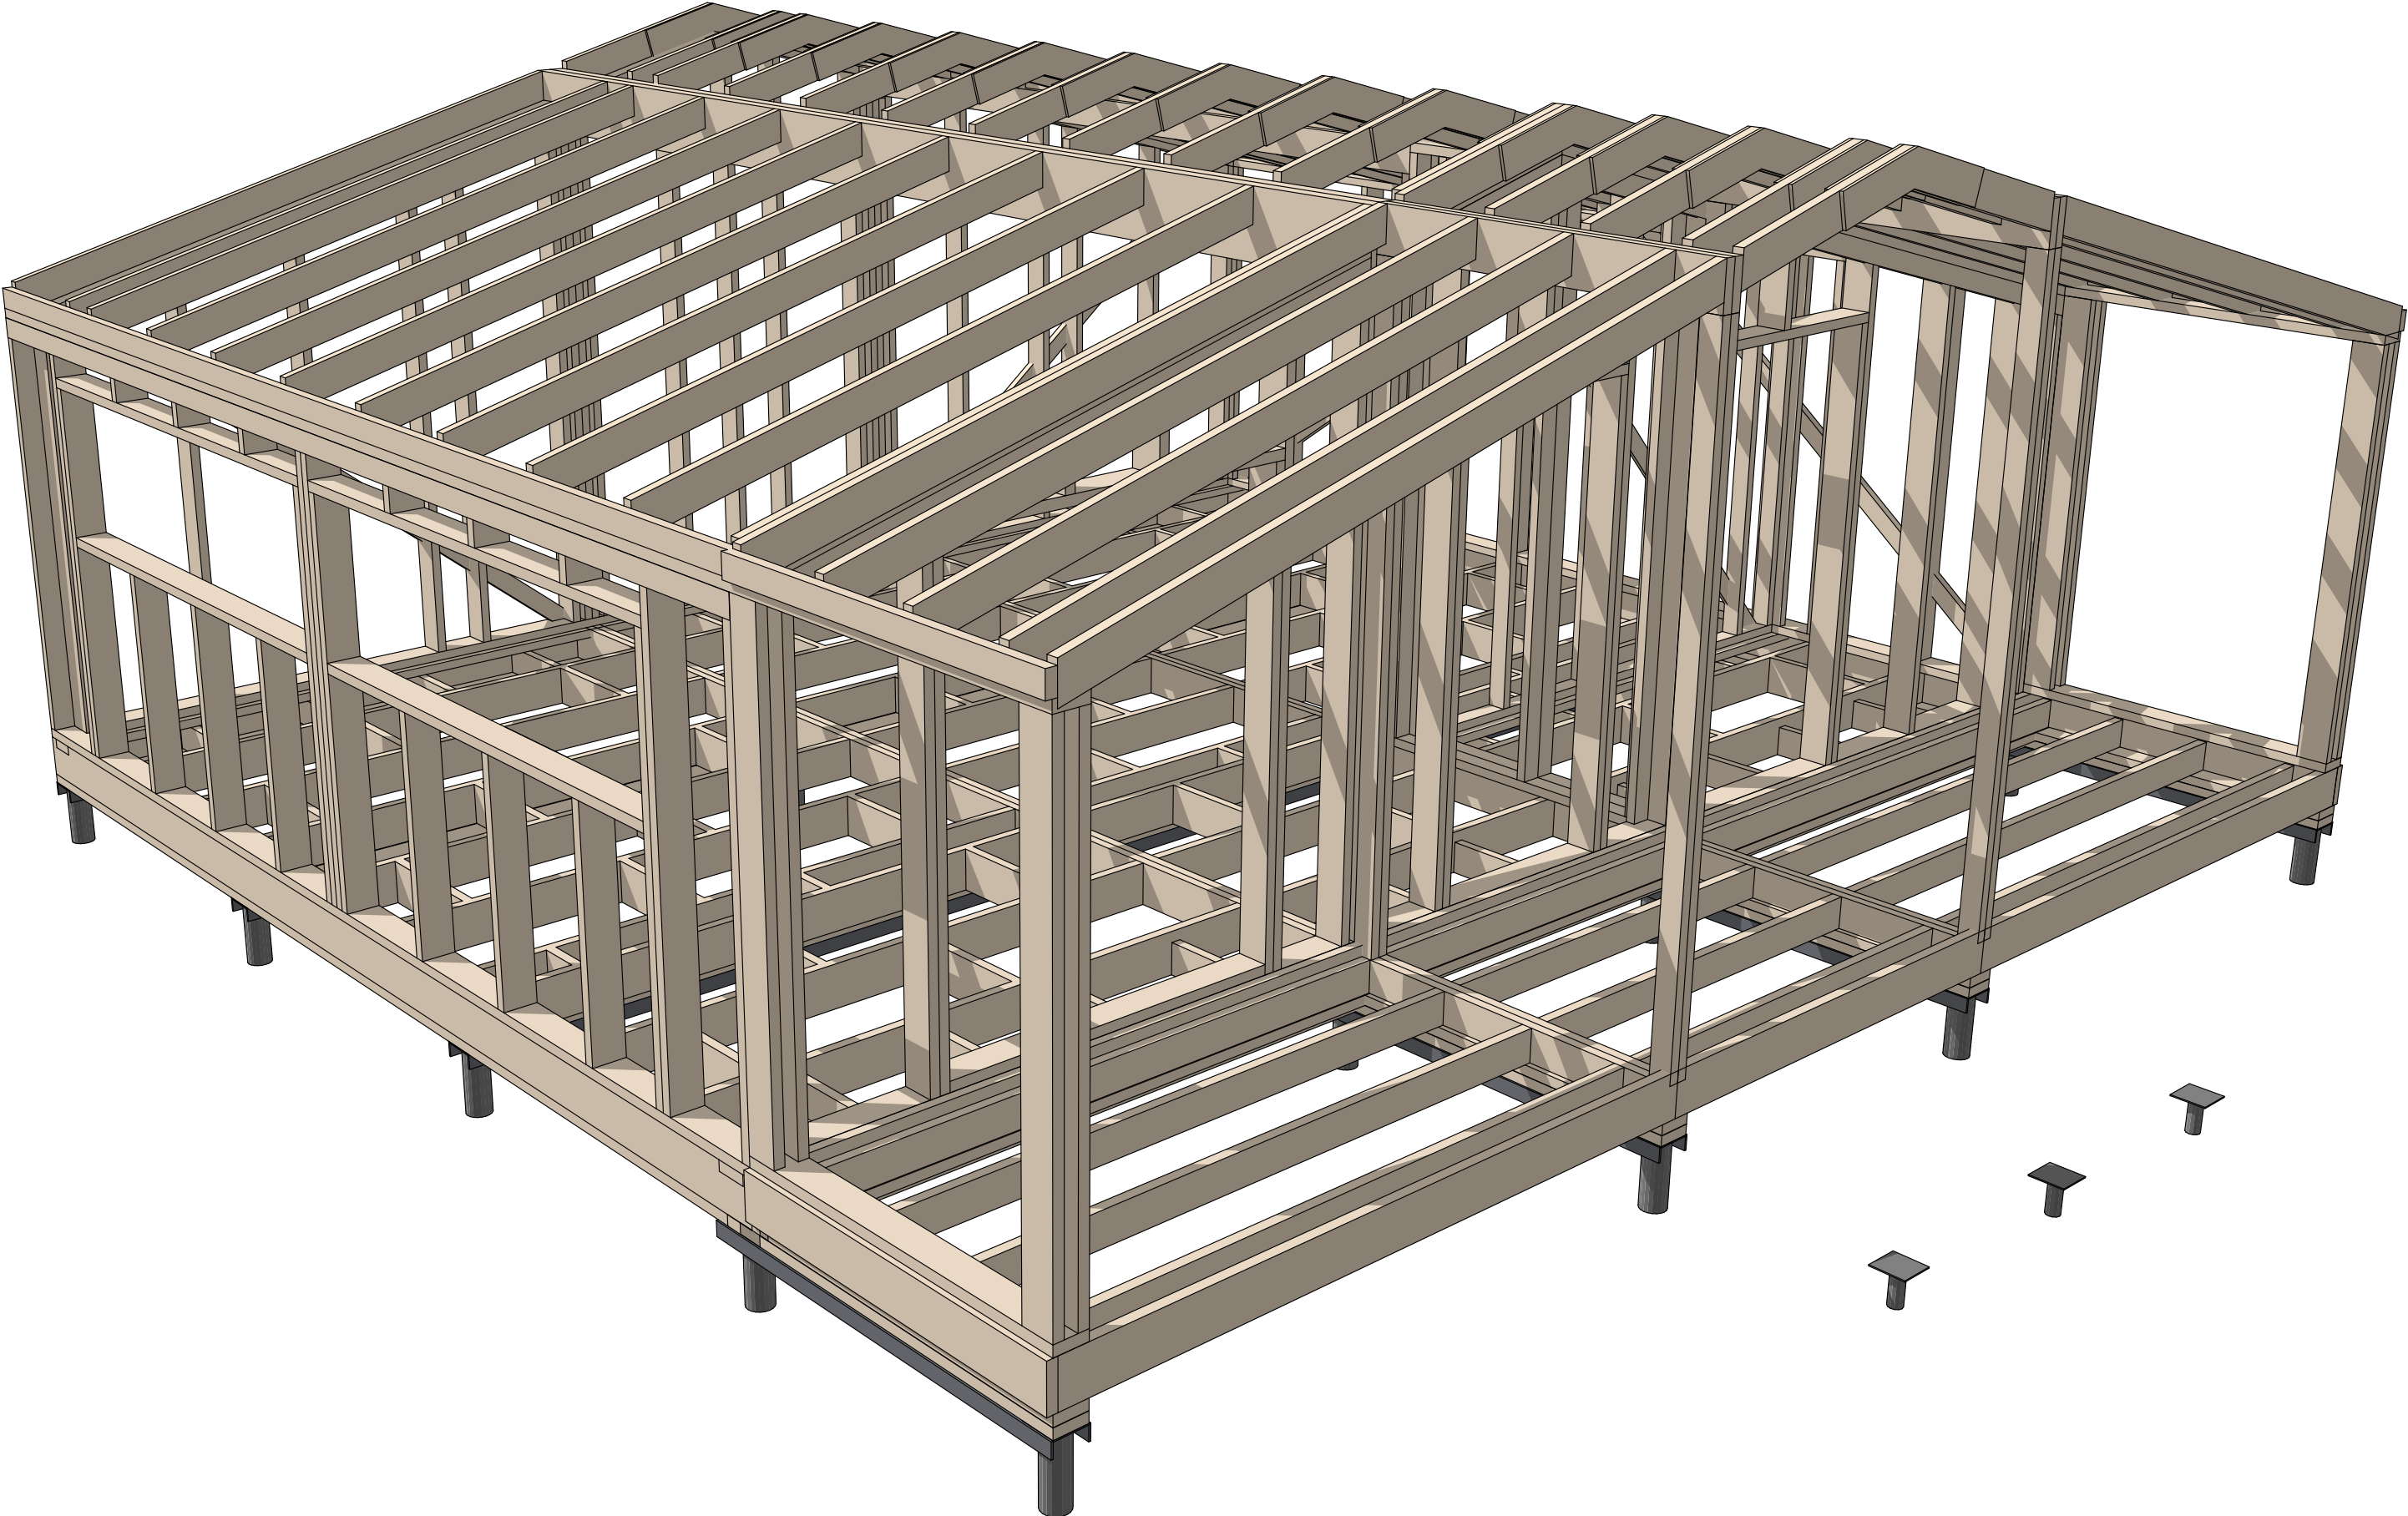

Разрез каркаса 1-1. М1:30

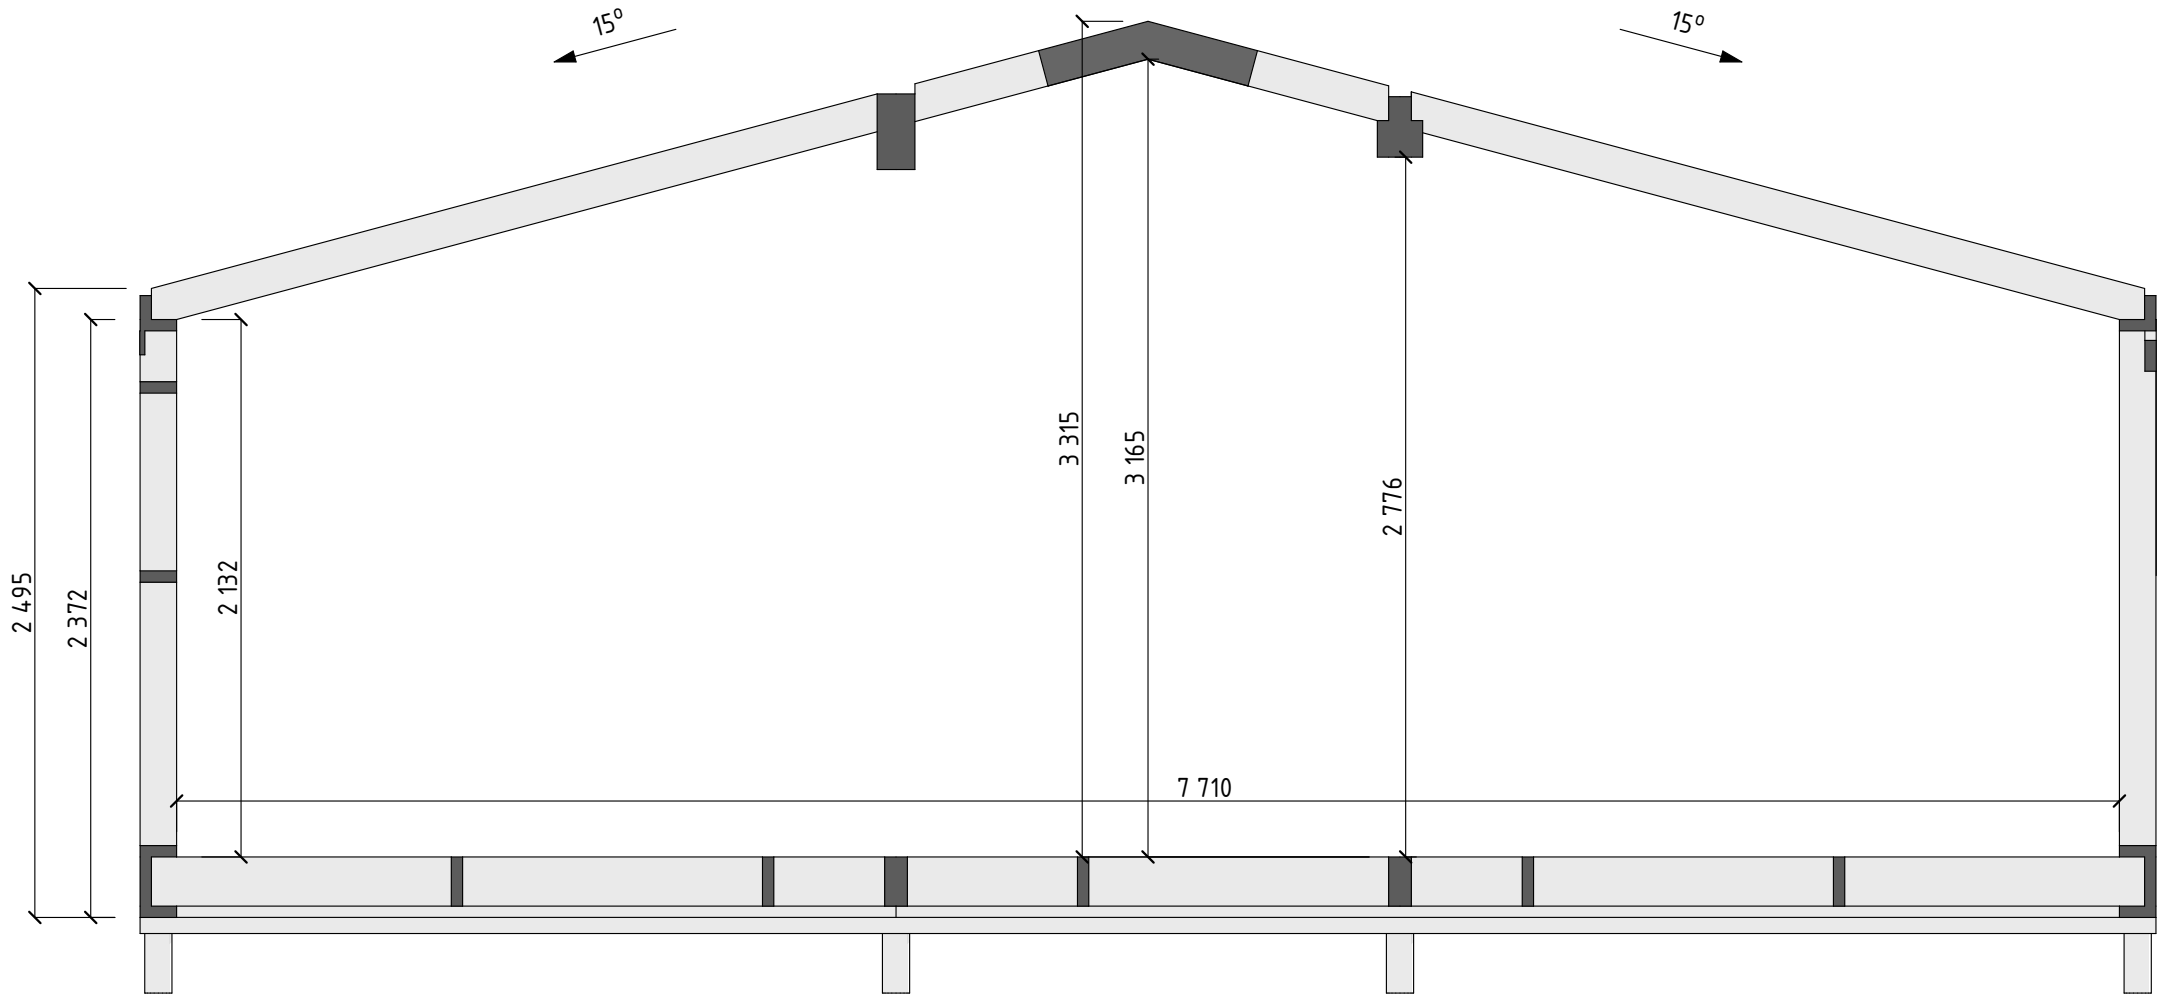



План свайного поля. М1:50

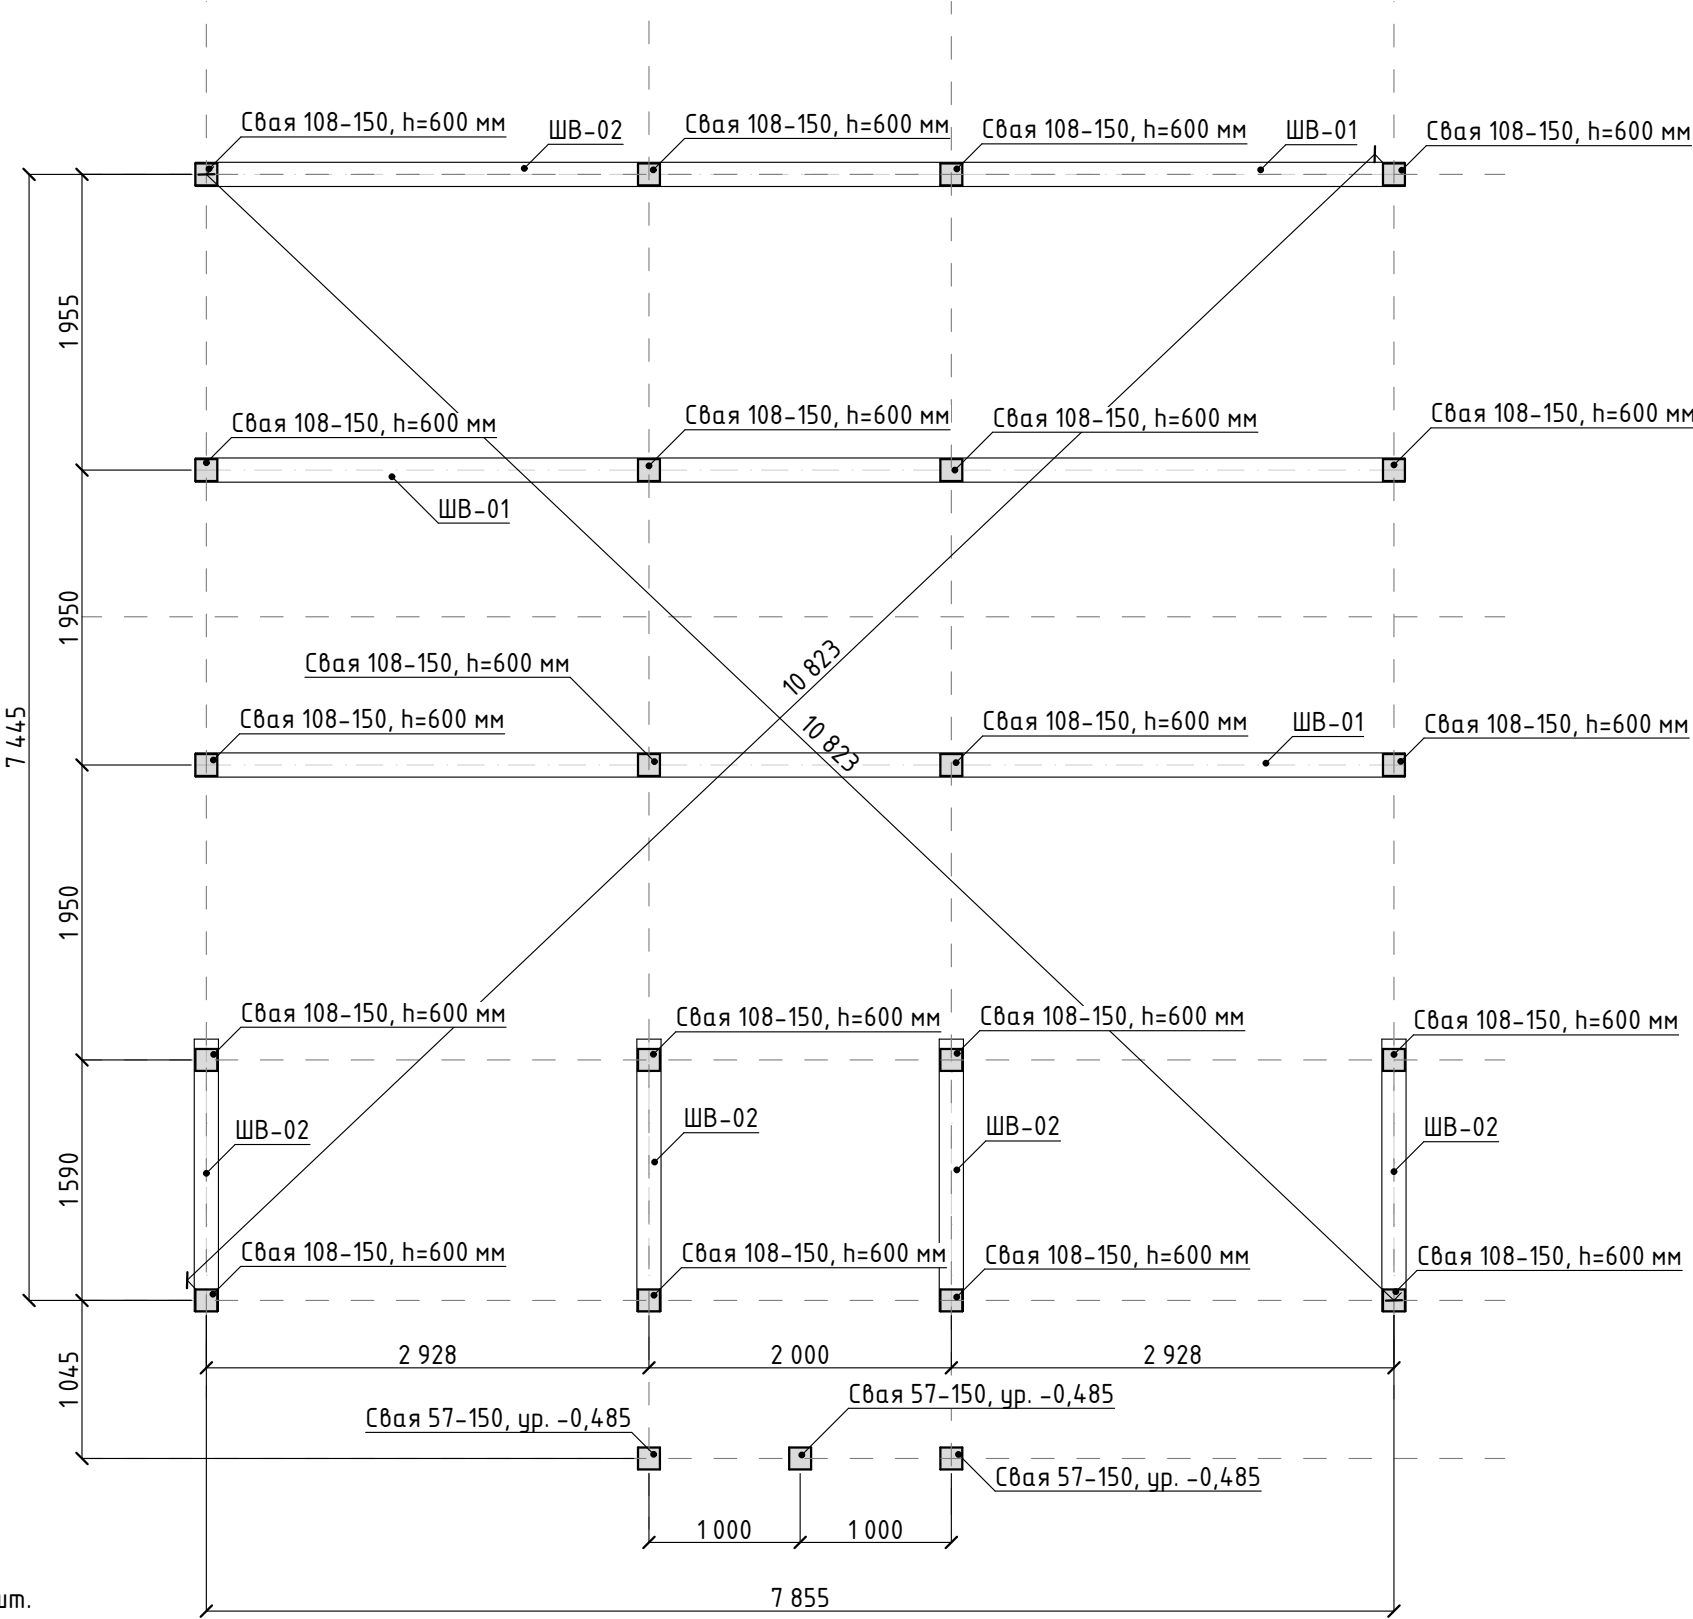

Металлические винтовые сваи Ø 108мм, L=2500мм – 20 шт.
Металлические винтовые сваи Ø 57мм, L=2500мм – 3 шт.

Спецификация элементов обвязки свай швеллером		
Поз.	Длина, мм	Кол-во
ШВ-01	8 000	3
ШВ-02	1 800	4


План расположения элементов обвязки свайного поля. М1:50

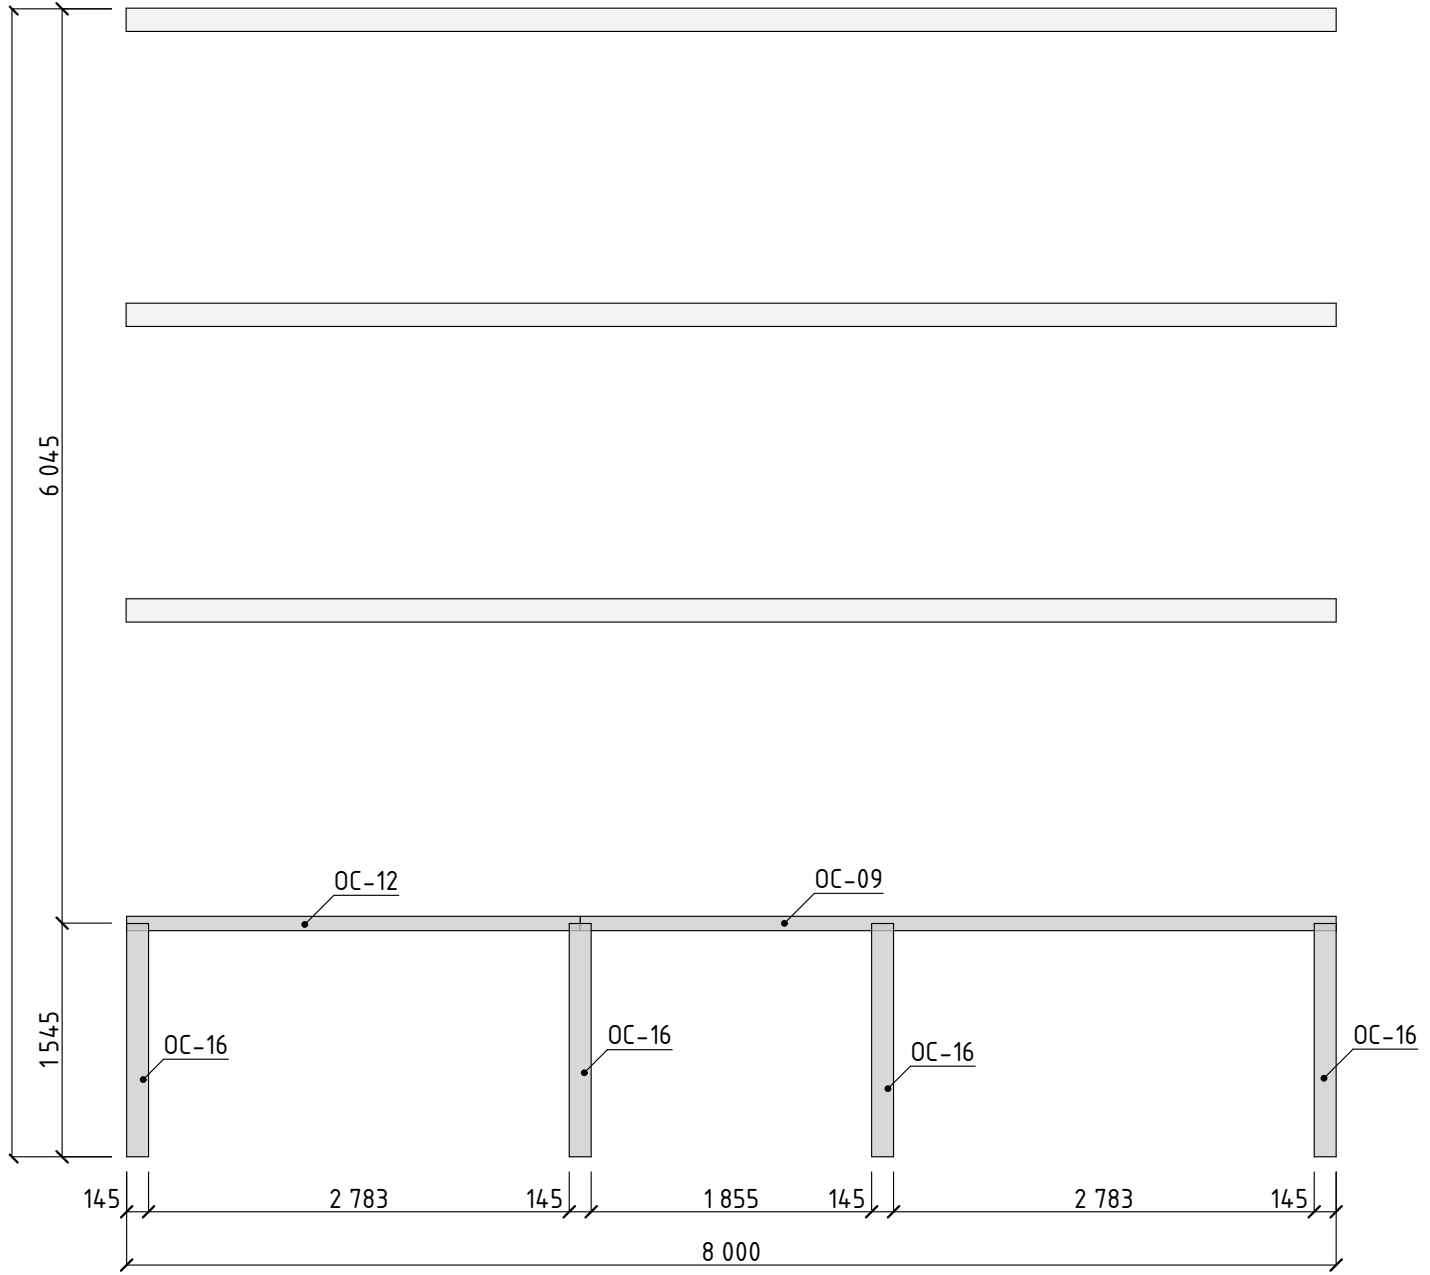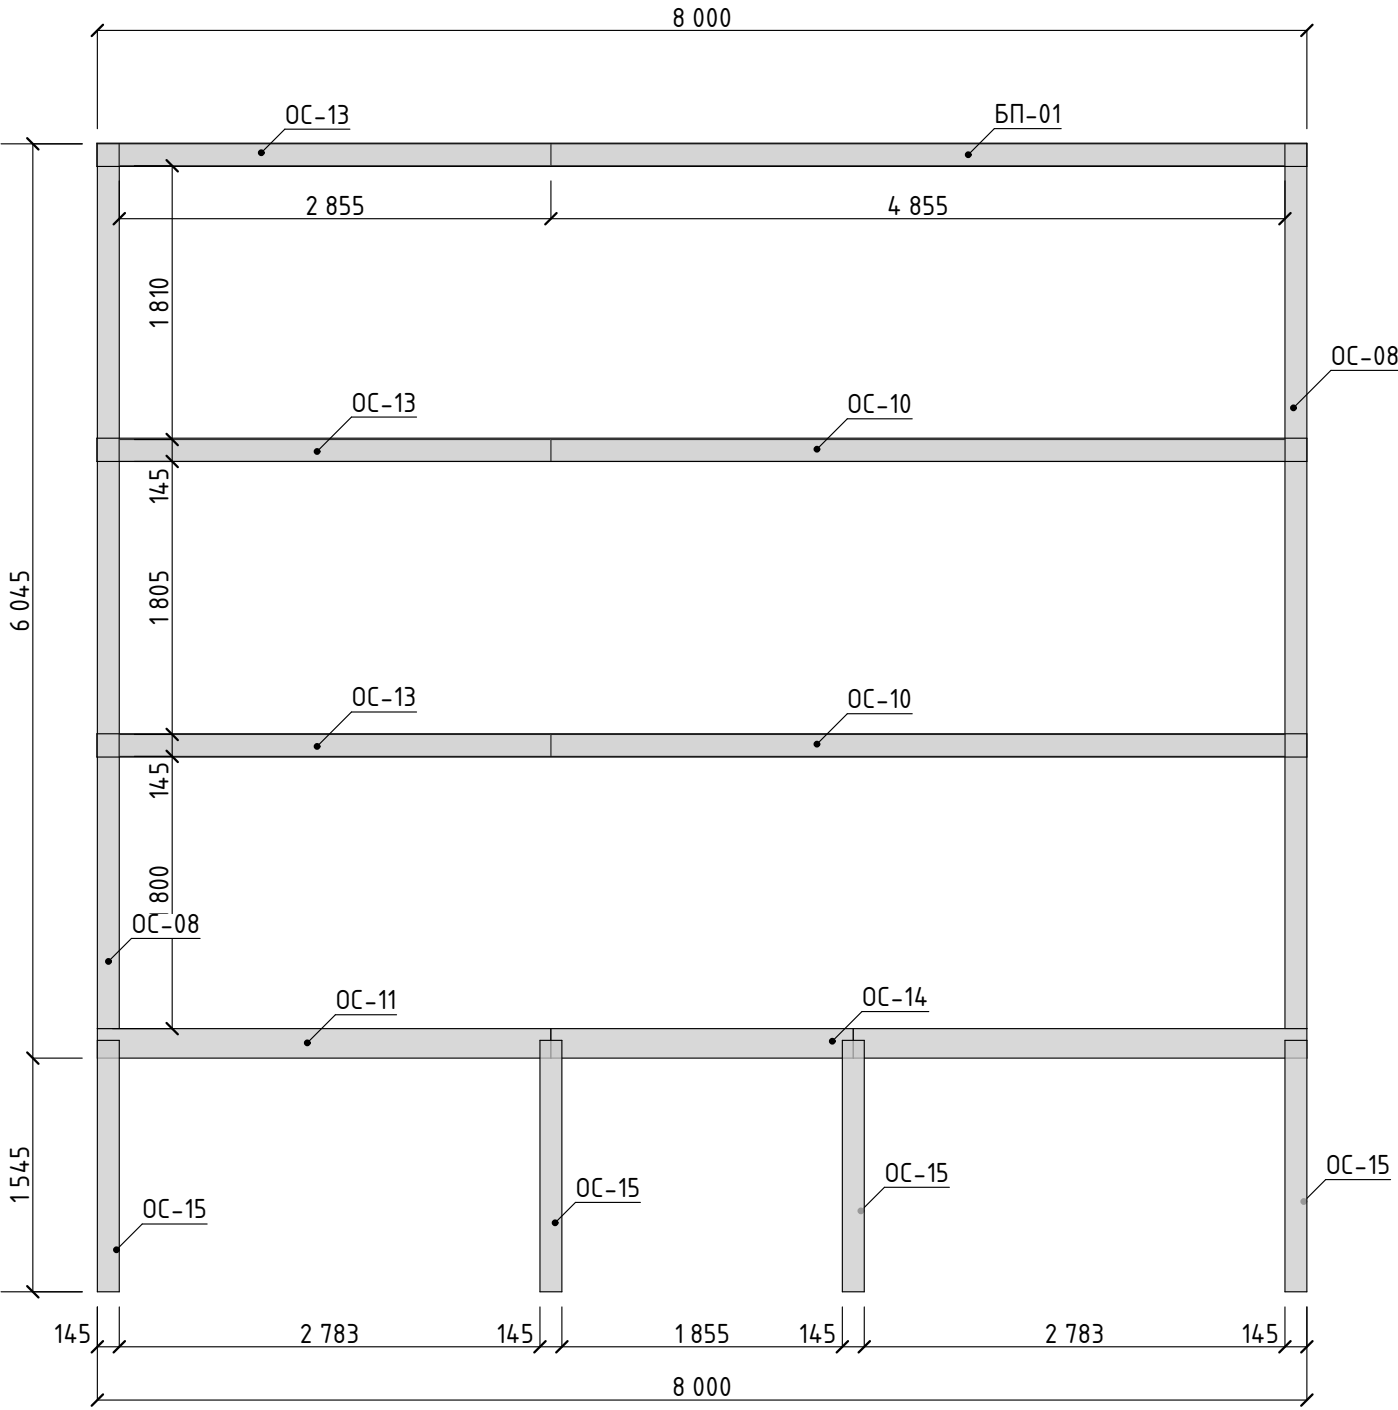

Спецификация элементов обвязки свай				
Поз.	Ширина, мм	Высота, мм	Длина, мм	Кол-во
БП-01	145	45	4 855	1
ОС-08	145	45	5 850	2
ОС-10	145	45	4 855	2
ОС-11	195	45	3 000	2
ОС-13	145	45	2 855	3
ОС-14	195	45	2 000	1
ОС-15	145	45	1 663	4


Поз.	Ширина, мм	Высота, мм	Длина, мм	Кол-во
ОС-09	95	45	5 000	1
ОС-12	95	45	3 000	1
ОС-16	145	45	1 543	4

Перспективный вид обвязки фундамента

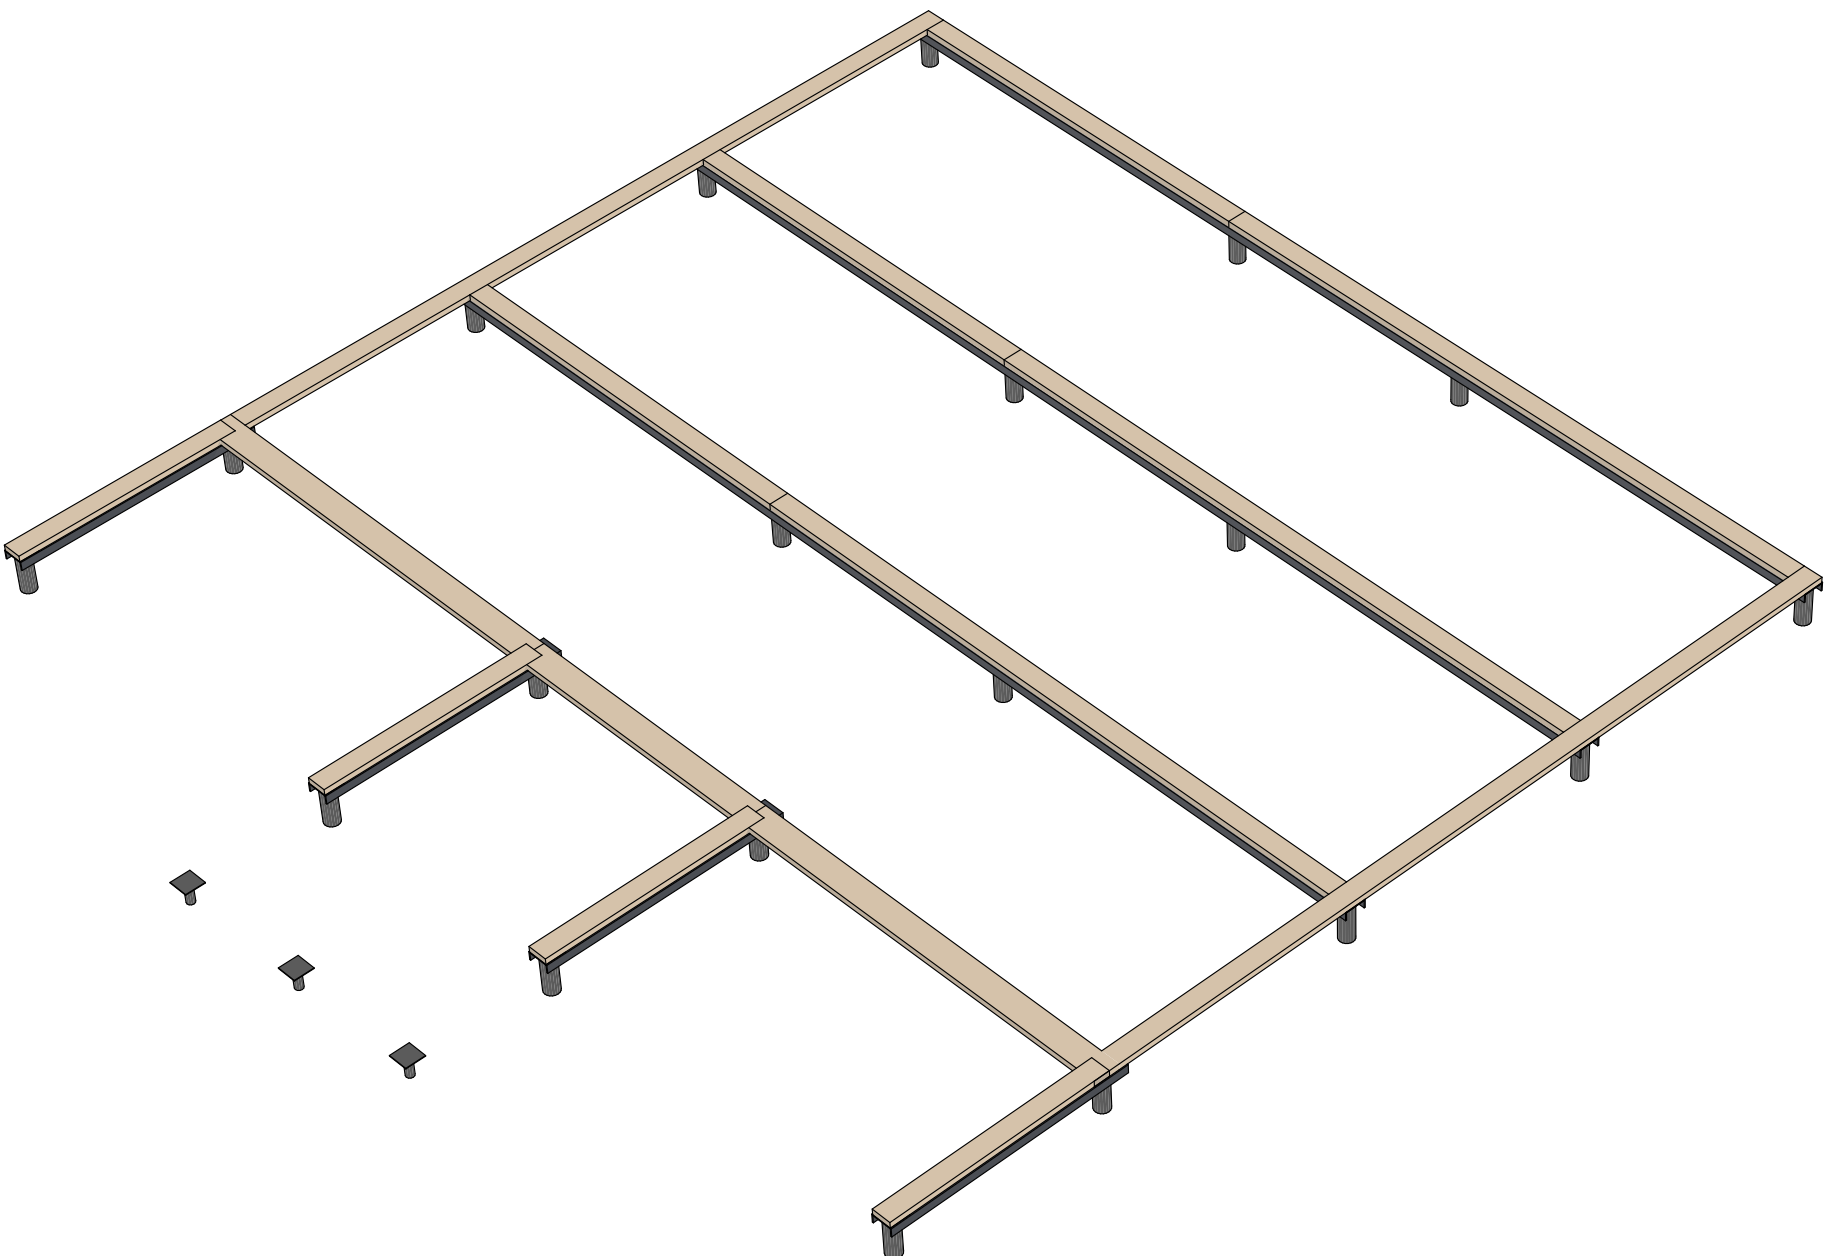


Перспективный вид обвязки фундамента

Смодия	Лист	Листов
КР	7	43

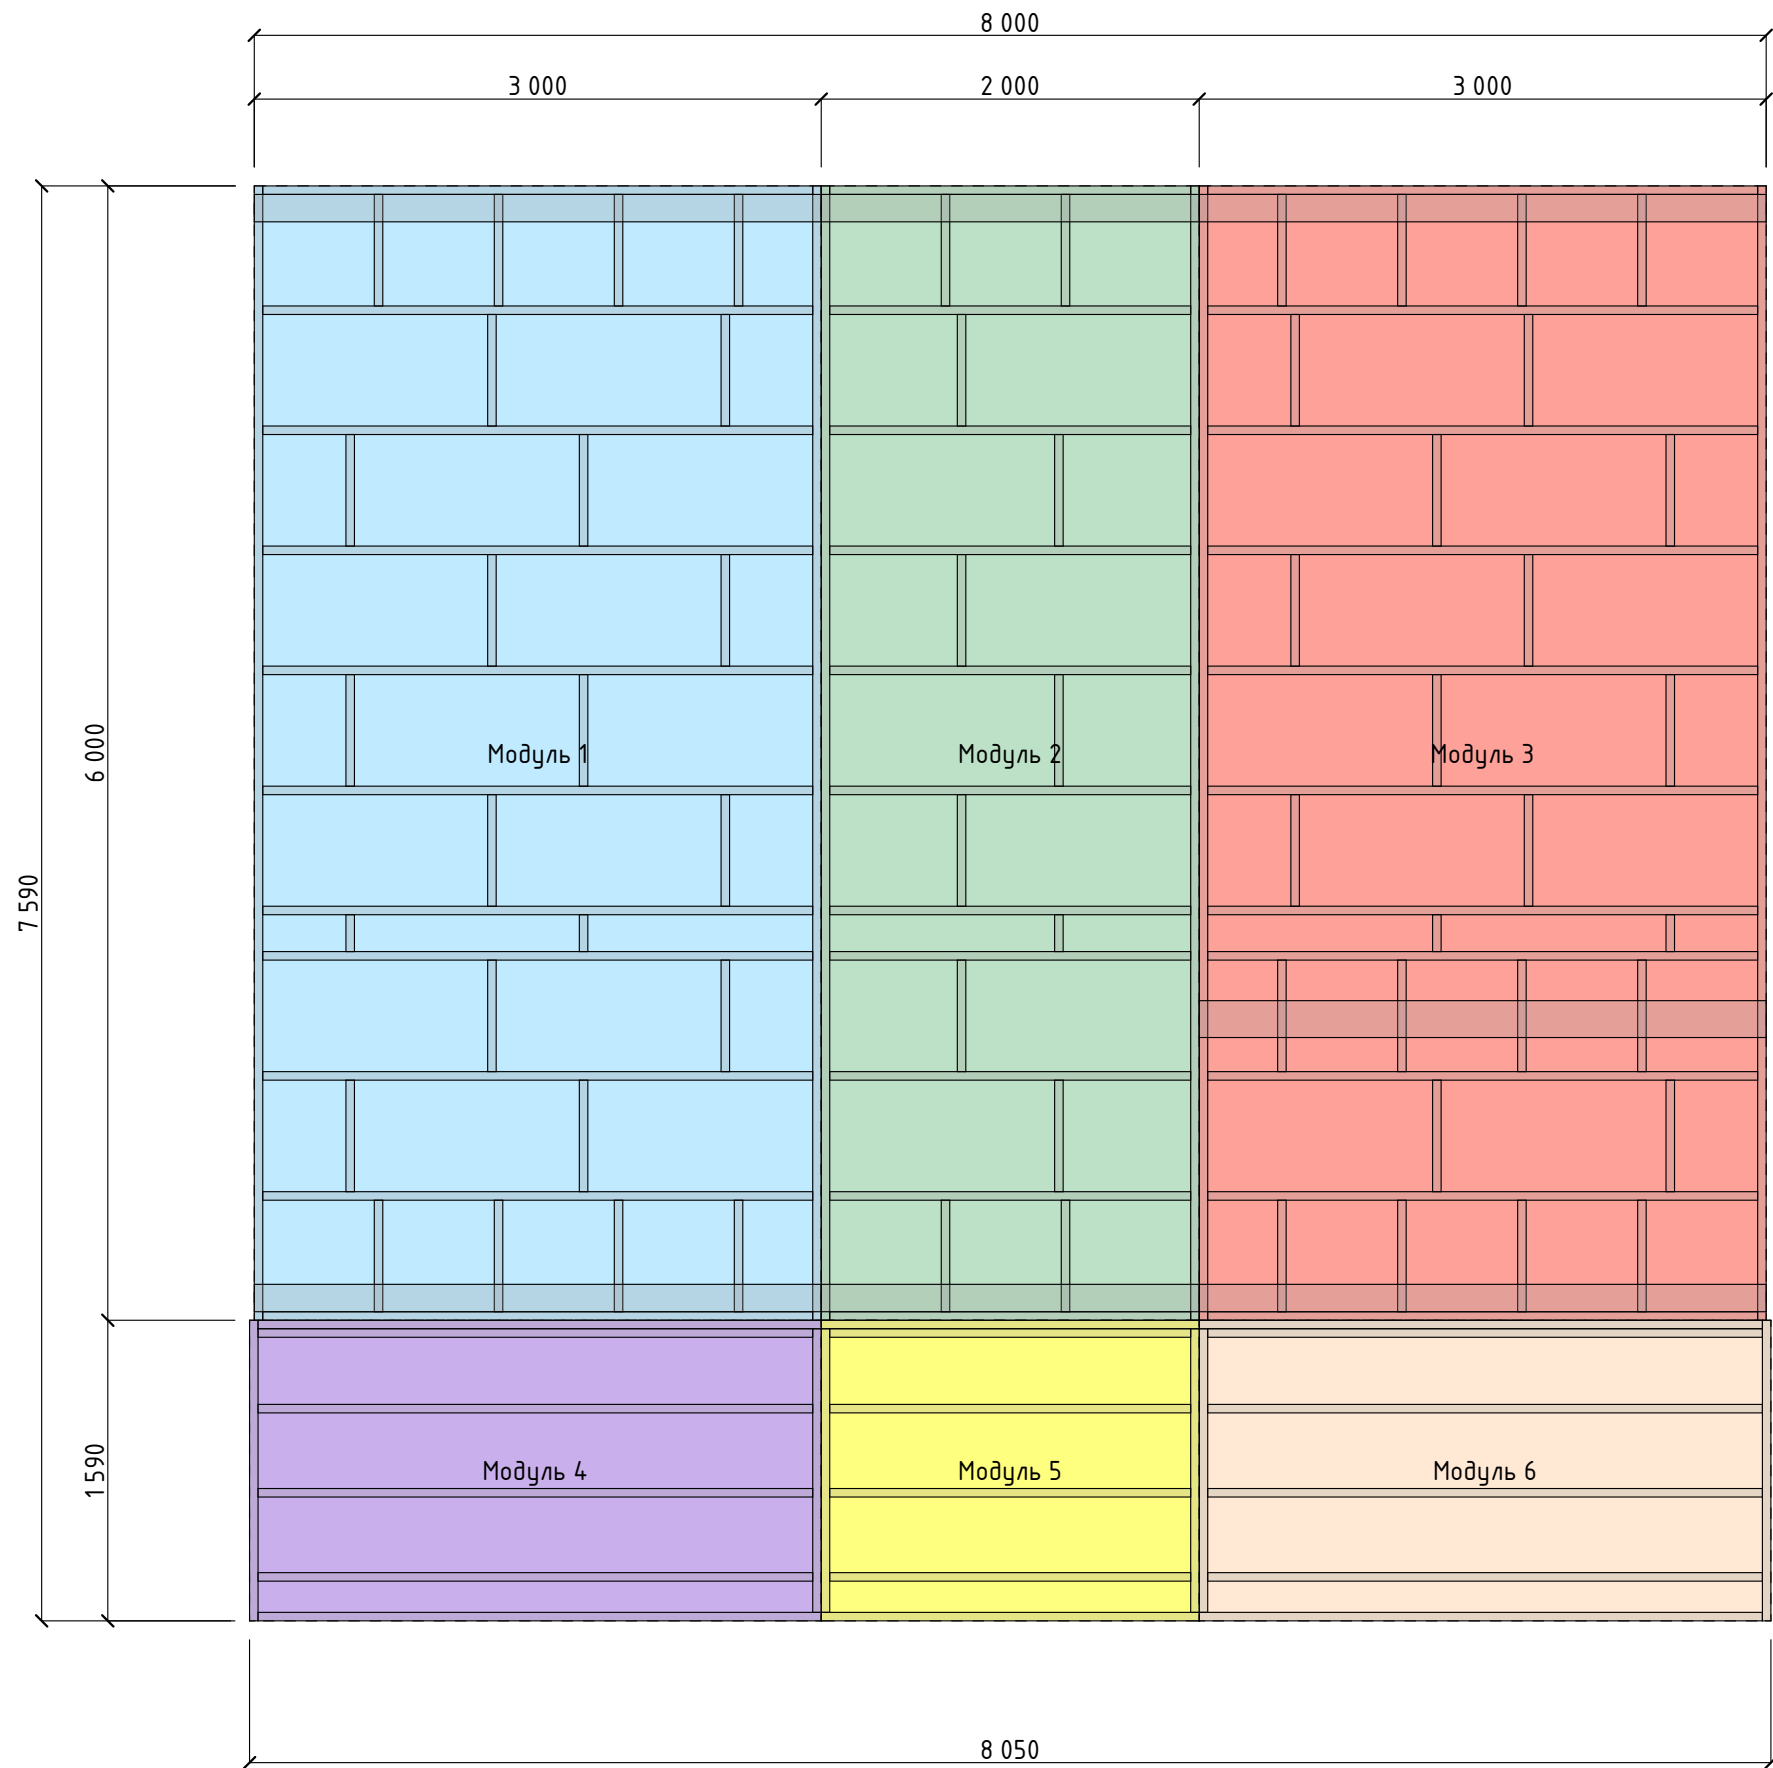

Перспективний вид перекриття першого этажа

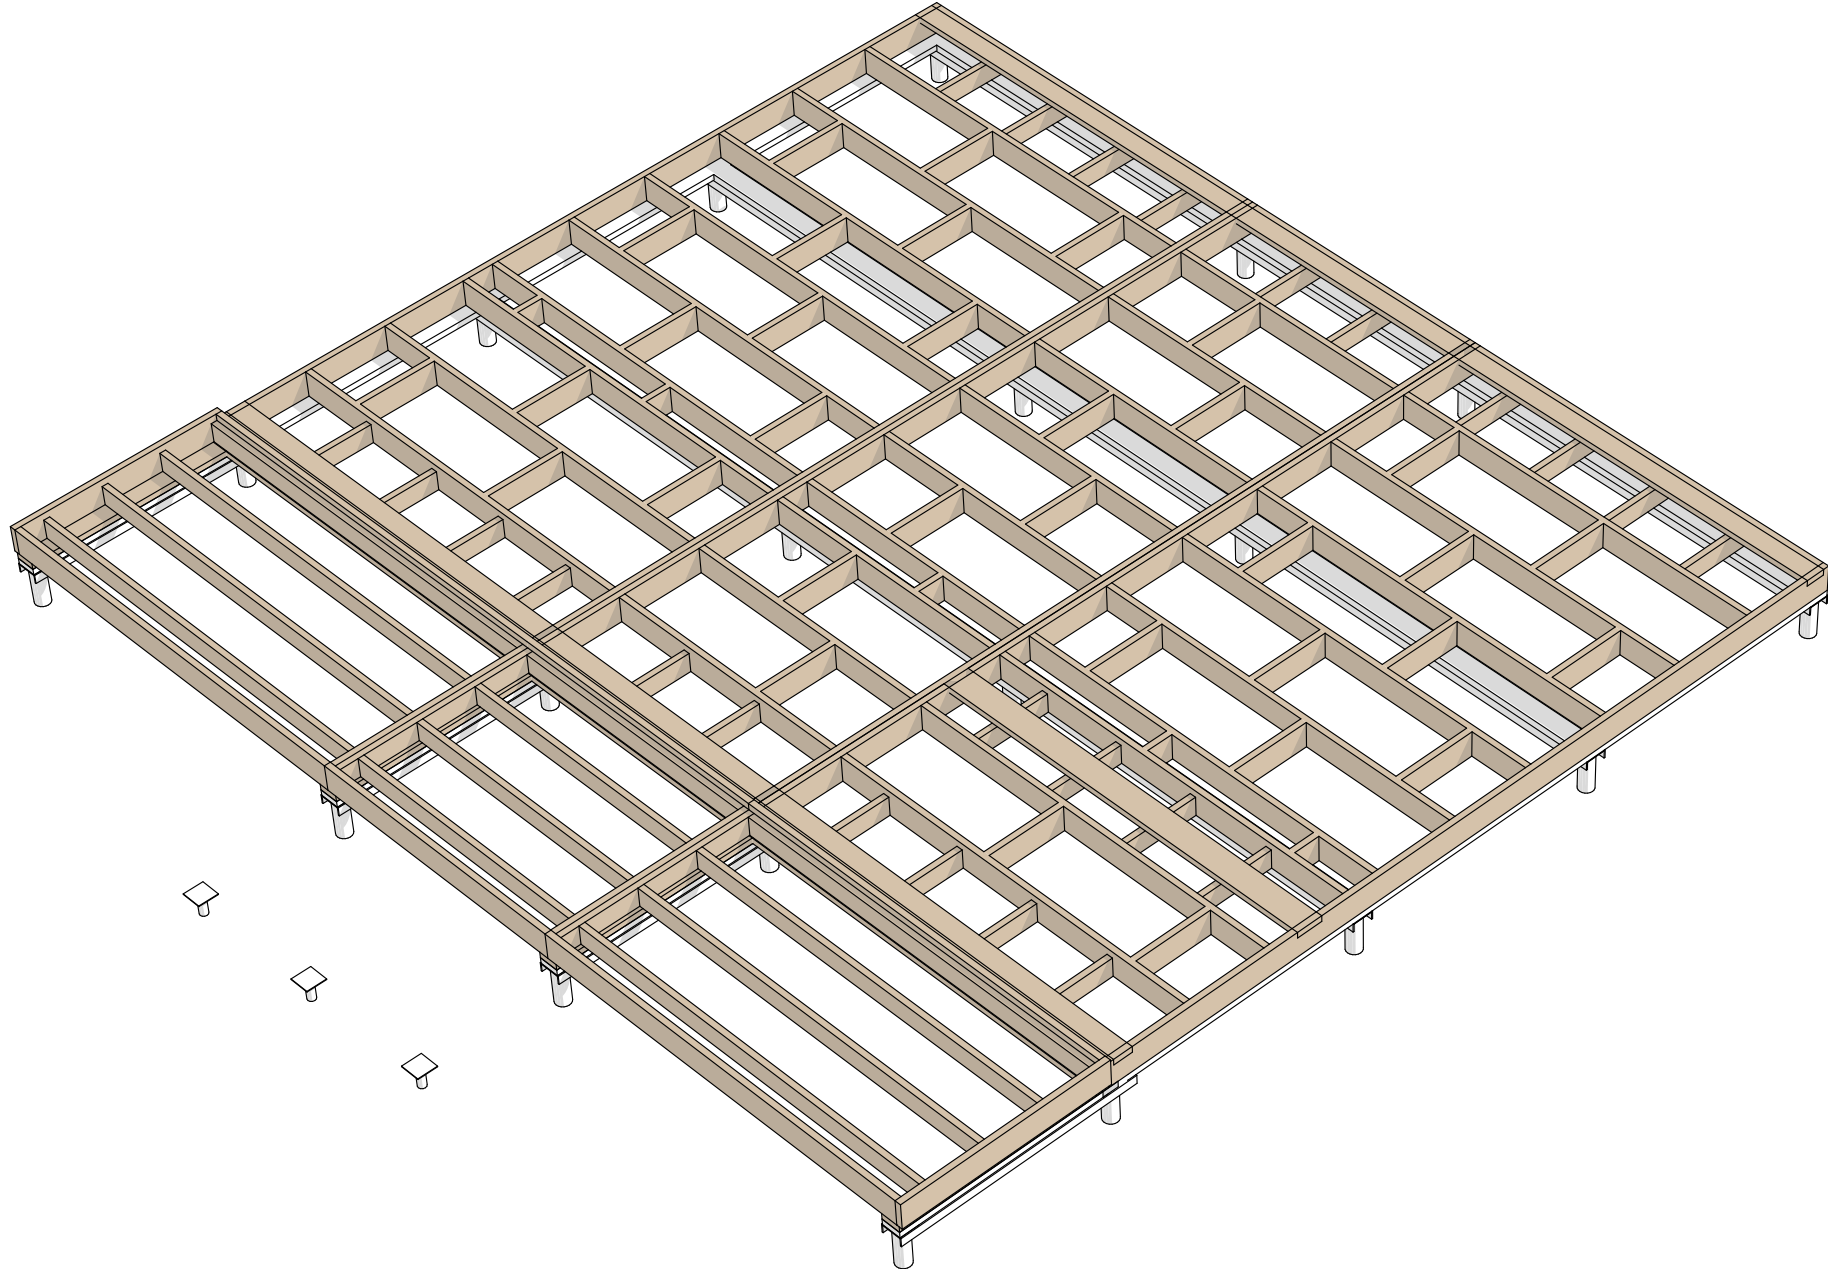


Перспективний вид перекриття першого этажа

Смадиця	Листм	Листмоб
КР	9	4,3


Узлы монтажа элементов перекрытия

Количество гвоздей по сечению пиломатериала


Высота до 100 мм
не менее двух гвоздей в торец

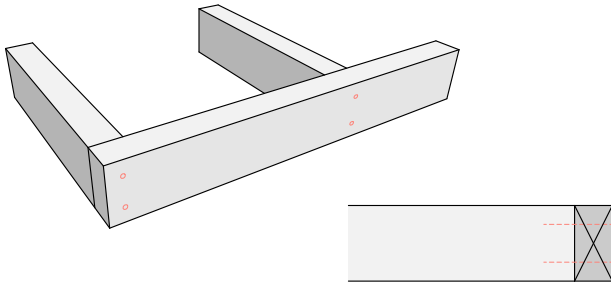



Высота до 150 мм
не менее трех гвоздей в торец

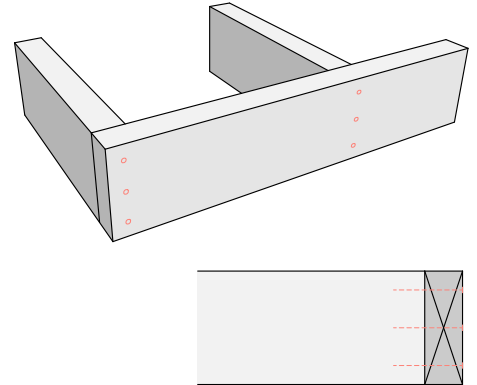

Высота до 200 мм
не менее четырех гвоздей в торец

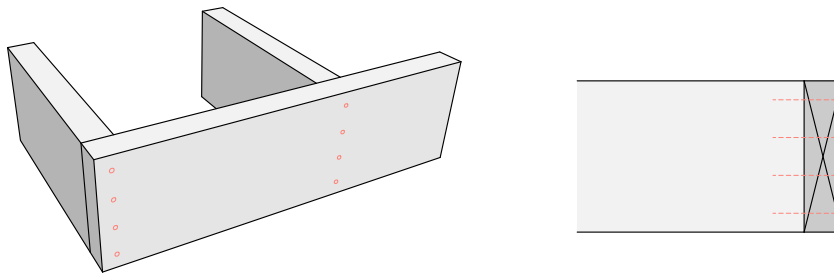

Крепление перекрытия к обвязочному брусу

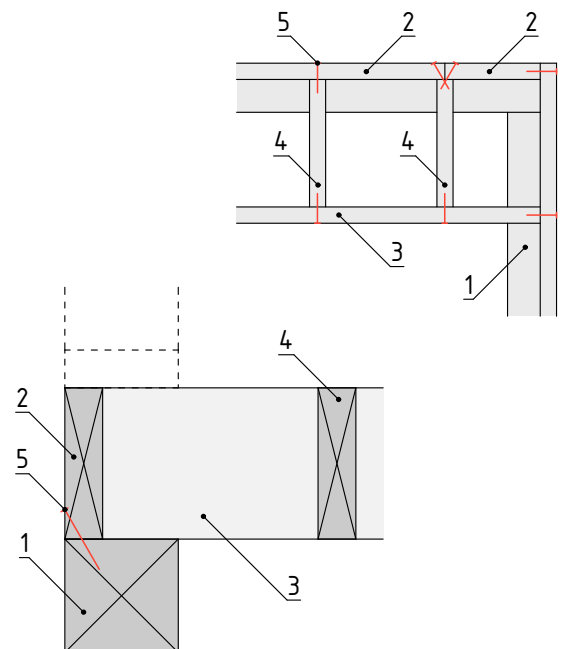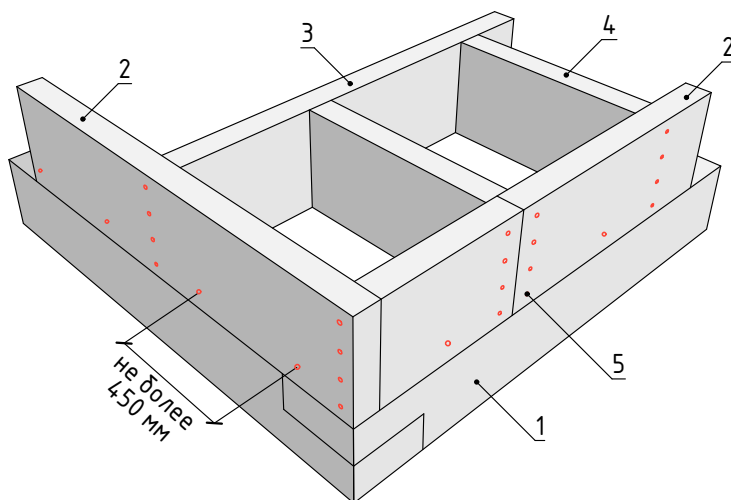


1-Обвязочный брус; 2-Обвязочная доска перекрытия; 3-Балка перекрытия; 4-Распорка (перемычка) ; 5-Гвоздь

		Узлы монтажа элементов перекрытия	Стадия	Лист	Листов
			КР	10	43


Узлы монтажа элементов перекрытия

Крепление распорок (перемычек) под внутренние стены и перегородки, находящиеся поперек балок перекрытия

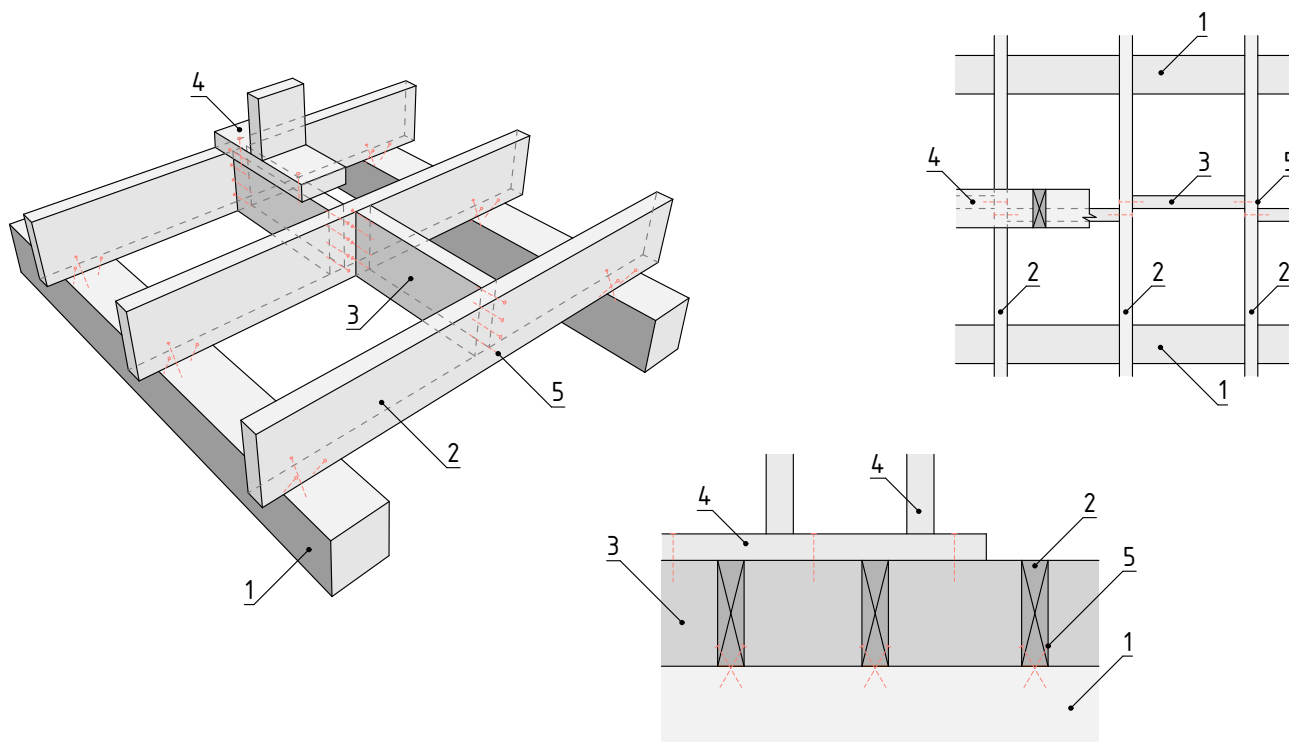

1-Обвязочный брус; 2-Балка перекрытия; 3-Распорка (перемычка); 4-Каркас стены; 5-Гвоздь


Крепление распорок (перемычек) под внутренние стены и перегородки, находящиеся вдоль балок перекрытия

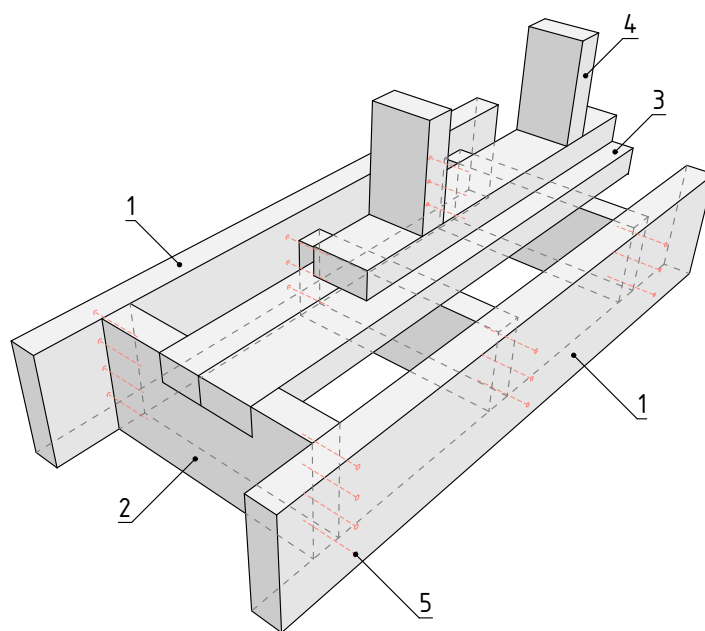

1-Балка перекрытия; 2-Распорка (перемычка) ; 3-Закладной лежень; 4-Каркас стены; 5-Гвоздь


		Узлы монтажа элементов перекрытия	Стадия	Лист	Листов
			КР	11	43

План расположения элементов силового каркаса первого этажа. М1:40

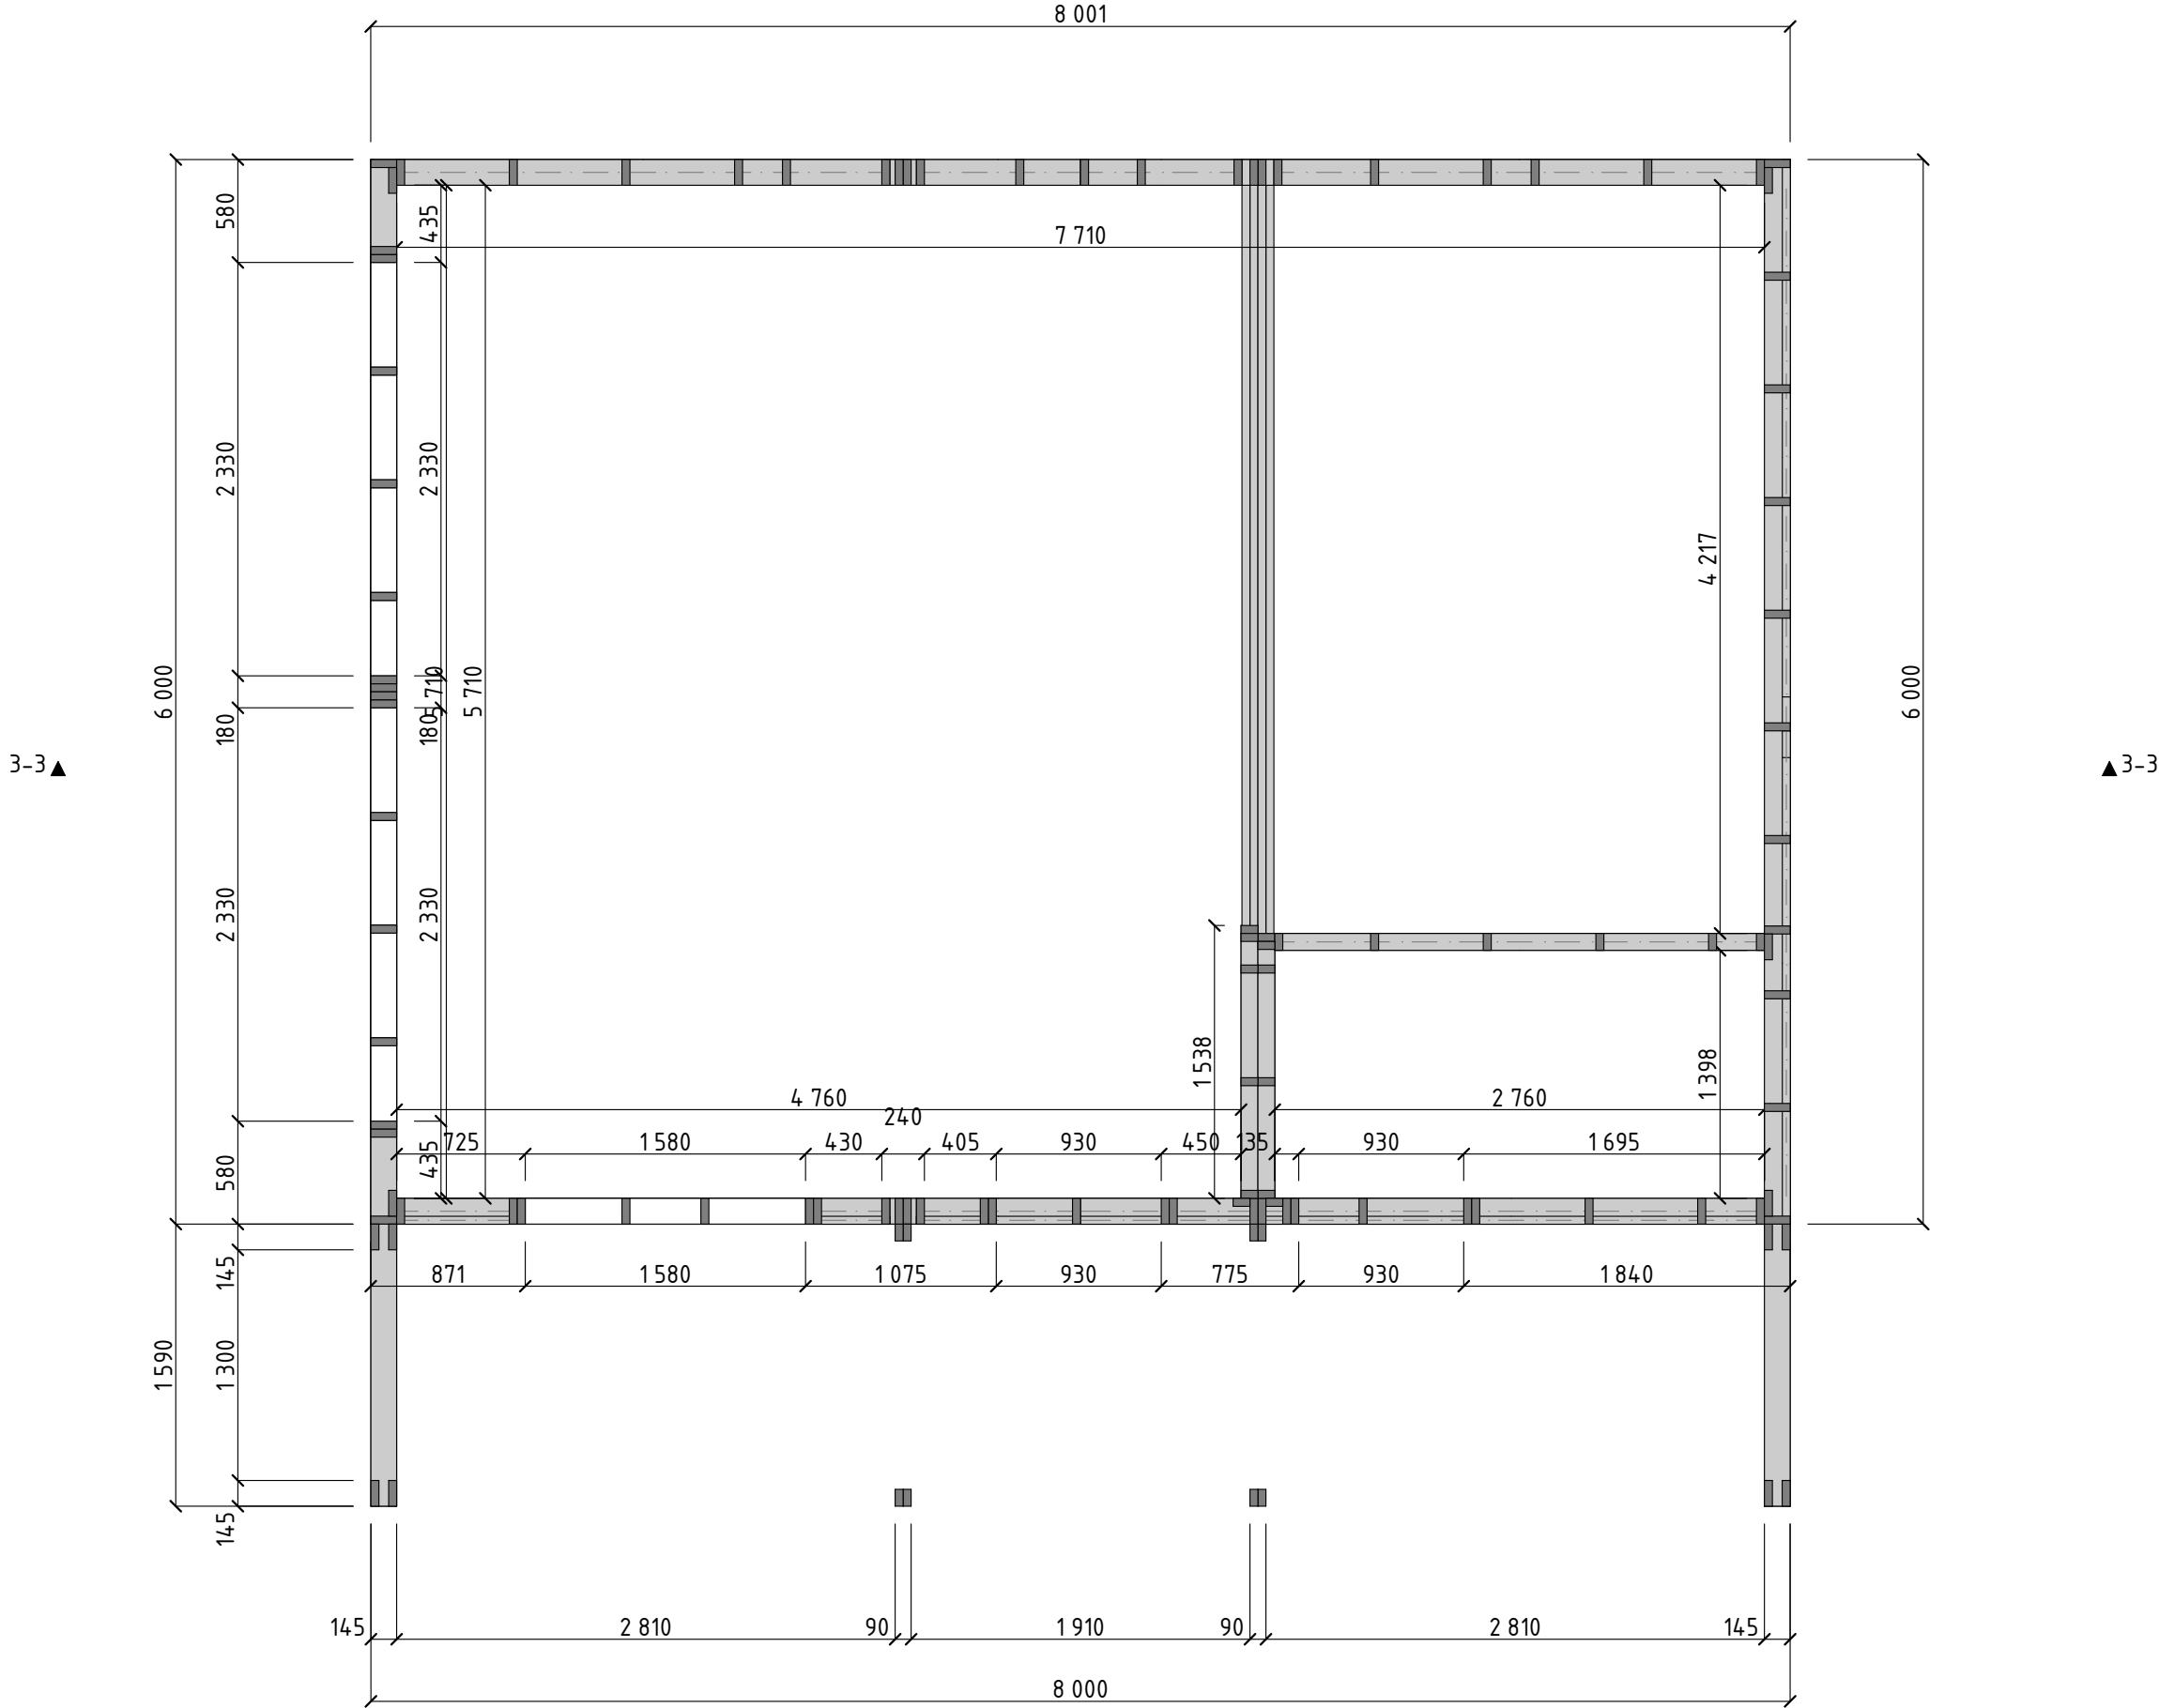

Узлы монтажа стен и перегородок


Монтаж стен и перегородок с закладным лежнем

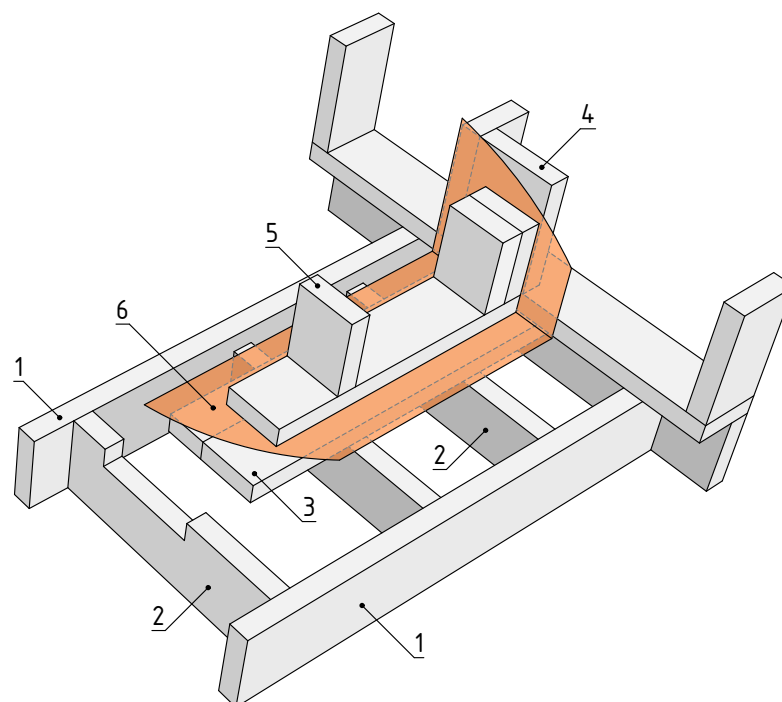

- 1-Балка перекрытия; 2-Распорка (перемычка); 3-Закладной лежень; 4-Каркас внешних стен;
5- Каркас стены/перегородки; 6-Закладная пароизоляция.


До установки стены/перегородки в проектное положение обеспечить монтаж закладной пароизоляции.

Монтаж обрешетки на перекрытие с закладным лежнем

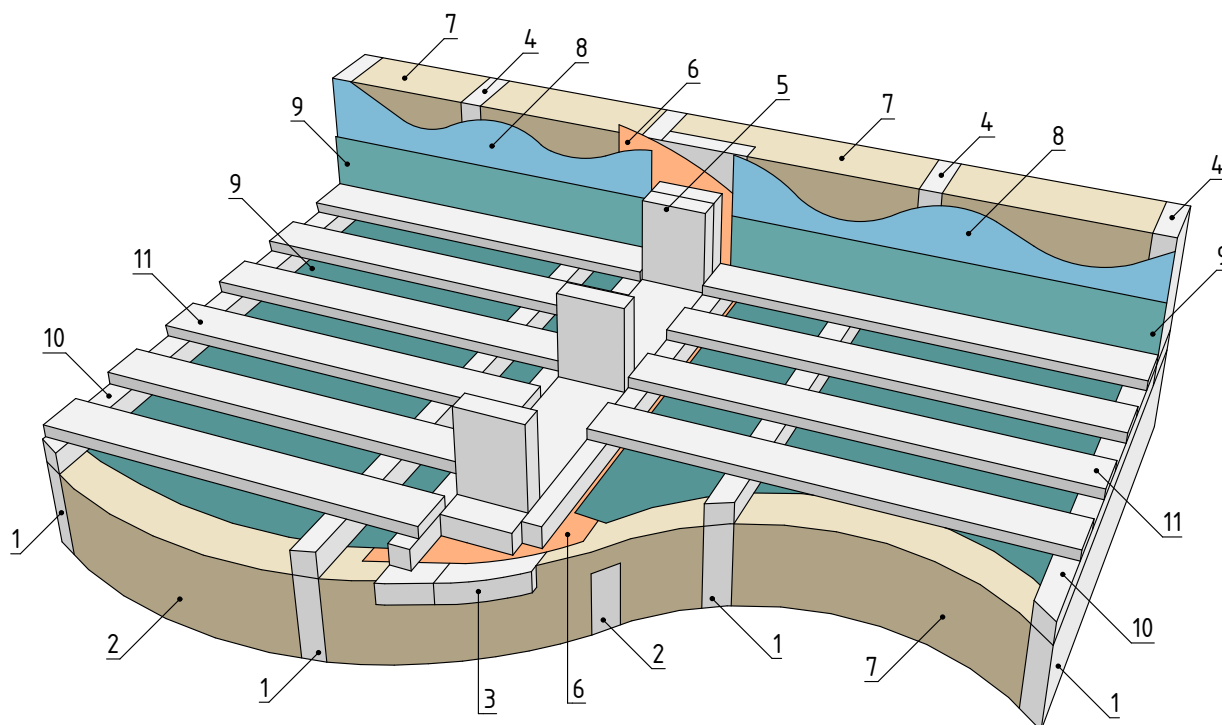

- 1-Балка перекрытия; 2-Распорка (перемычка); 3-Закладной лежень; 4-Каркас внешних стен;
5- Каркас стены/перегородки; 6-Закладная пароизоляция; 7-Утеплитель; 8-Пароизоляция внешней стены;
9-Пароизоляция перекрытия; 10-Контрообрешетка; 11-Обрешетка.



После монтажа пароизоляции внешней стены и пароизоляции перекрытия произвести их склейку с закладной пароизоляцией, обеспечив непрерывность паробарьера.

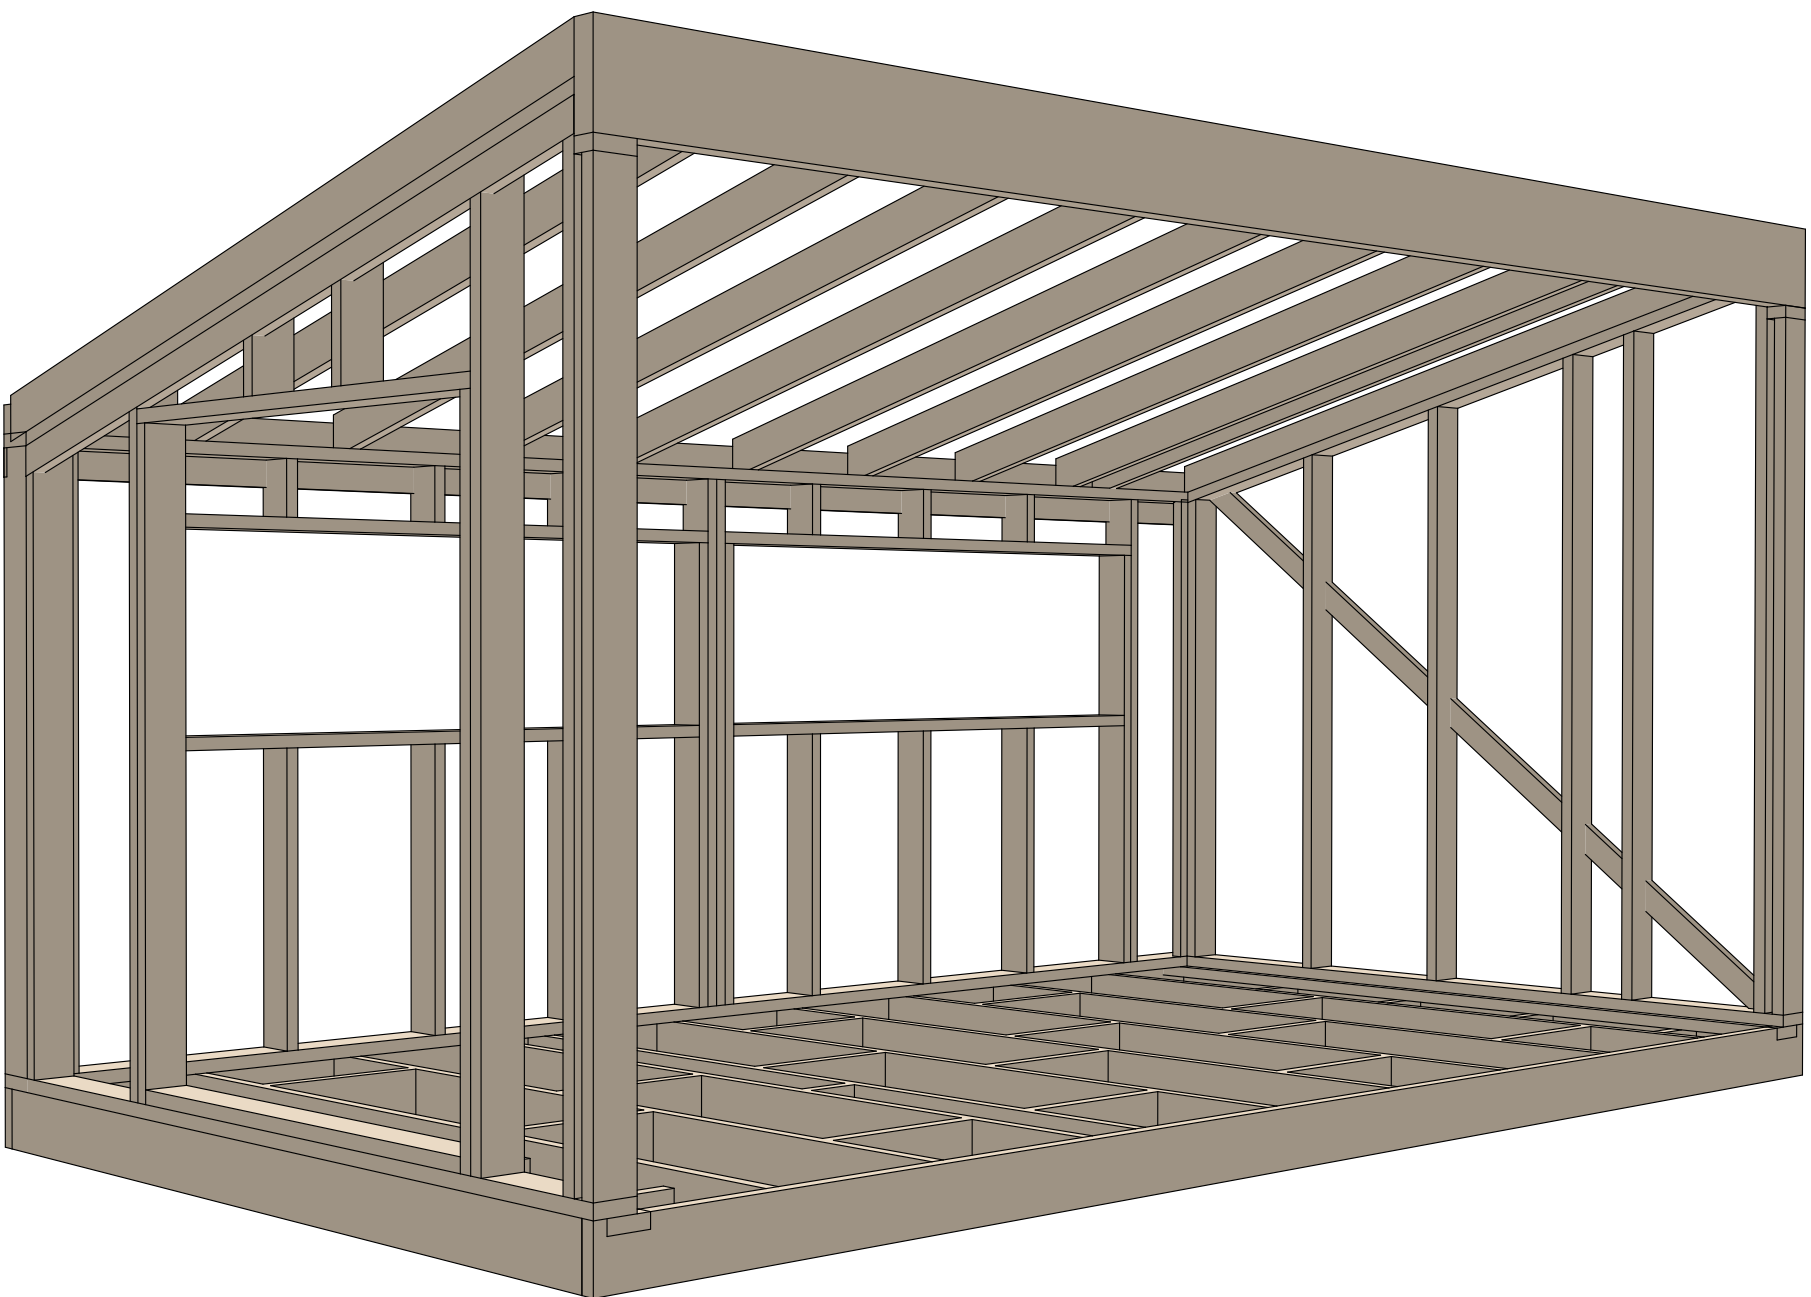

Модуль 1


Смаður	Лусм	Лусмоб
КР	14	43

План расположения элементов перекрытия Модуля 1. М1:30

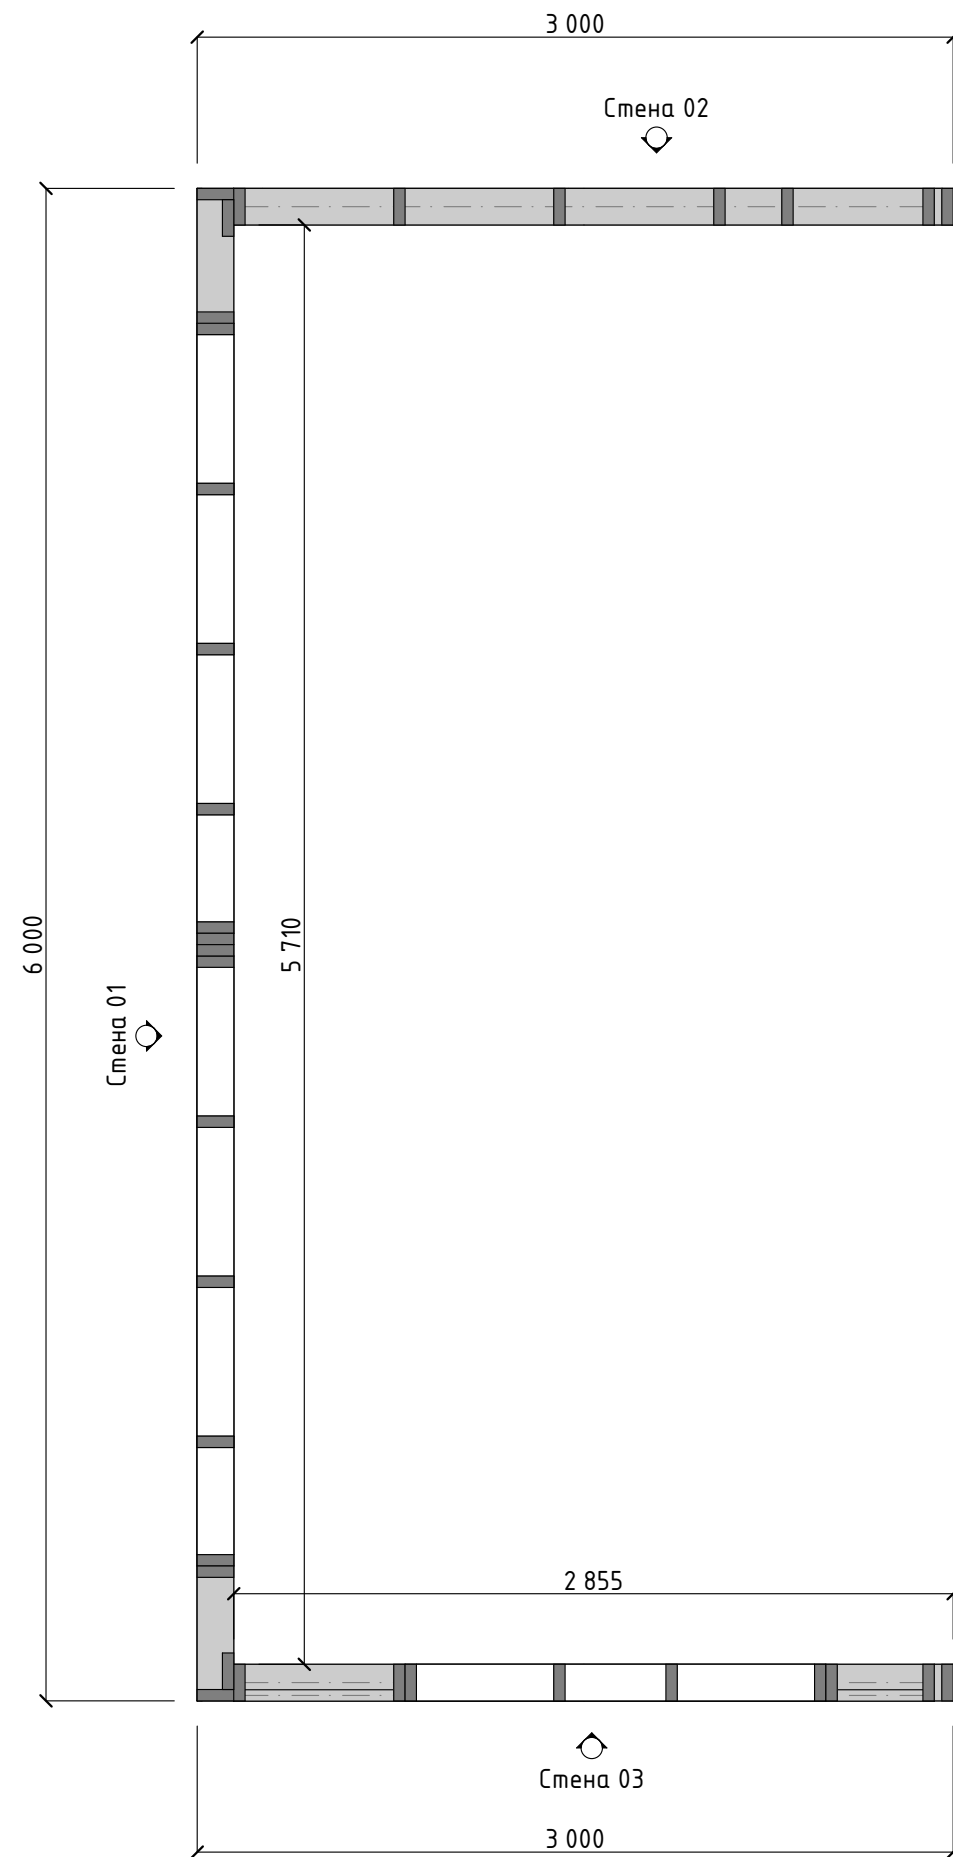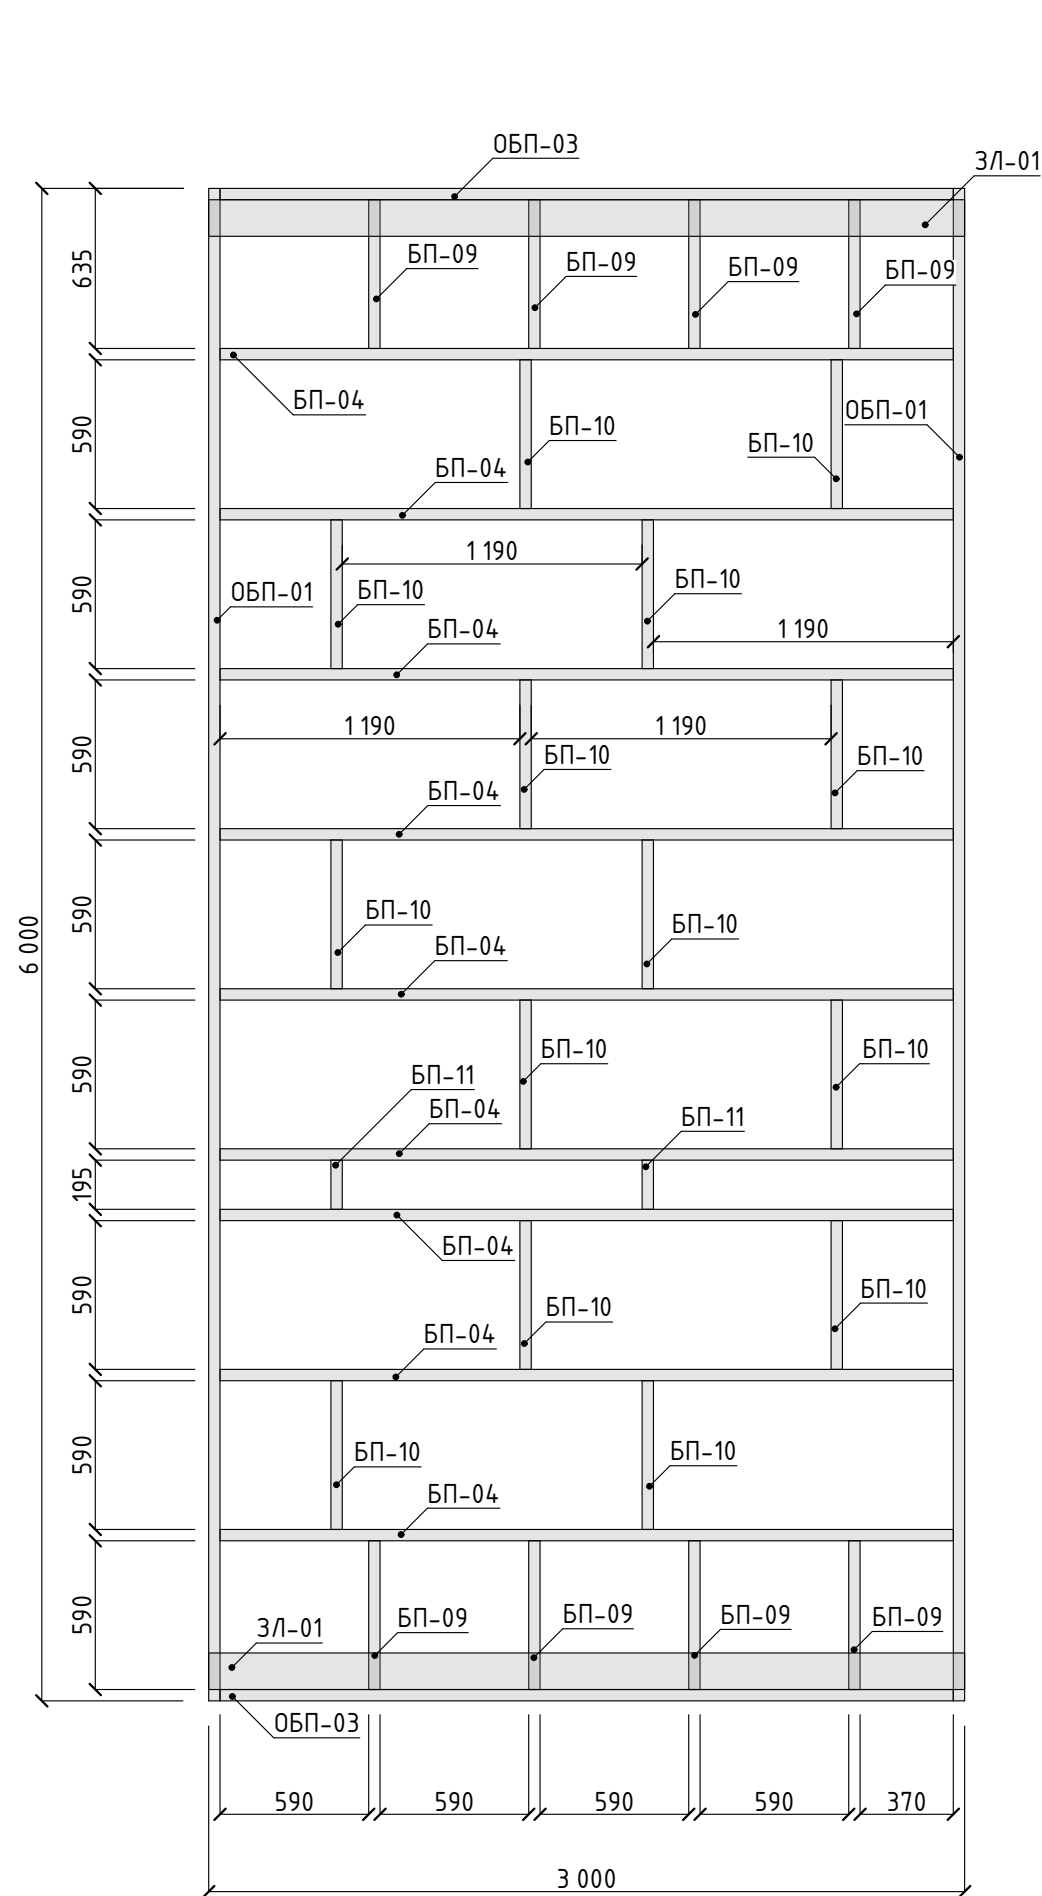


Спецификация элементов перекрытия 1 этажа М1				
Поз.	Ширина, мм	Высота, мм	Длина, мм	Кол-во
БП-04	45	195	2 910	9
БП-09	45	145	590	8
БП-10	45	195	590	14
БП-11	45	195	195	2
ЗЛ-01	145	45	3 000	2
ОБП-01	45	195	6 000	2
ОБП-03	45	195	2 910	2


План расположения элементов стены. Стена 01

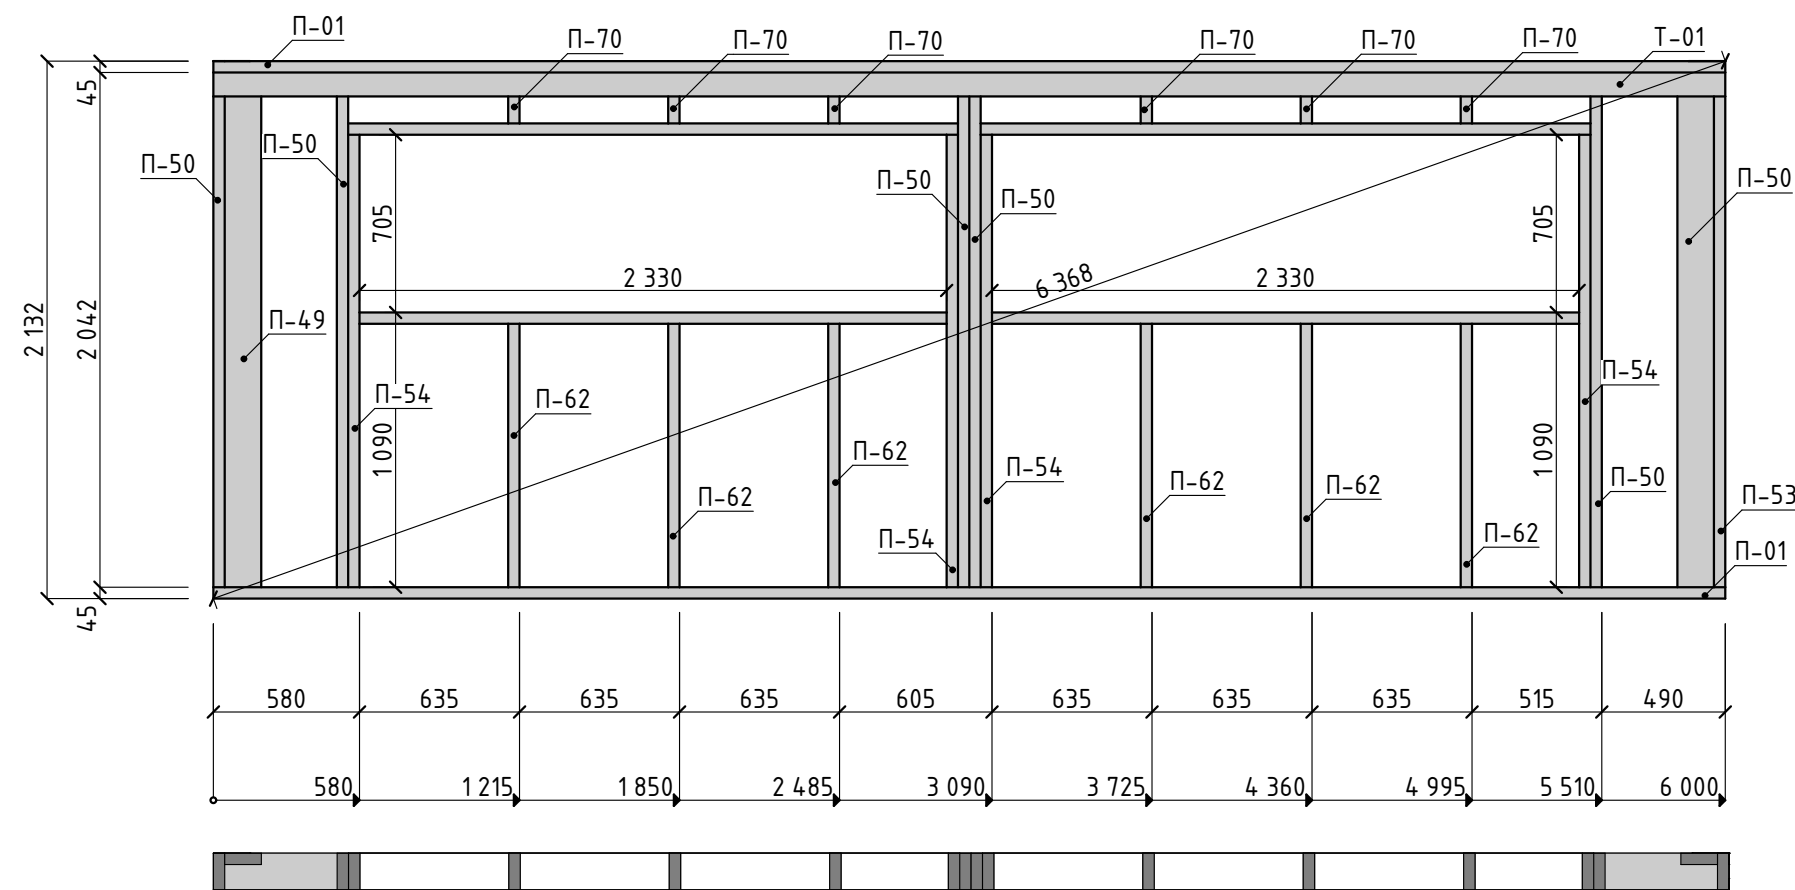


Спецификация элементов Стены 01				
Поз.	Ширина, мм	Высота, мм	Длина, мм	Кол-во
П-01	145	45	6 000	2
П-38	145	45	2 420	2
П-40	145	45	2 330	2
П-49	145	45	2 052	1
П-50	145	45	2 042	7
П-54	145	45	1 795	4
П-62	145	45	1 045	6
П-70	145	45	202	6
Т-01	20	95	6 000	1

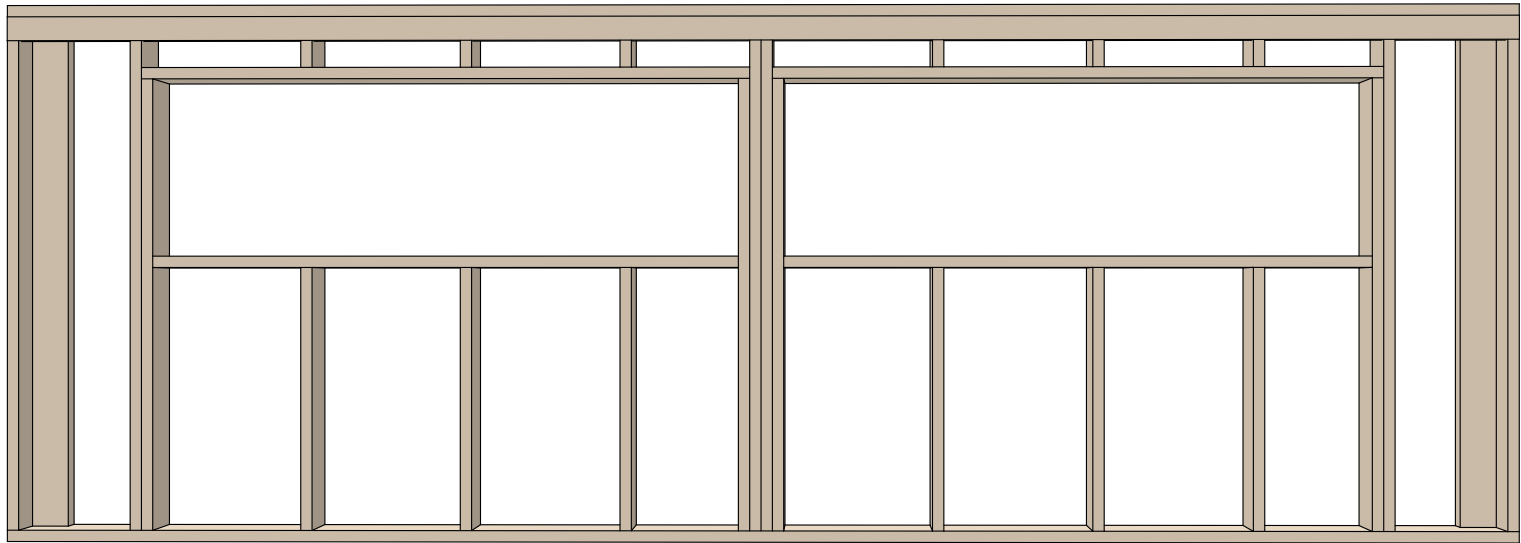


План расположения элументов стен. Стена 02

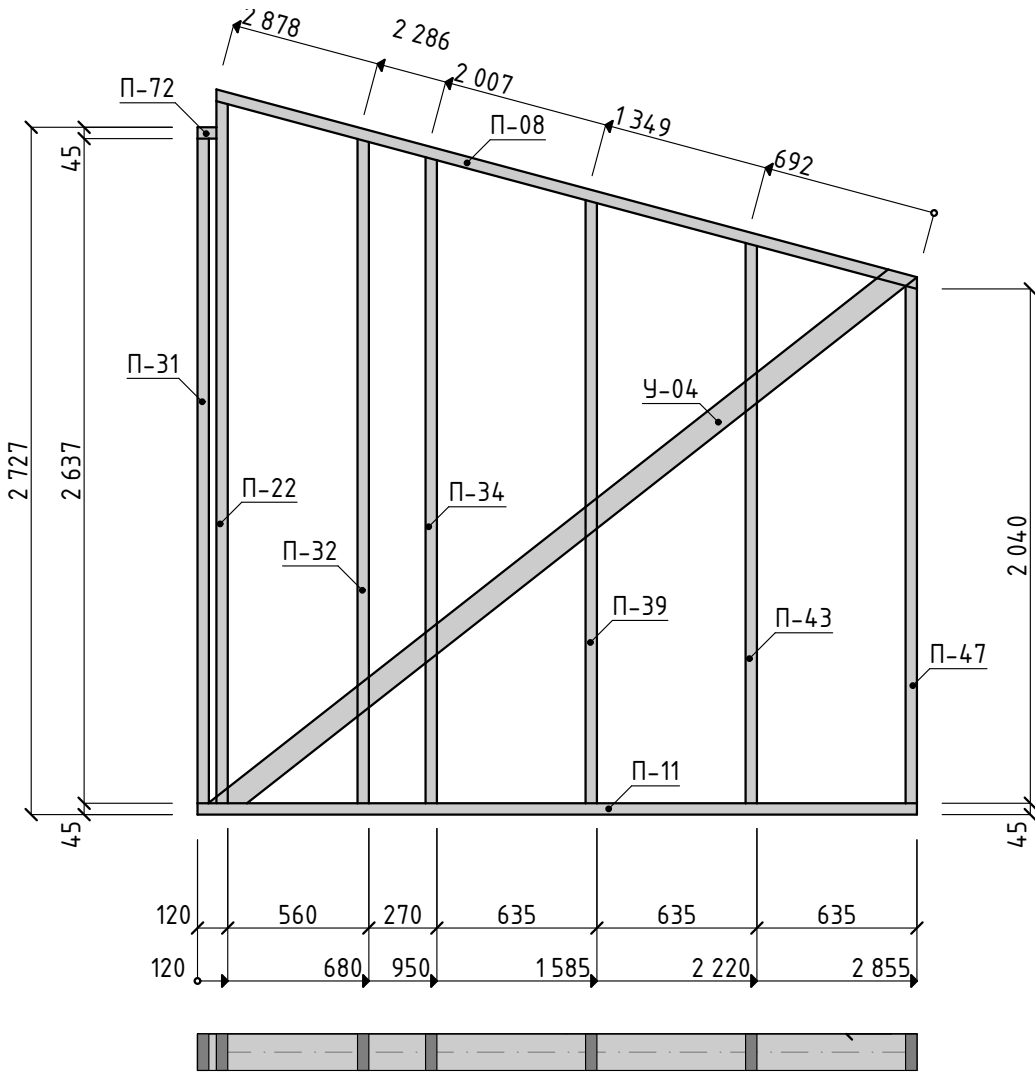


Спецификация элементов Стены 02				
Поз.	Ширина, мм	Высота, мм	Длина, мм	Кол-во
П-08	145	45	2 890	1
П-11	145	45	2 855	1
П-22	145	45	2 785	1
П-31	145	45	2 637	1
П-32	145	45	2 635	1
П-34	145	45	2 563	1
П-39	145	45	2 393	1
П-43	145	45	2 223	1
П-47	145	45	2 052	1
П-72	145	45	75	1
У-04	45	95	3 501	1

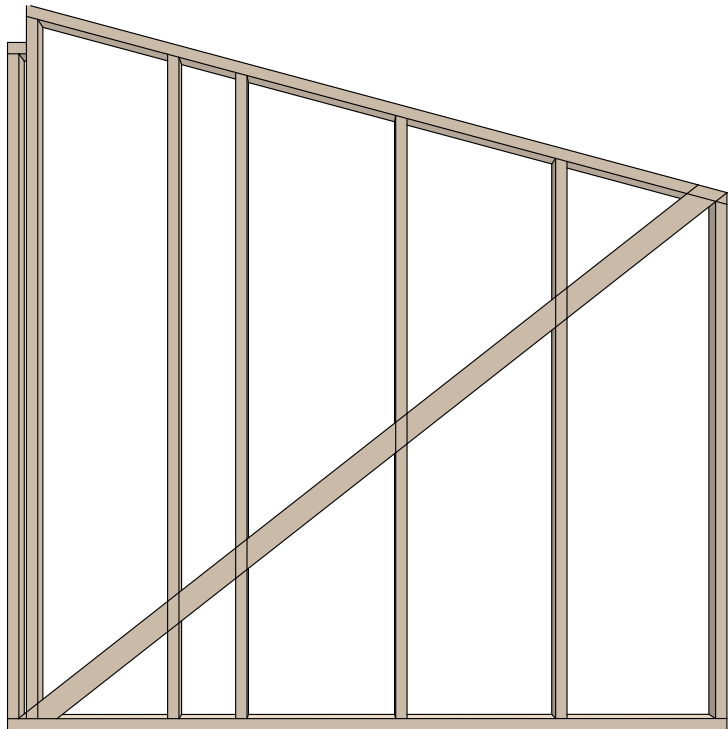



План расположения элементов стены. Стена 03

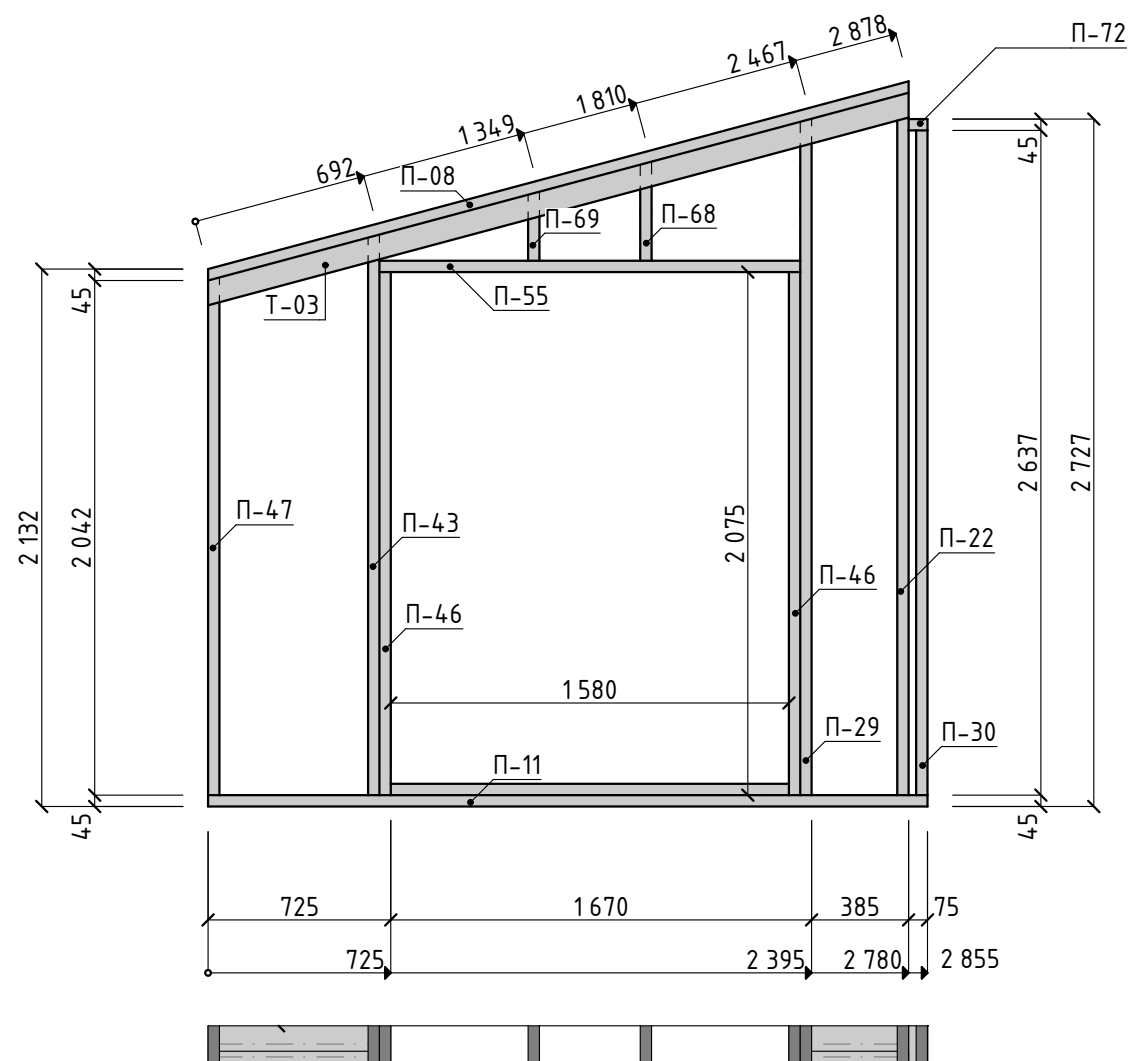


Спецификация элементов Стены 03				
Поз.	Ширина, мм	Высота, мм	Длина, мм	Кол-во
П-08	145	45	2 890	1
П-11	145	45	2 855	1
П-22	145	45	2 785	1
П-29	145	45	2 682	1
П-30	145	45	2 637	1
П-43	145	45	2 223	1
П-46	145	45	2 075	2
П-47	145	45	2 052	1
П-55	145	45	1 670	1
П-57	145	45	1 580	1
П-68	145	45	392	1
П-69	145	45	273	1
П-72	145	45	75	1
Т-03	45	95	2 904	1

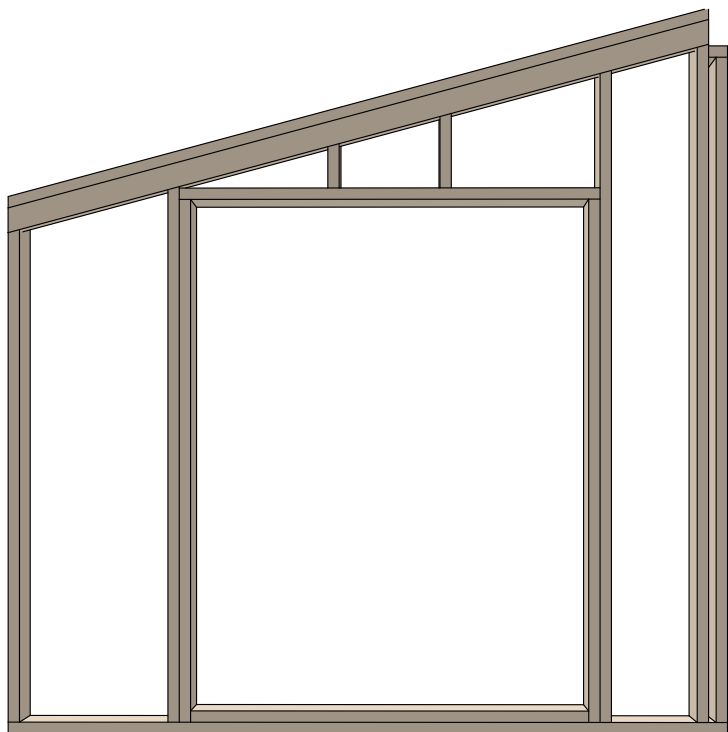


Стропильная система Модуля 1

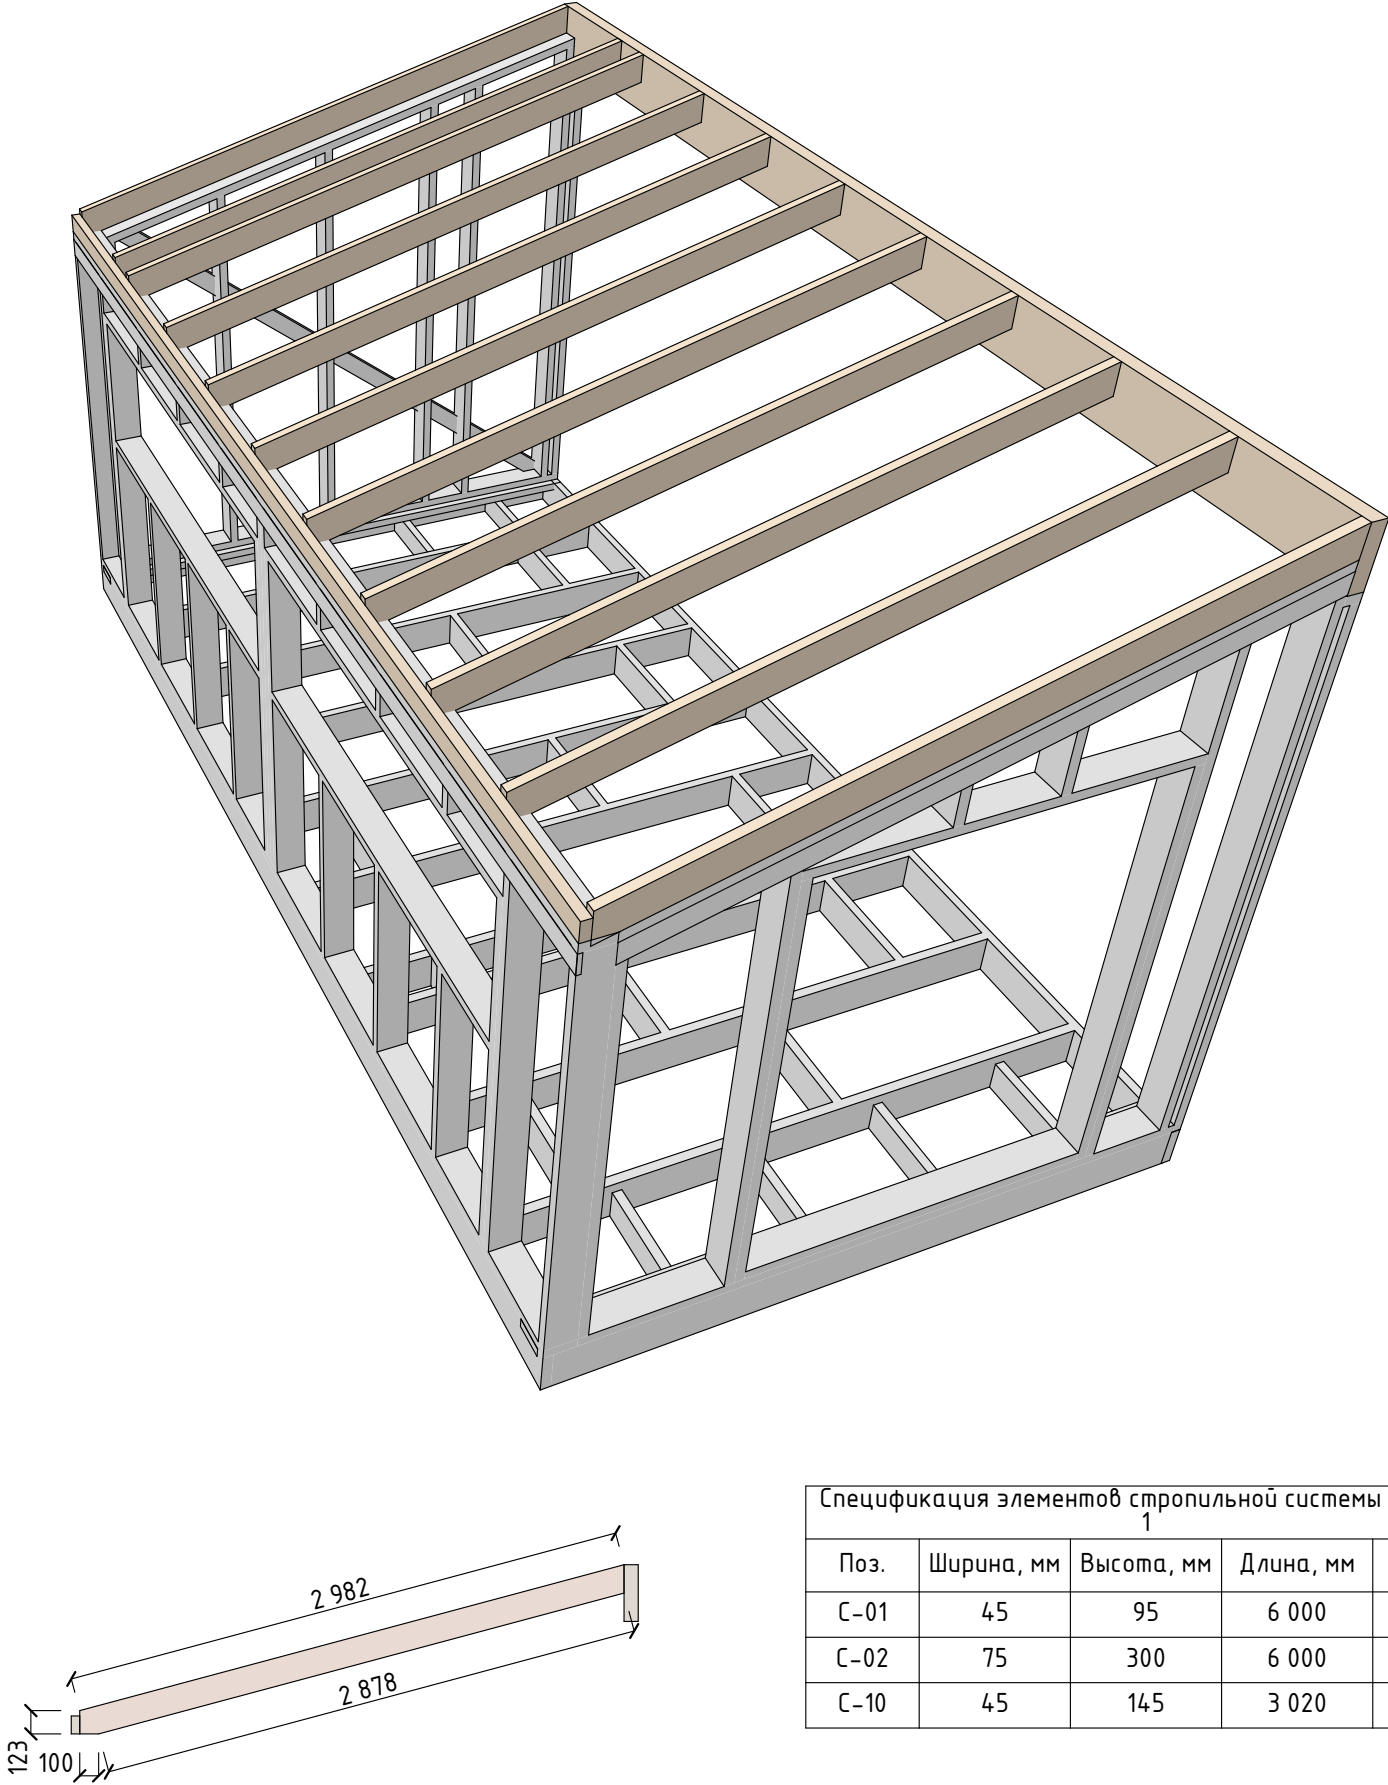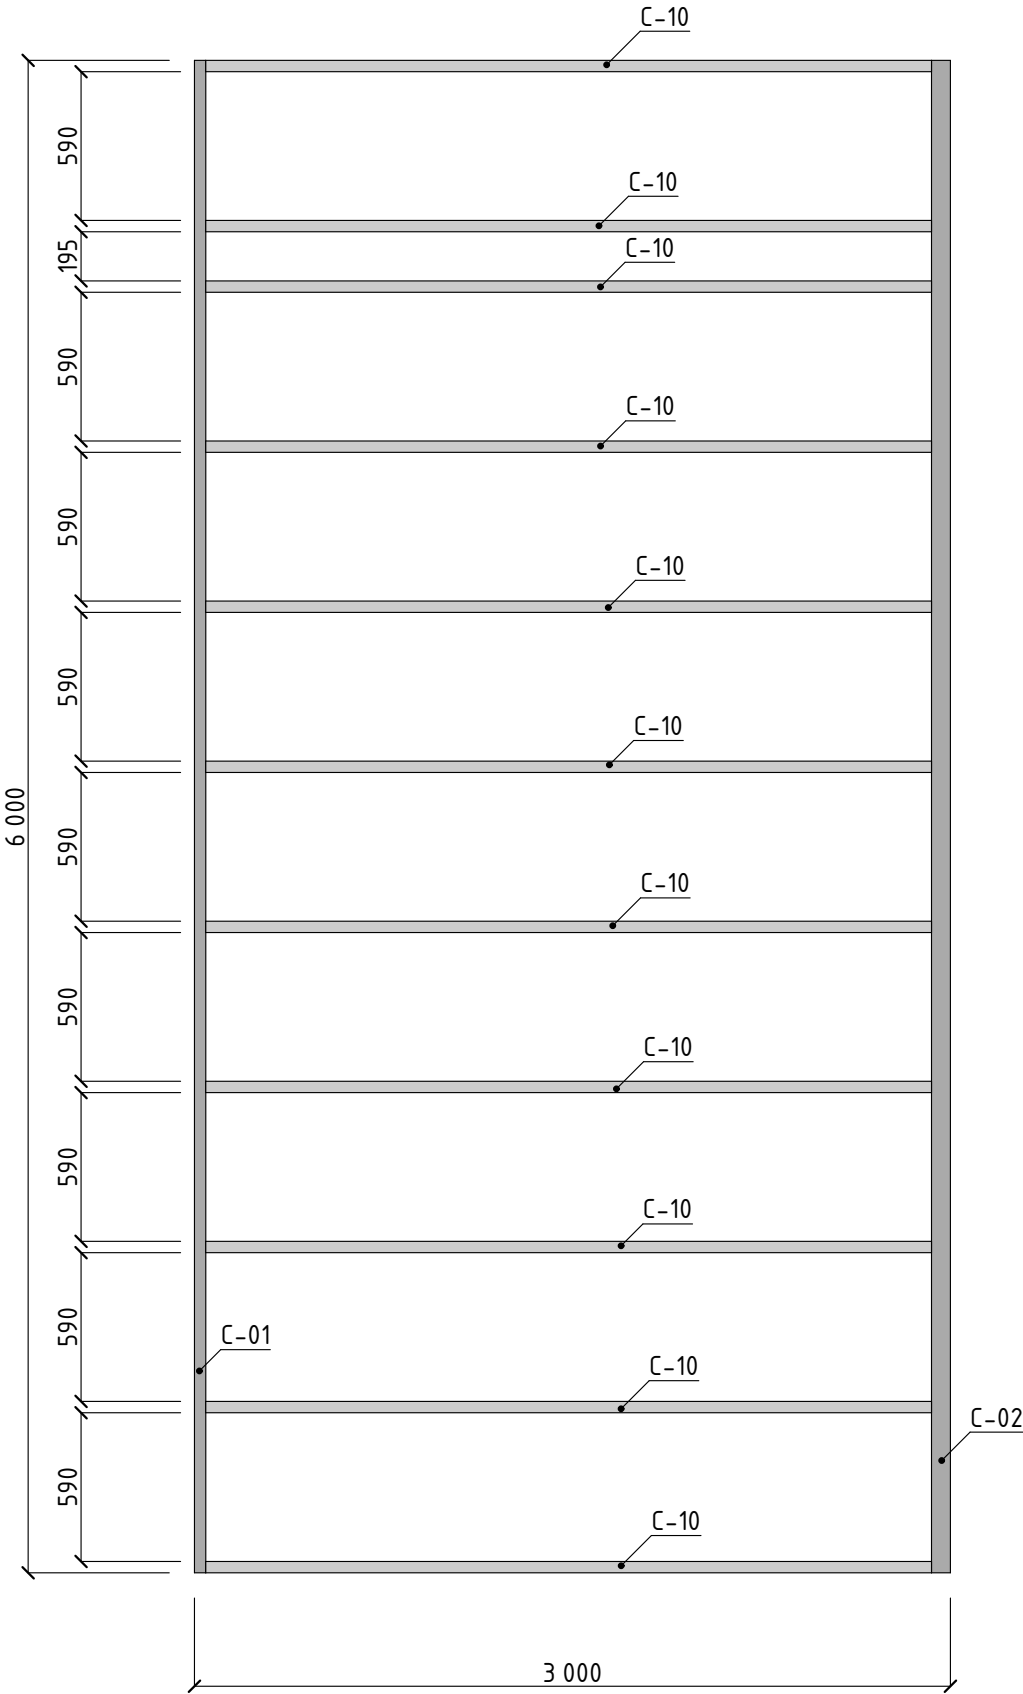

Спецификация элементов стропильной системы Модуля 1				
Поз.	Ширина, мм	Высота, мм	Длина, мм	Кол-во
С-01	45	95	6 000	1
С-02	75	300	6 000	1
С-10	45	145	3 020	11


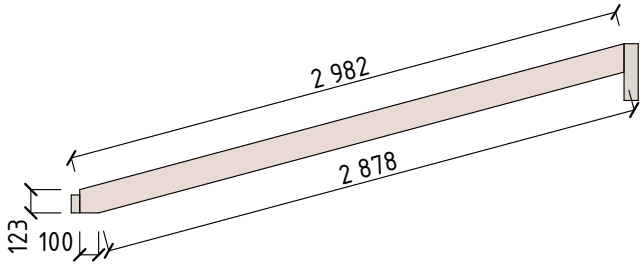


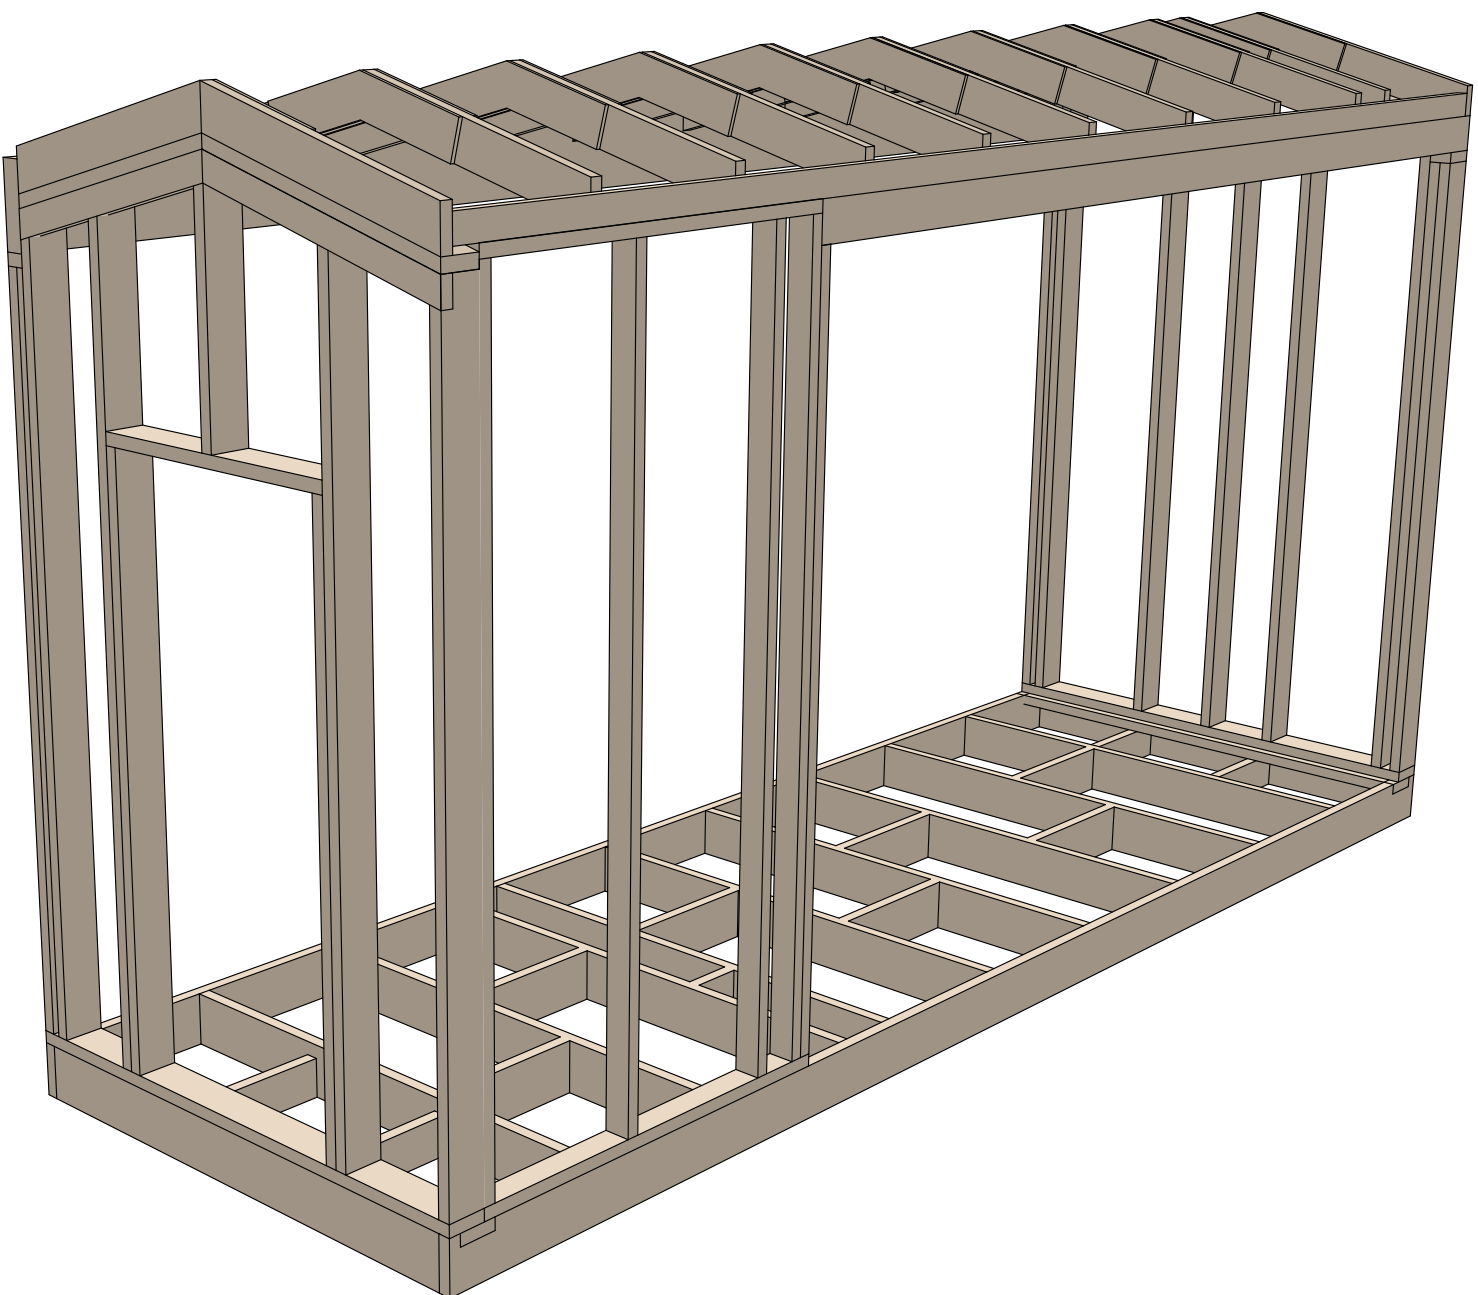

Модуль 2

Склад	Лист	Листов
КР	20	43


План расположения перекрытия Модуля 2. М1:30

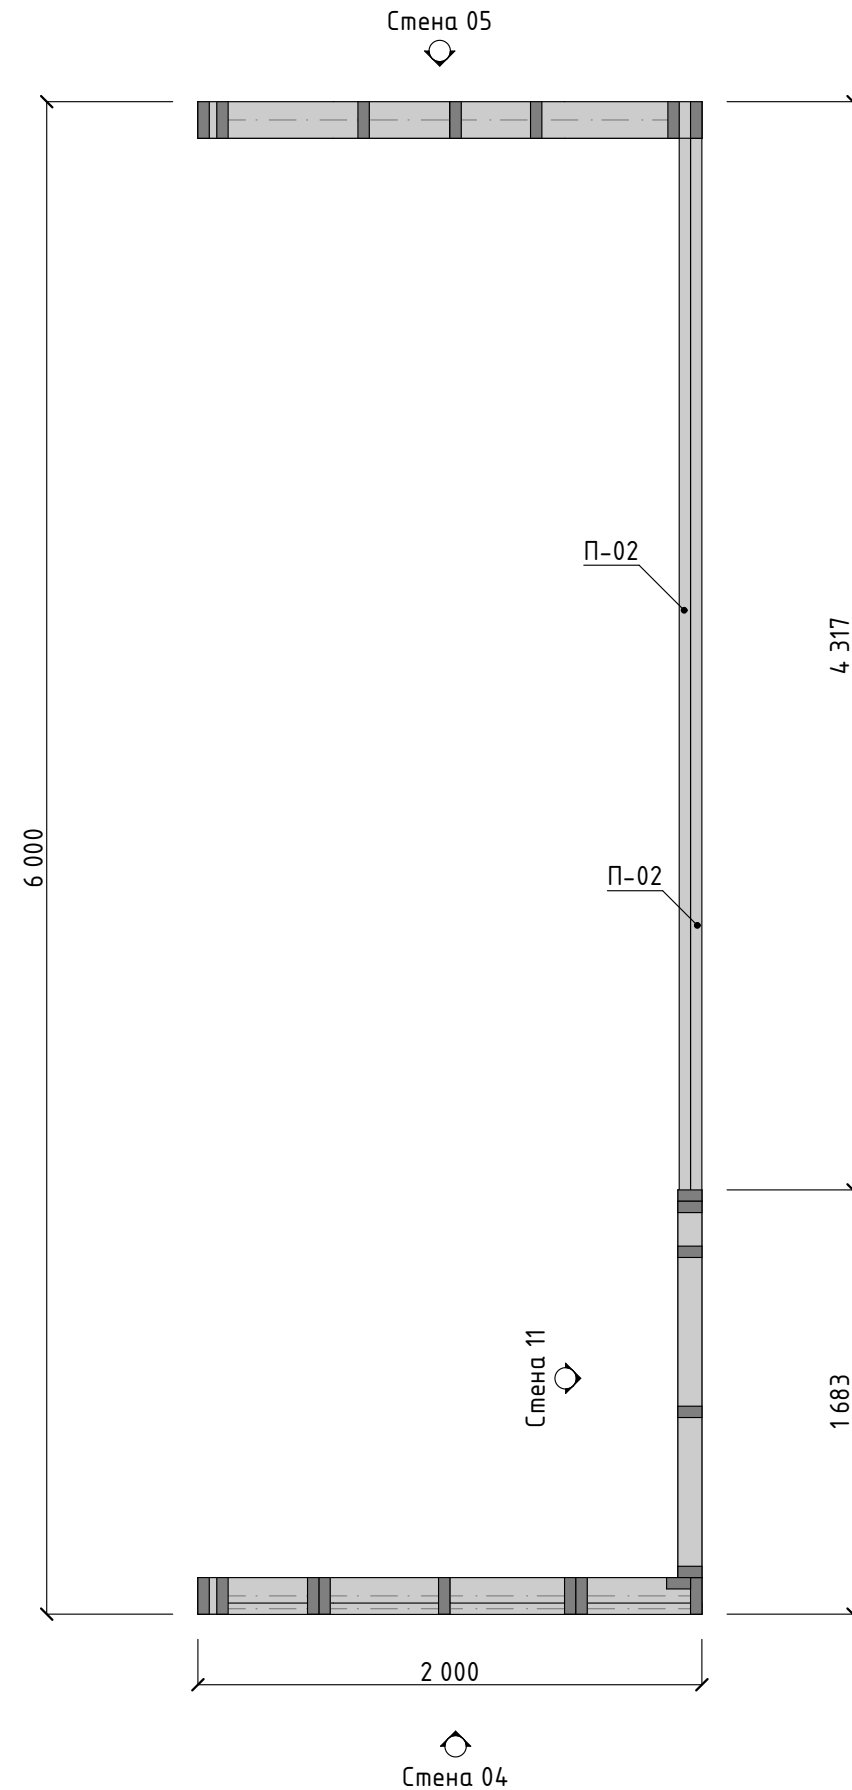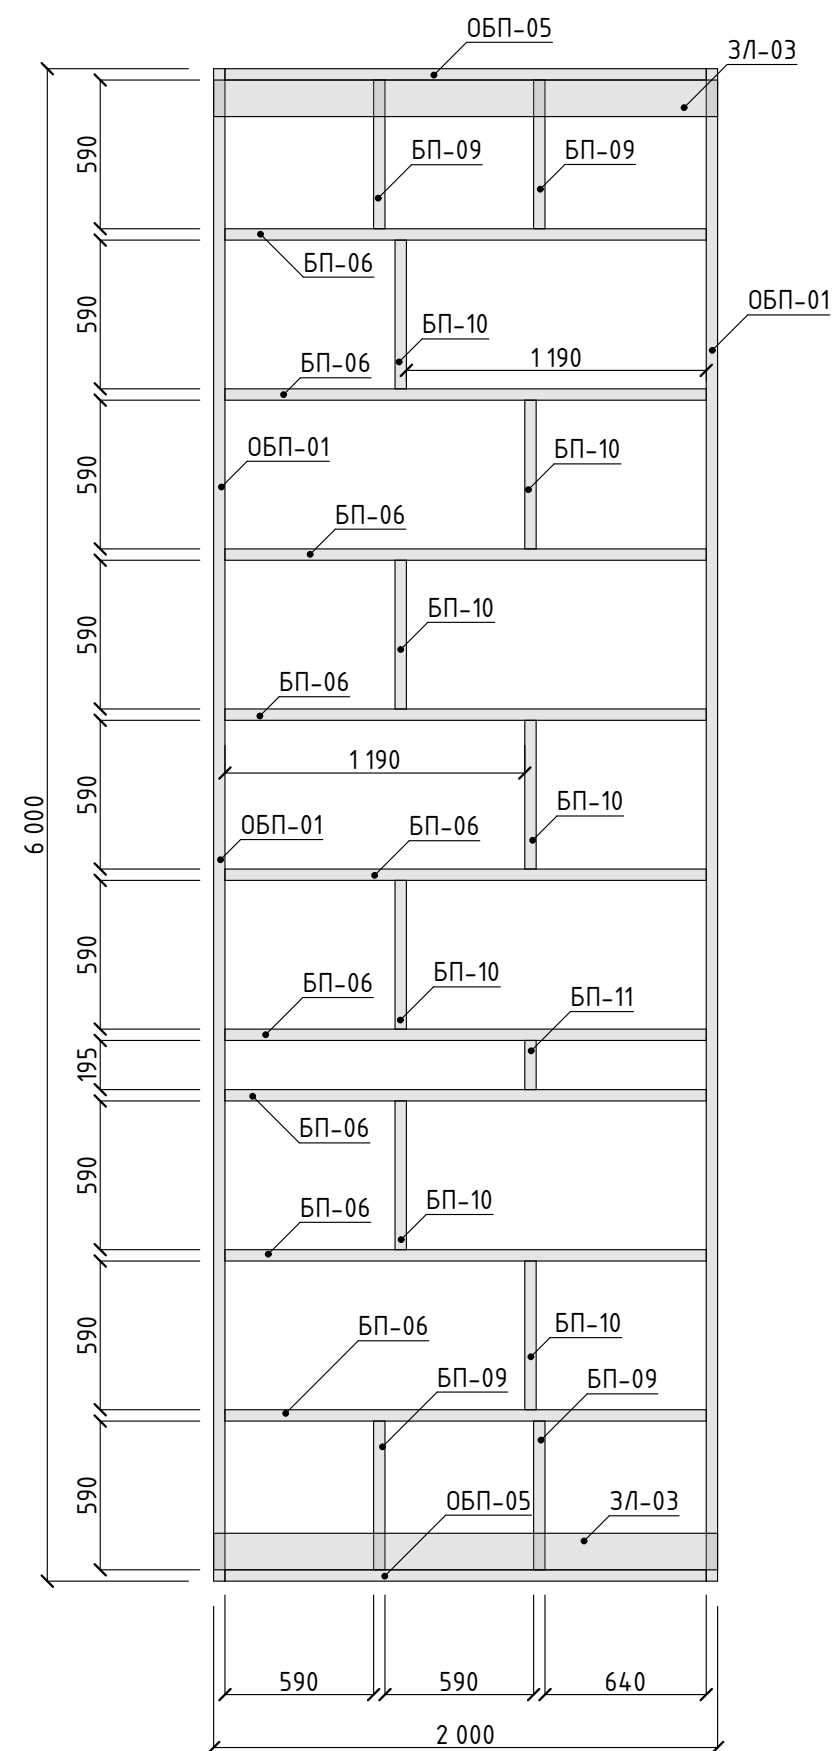

Спецификация элементов перекрытия 1 этажа М2				
Поз.	Ширина, мм	Высота, мм	Длина, мм	Кол-во
БП-06	45	195	1 910	9
БП-09	45	145	590	4
БП-10	45	195	590	7
БП-11	45	195	195	1
ЗЛ-03	145	45	2 000	2
ОБП-01	45	195	6 000	2
ОБП-05	45	195	1 910	2


Спецификация элементов Модуля 2				
Поз.	Ширина, мм	Высота, мм	Длина, мм	Кол-во
П-02	45	145	4 362	2

План расположения элементов стен. Стена 04

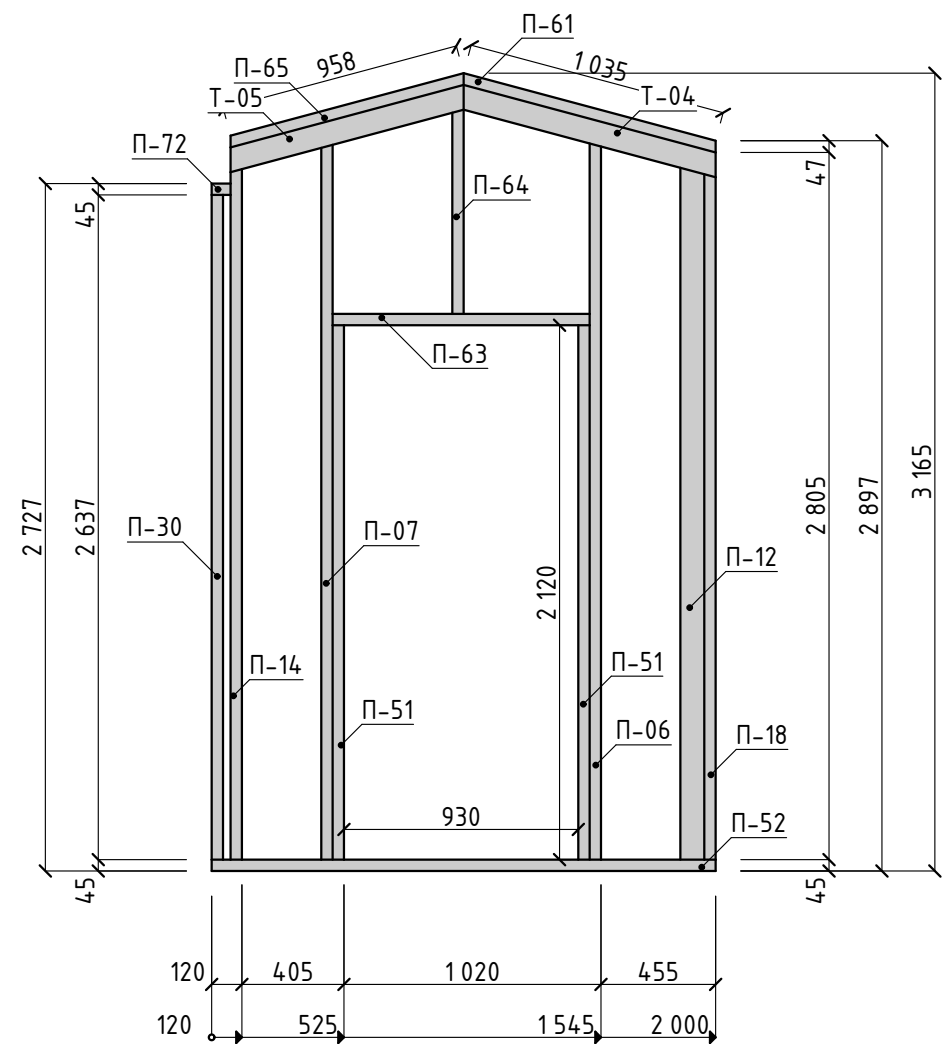


Спецификация элементов Стены 04				
Поз.	Ширина, мм	Высота, мм	Длина, мм	Кол-во
П-06	145	45	2 939	1
П-07	145	45	2 934	1
П-12	45	95	2 843	1
П-14	145	45	2 838	1
П-18	145	45	2 817	1
П-30	145	45	2 637	1
П-51	145	45	2 120	2
П-52	145	45	2 000	1
П-61	145	45	1 047	1
П-63	145	45	1 020	1
П-64	145	45	908	1
П-65	145	45	970	1
П-72	145	45	75	1
Т-04	45	95	1 061	1
Т-05	45	95	983	1


План расположения элементов стен.Стена 05

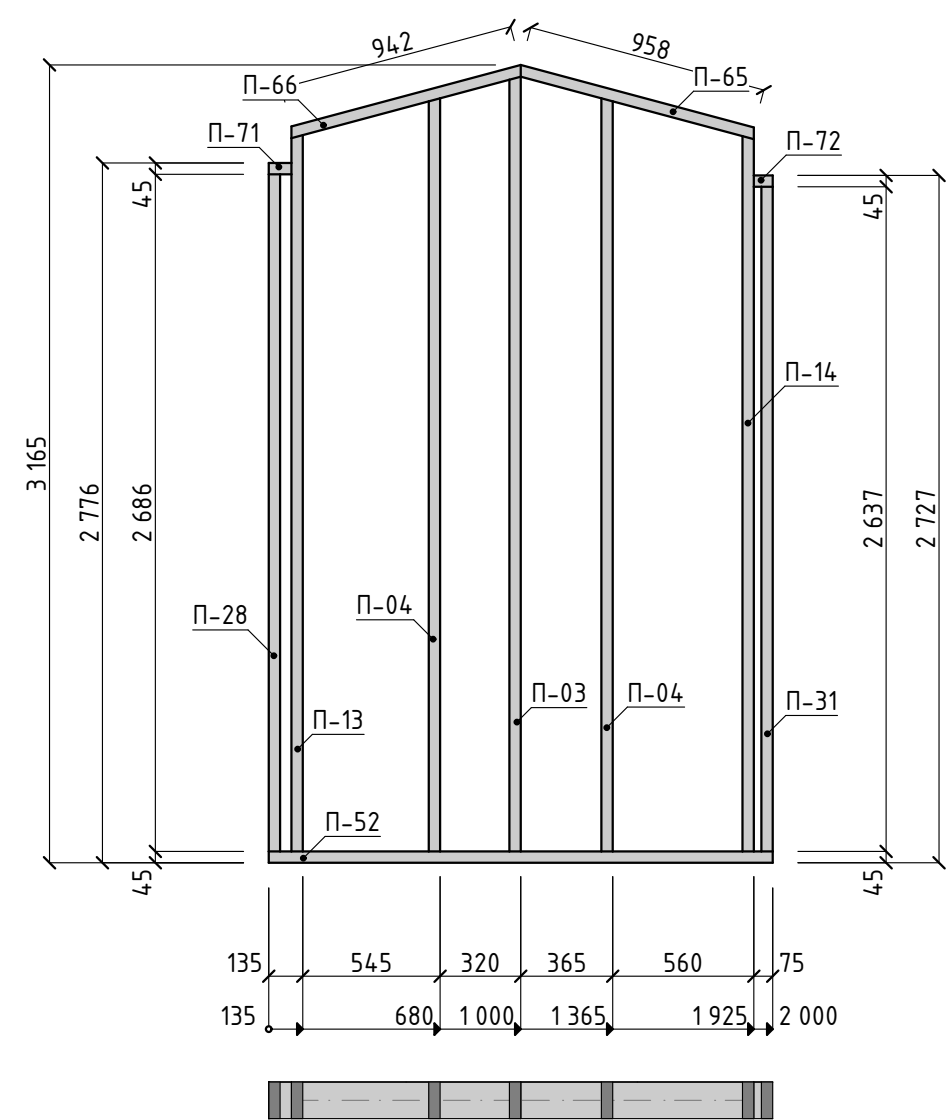


Спецификация элементов Стены 05				
Поз.	Ширина, мм	Высота, мм	Длина, мм	Кол-во
П-03	145	45	3 073	1
П-04	145	45	2 988	2
П-13	145	45	2 842	1
П-14	145	45	2 838	1
П-28	145	45	2 686	1
П-31	145	45	2 637	1
П-52	145	45	2 000	1
П-65	145	45	970	1
П-66	145	45	954	1
П-71	145	45	90	1
П-72	145	45	75	1

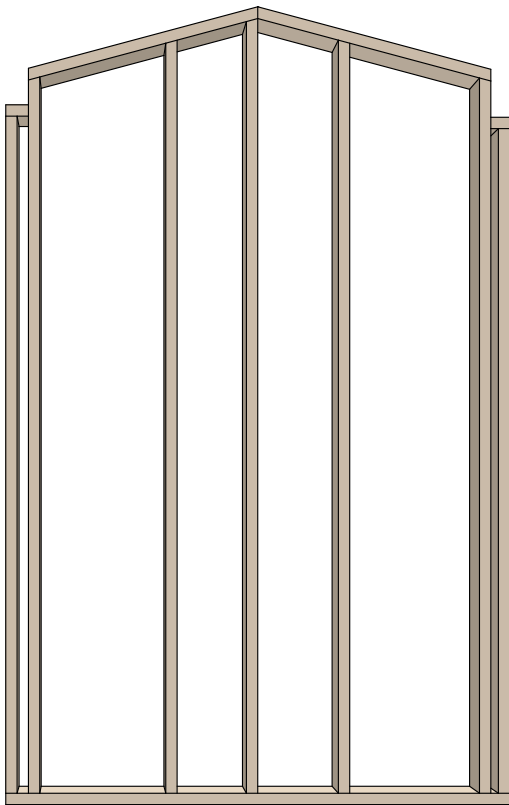



План расположения элементов стен. Стена 11

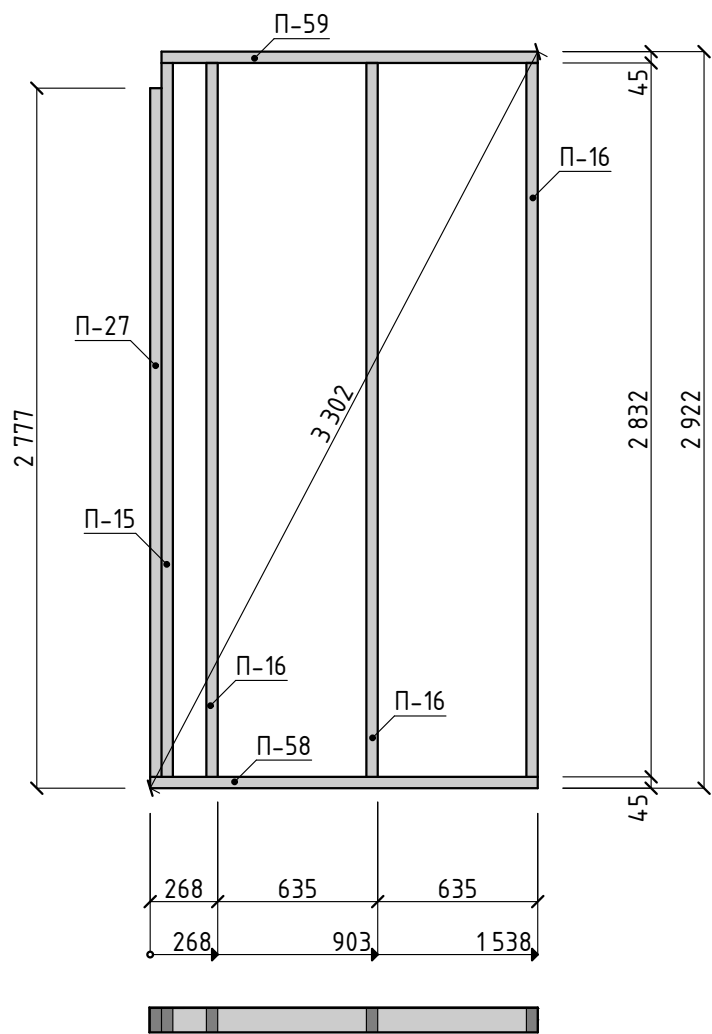


Спецификация элементов Стены 11				
Поз.	Ширина, мм	Высота, мм	Длина, мм	Кол-во
П-15	95	45	2 832	1
П-16	95	45	2 832	3
П-27	95	45	2 732	1
П-58	95	45	1 538	1
П-59	95	45	1 493	1

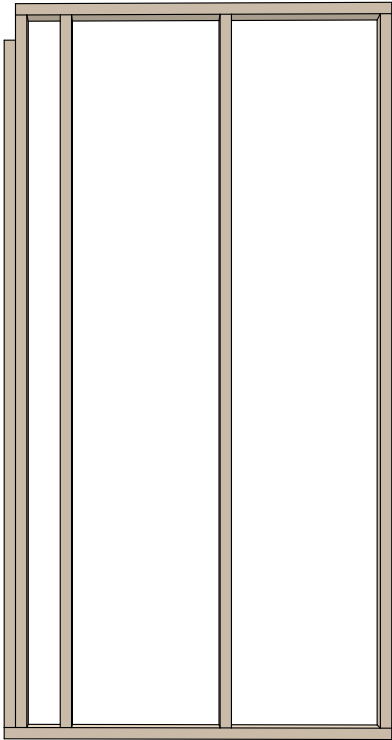


Стропильная система Модуля 2

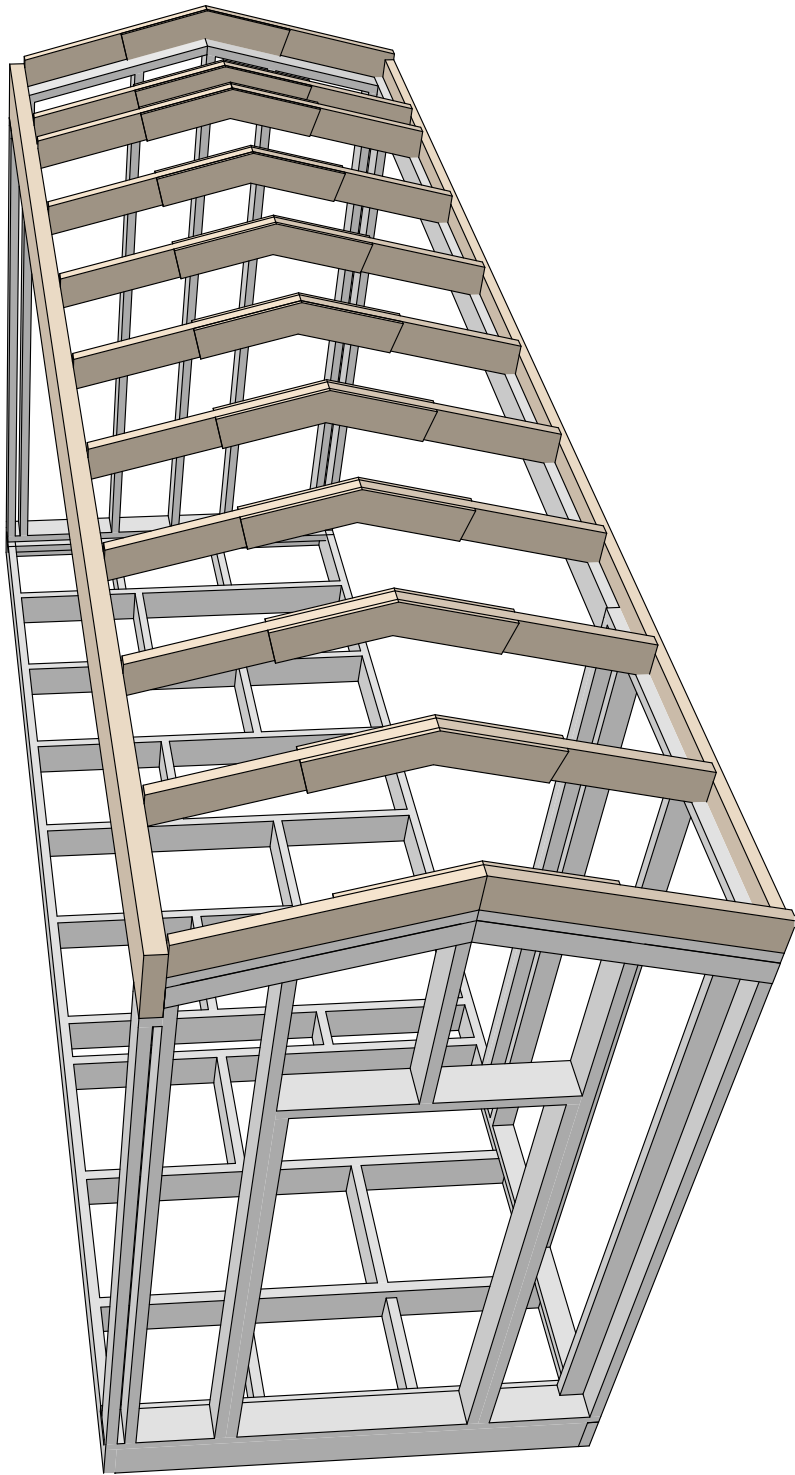
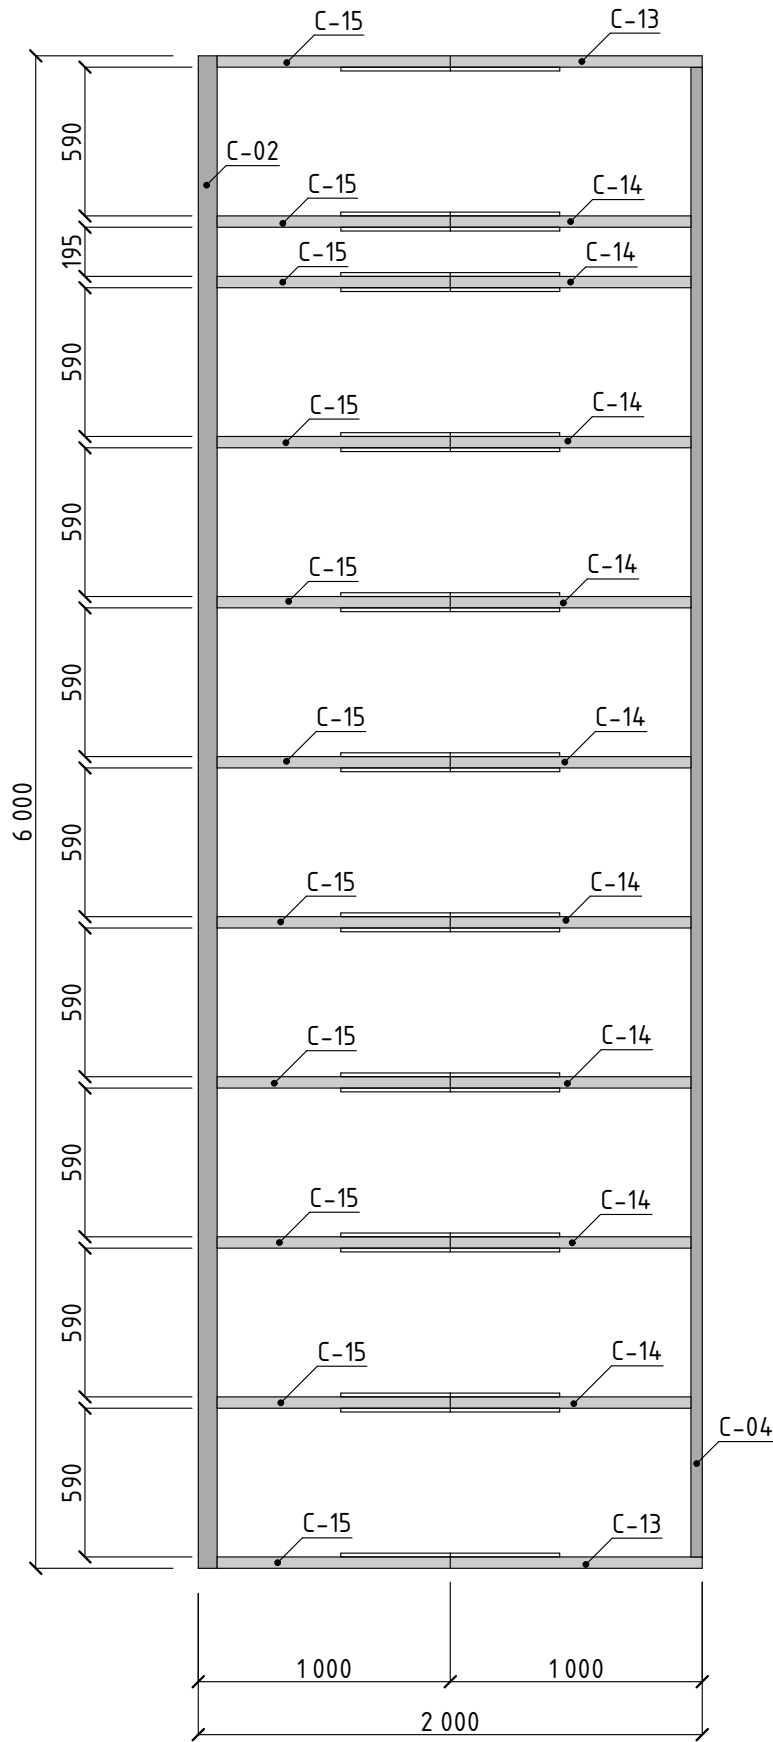


Спецификация элементов стропильной системы Модуля 2				
Поз.	Ширина, мм	Высота, мм	Длина, мм	Кол-во
С-02	75	300	6 000	1
С-04	45	95	5 910	1
С-13	45	145	1 074	2
С-14	45	145	1 028	9
С-15	45	145	996	11

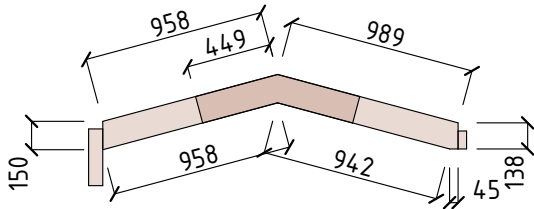

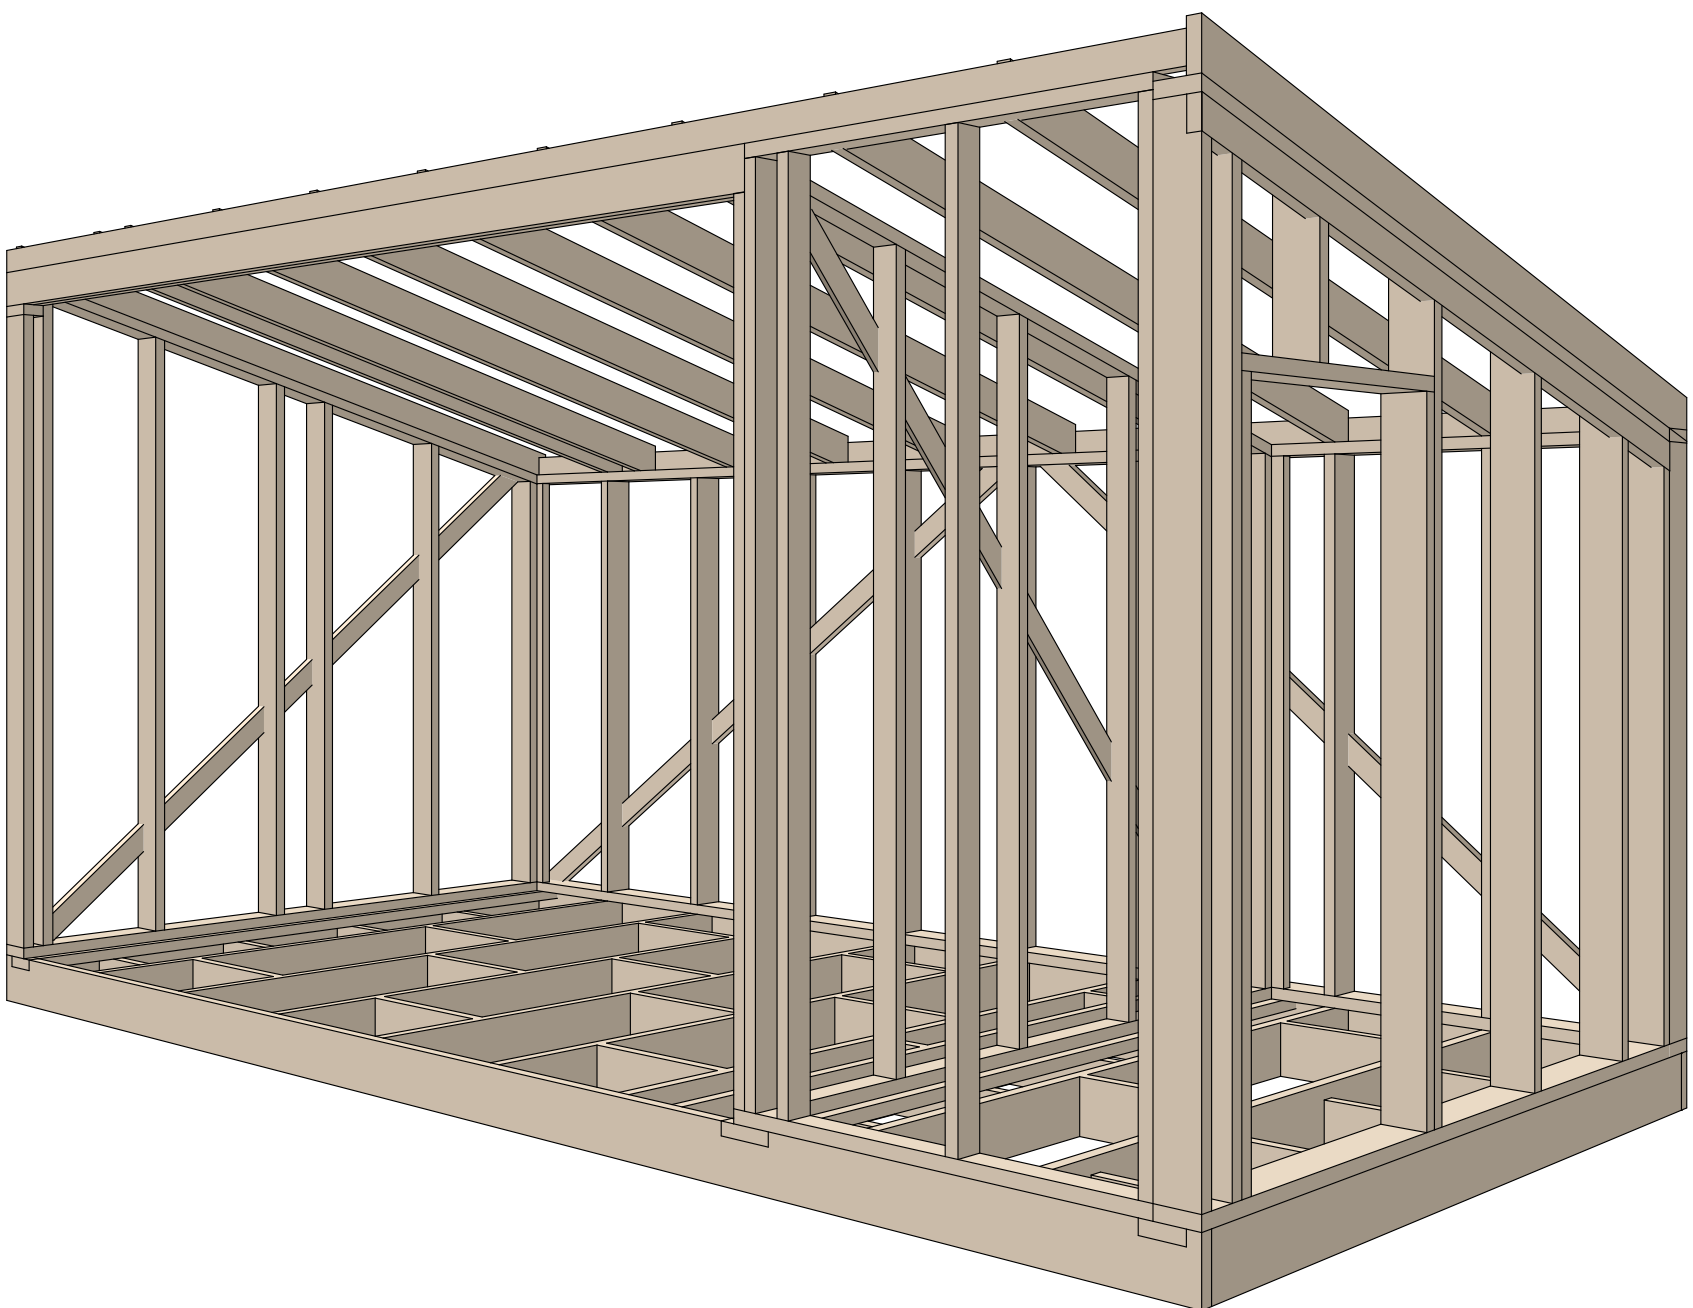


План расположения элементов перекрытия Модуля 3

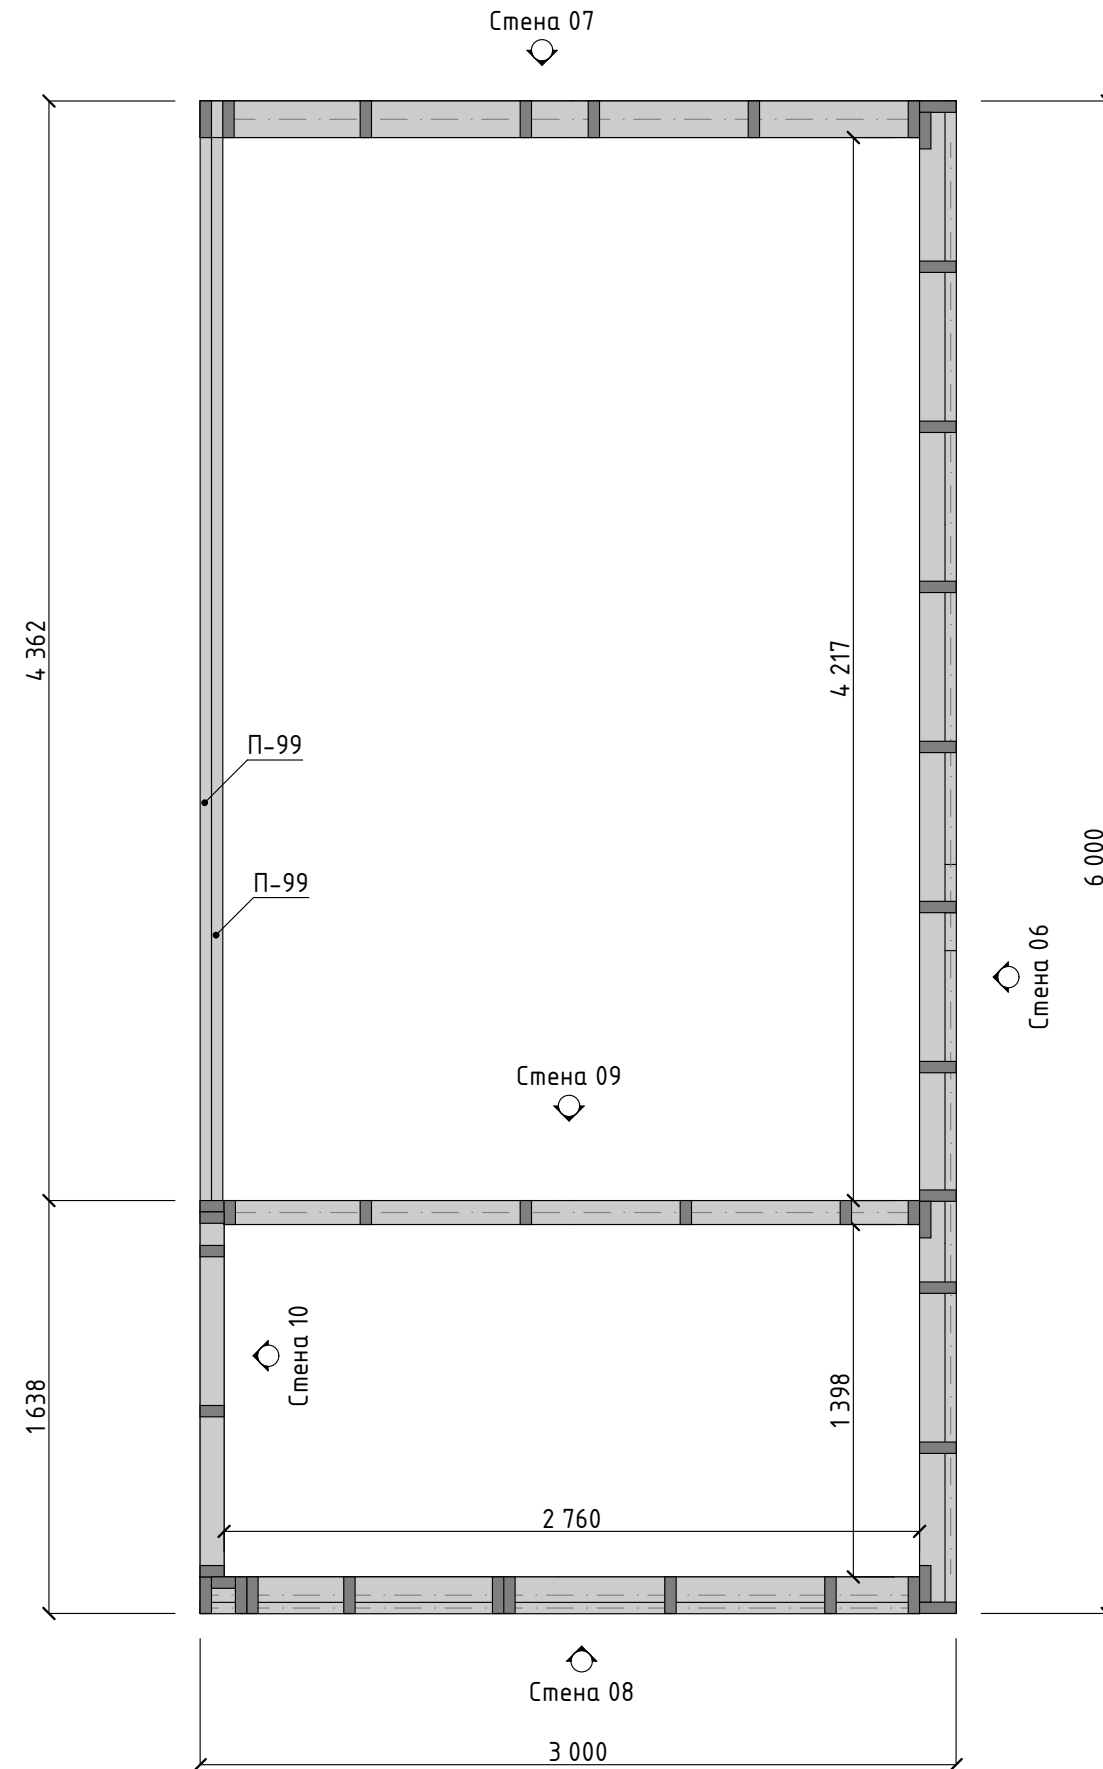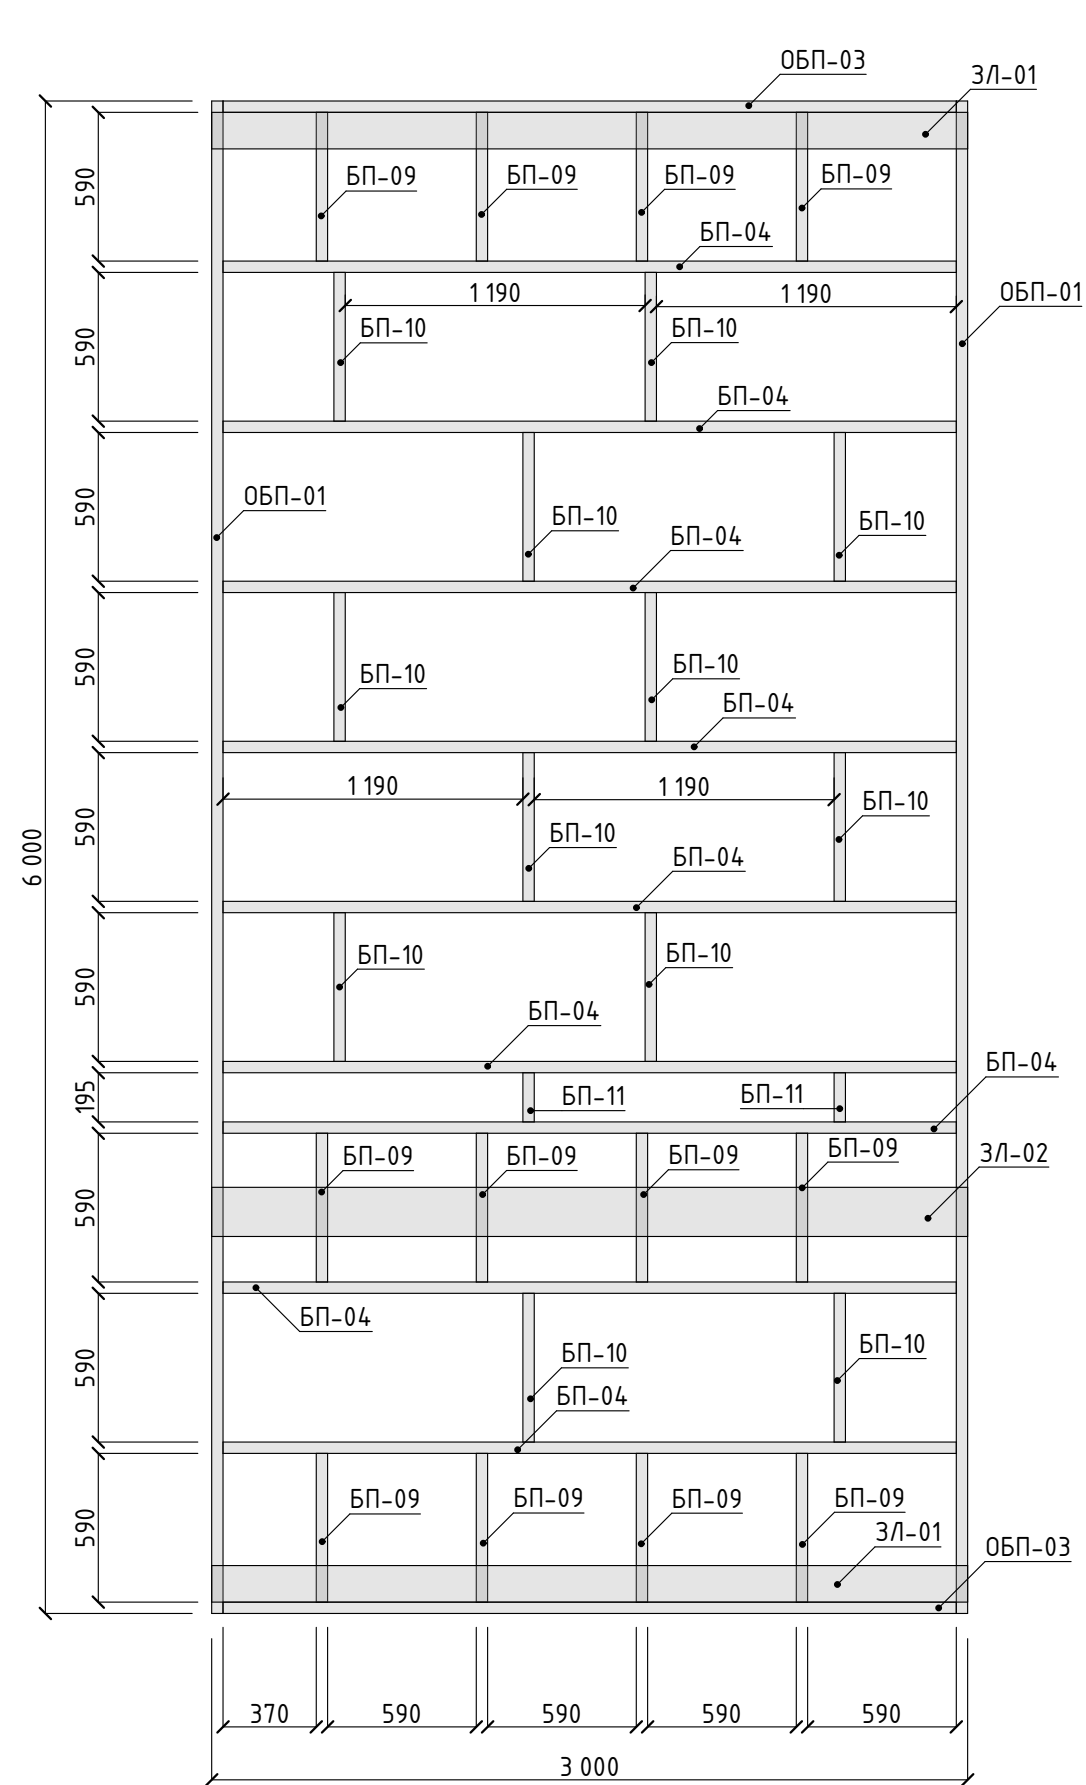


Спецификация элементов перекрытия 1 этажа МЗ				
Поз.	Ширина, мм	Высота, мм	Длина, мм	Кол-во
БП-04	45	195	2 910	9
БП-09	45	145	590	12
БП-10	45	195	590	12
БП-11	45	195	195	2
ЗЛ-01	145	45	3 000	2
ЗЛ-02	195	45	3 000	1
ОБП-01	45	195	6 000	2
ОБП-03	45	195	2 910	2

Спецификация элементов Модуля 3				
Поз.	Ширина, мм	Высота, мм	Длина, мм	Кол-во
П-99	45	145	4 407	2


План расположения элементов стен. Стена 06

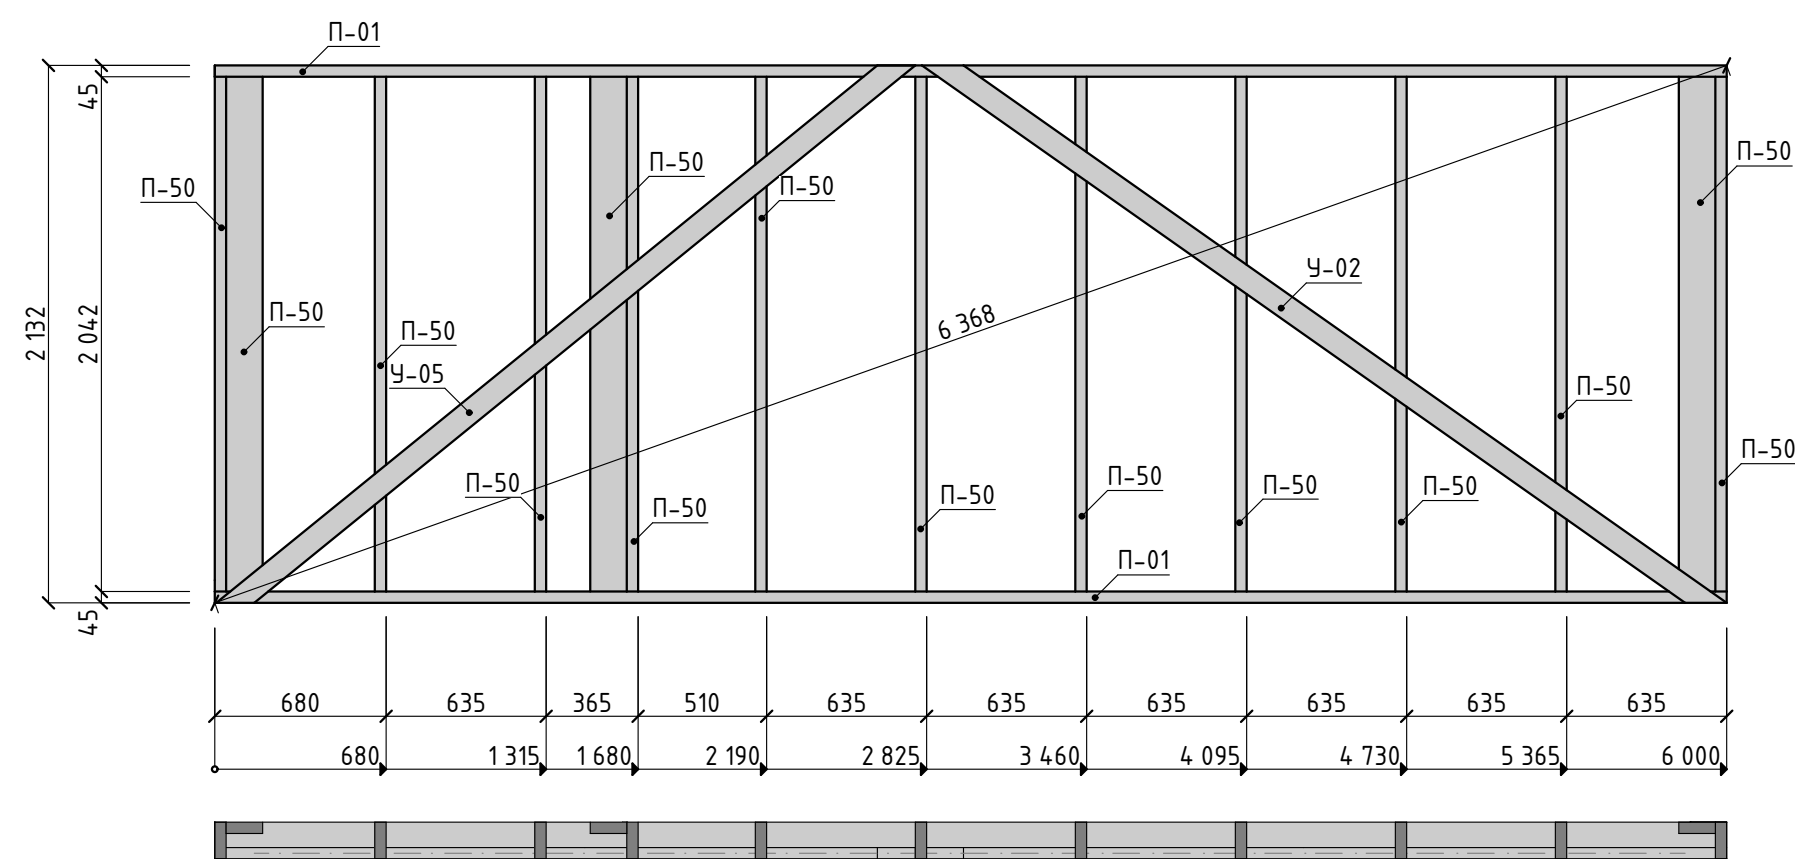


Спецификация элементов Стены 06				
Поз.	Ширина, мм	Высота, мм	Длина, мм	Кол-во
П-01	145	45	6 000	2
П-50	145	45	2 042	14
Ч-02	45	95	3 839	1
Ч-05	45	95	3 497	1

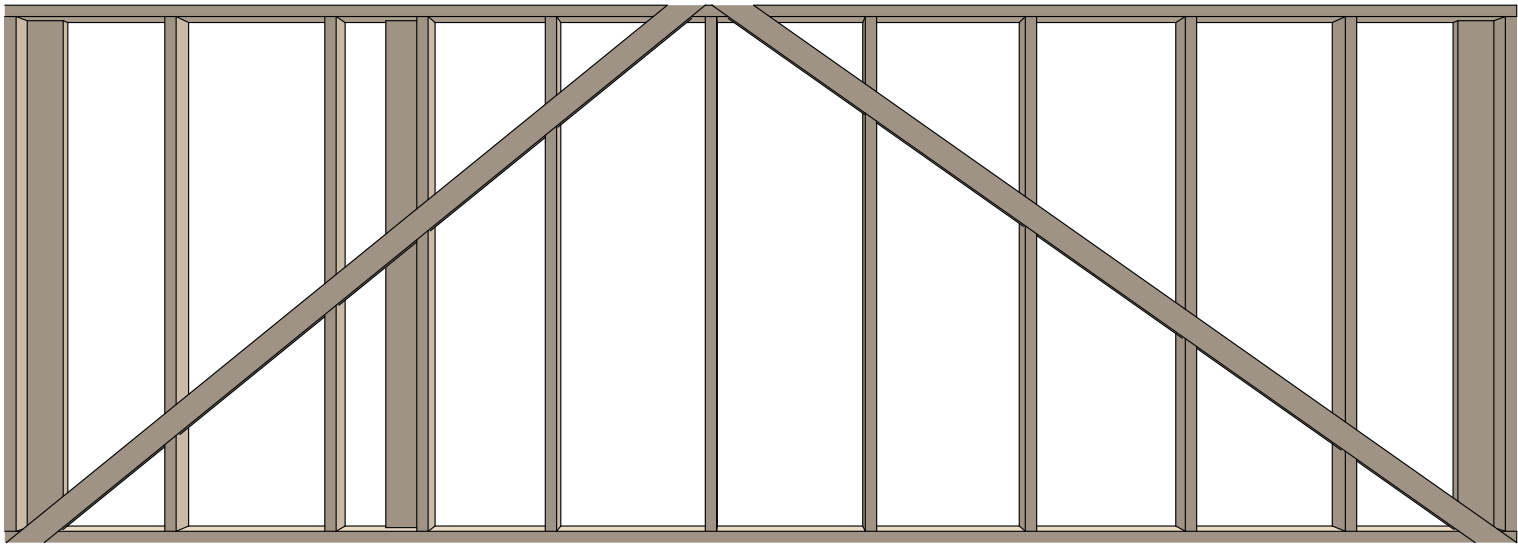


План расположения элементов стены. Стена 07

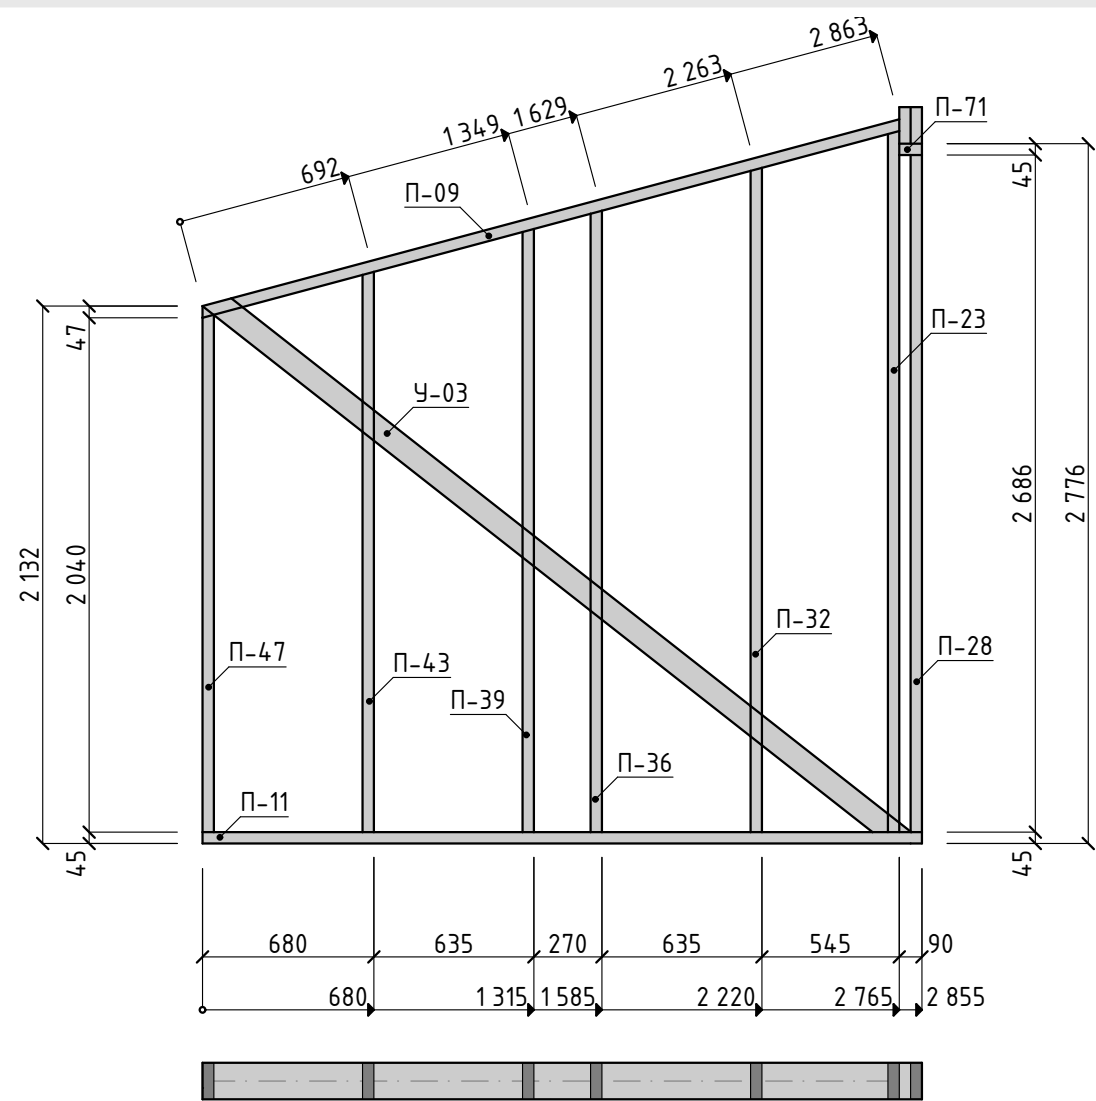


Спецификация элементов Стены 07				
Поз.	Ширина, мм	Высота, мм	Длина, мм	Кол-во
П-09	145	45	2 875	1
П-11	145	45	2 855	1
П-23	145	45	2 781	1
П-28	145	45	2 686	1
П-32	145	45	2 635	1
П-36	145	45	2 465	1
П-39	145	45	2 393	1
П-43	145	45	2 223	1
П-47	145	45	2 052	1
П-71	145	45	90	1
У-03	45	95	3 501	1

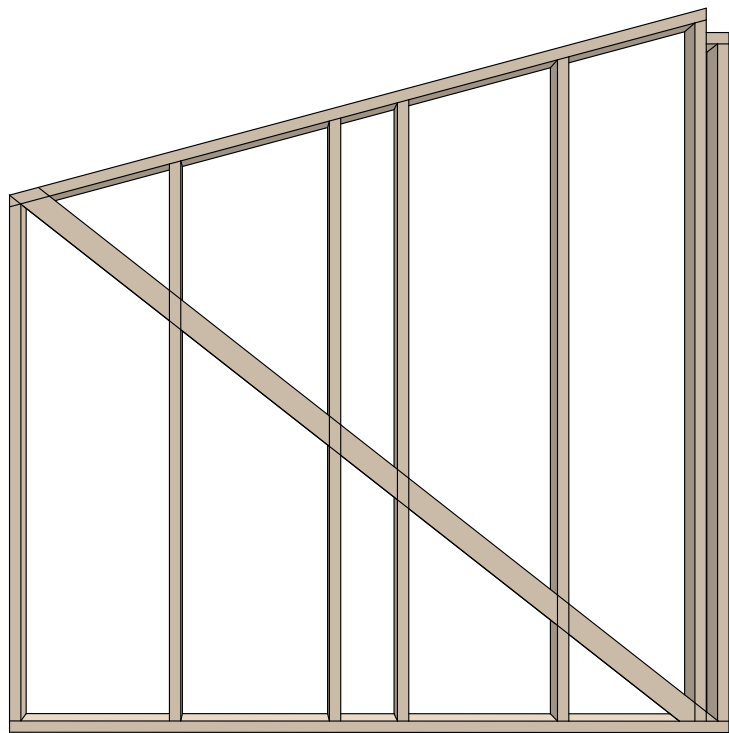



План расположения элементов стен. Стена 08

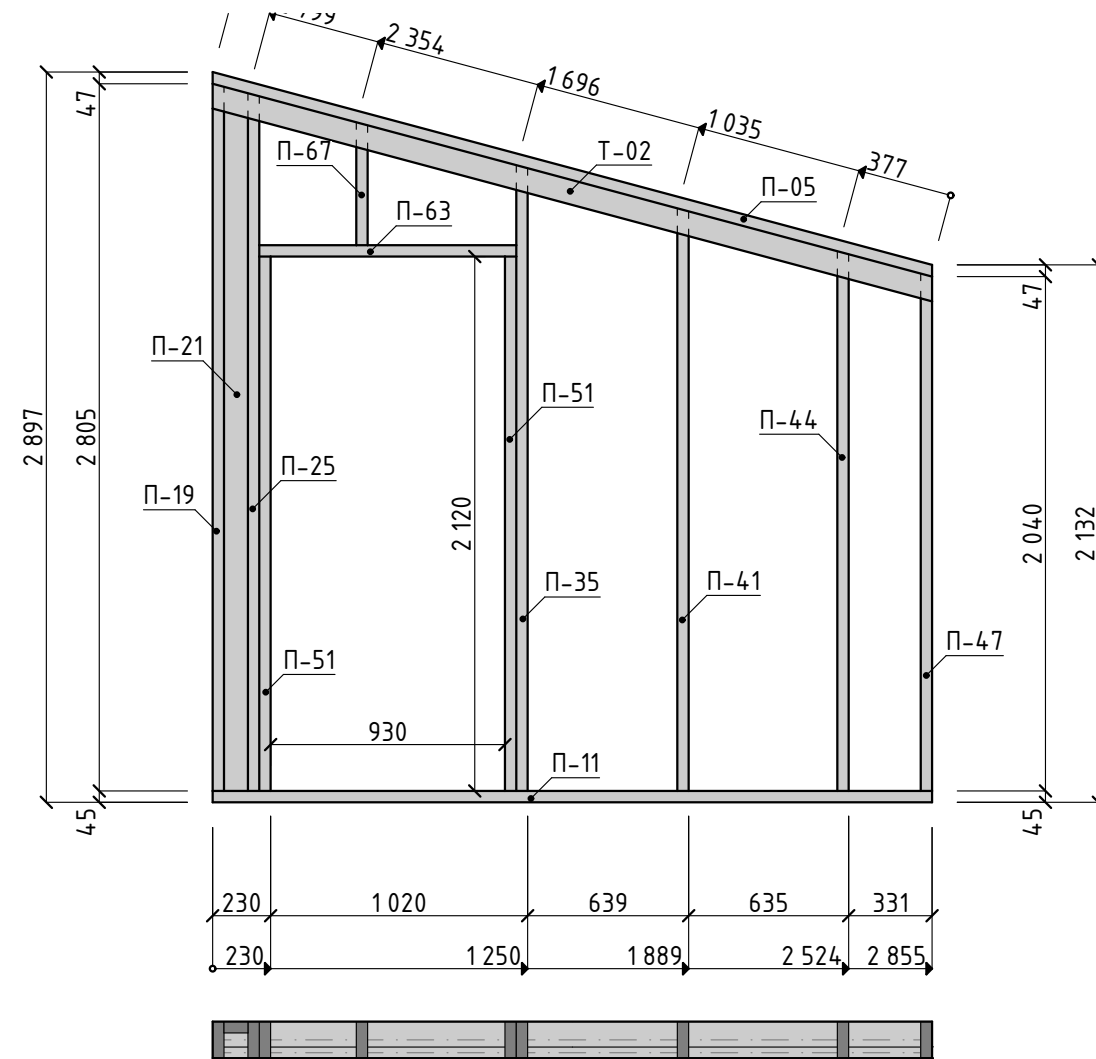

Спецификация элементов Стены 08				
Поз.	Ширина, мм	Высота, мм	Длина, мм	Кол-во
П-05	145	45	2 968	1
П-11	145	45	2 855	1
П-19	145	45	2 805	1
П-21	45	95	2 793	1
П-25	145	45	2 768	1
П-35	145	45	2 483	1
П-41	145	45	2 311	1
П-44	145	45	2 141	1
П-47	145	45	2 052	1
П-51	145	45	2 120	2
П-63	145	45	1 020	1
П-67	145	45	488	1
Т-02	45	95	2 981	1


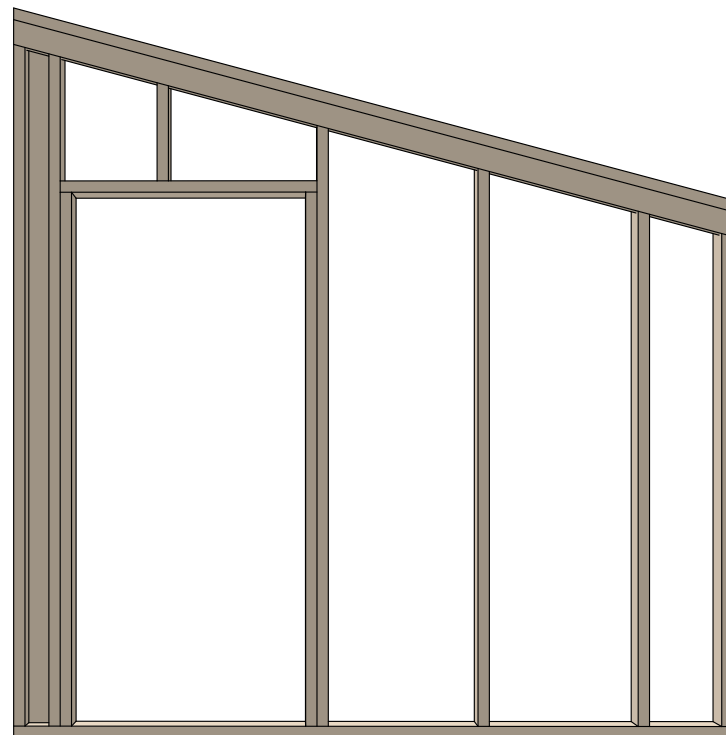


План расположения элементов стен. Стена 09. Стена 10


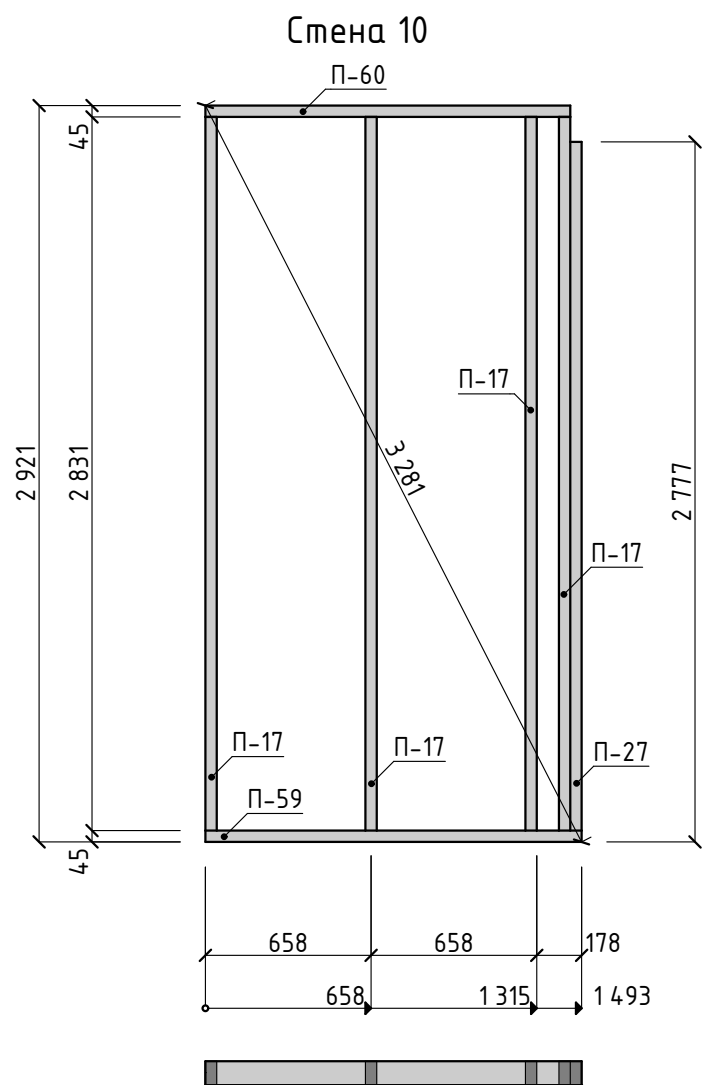
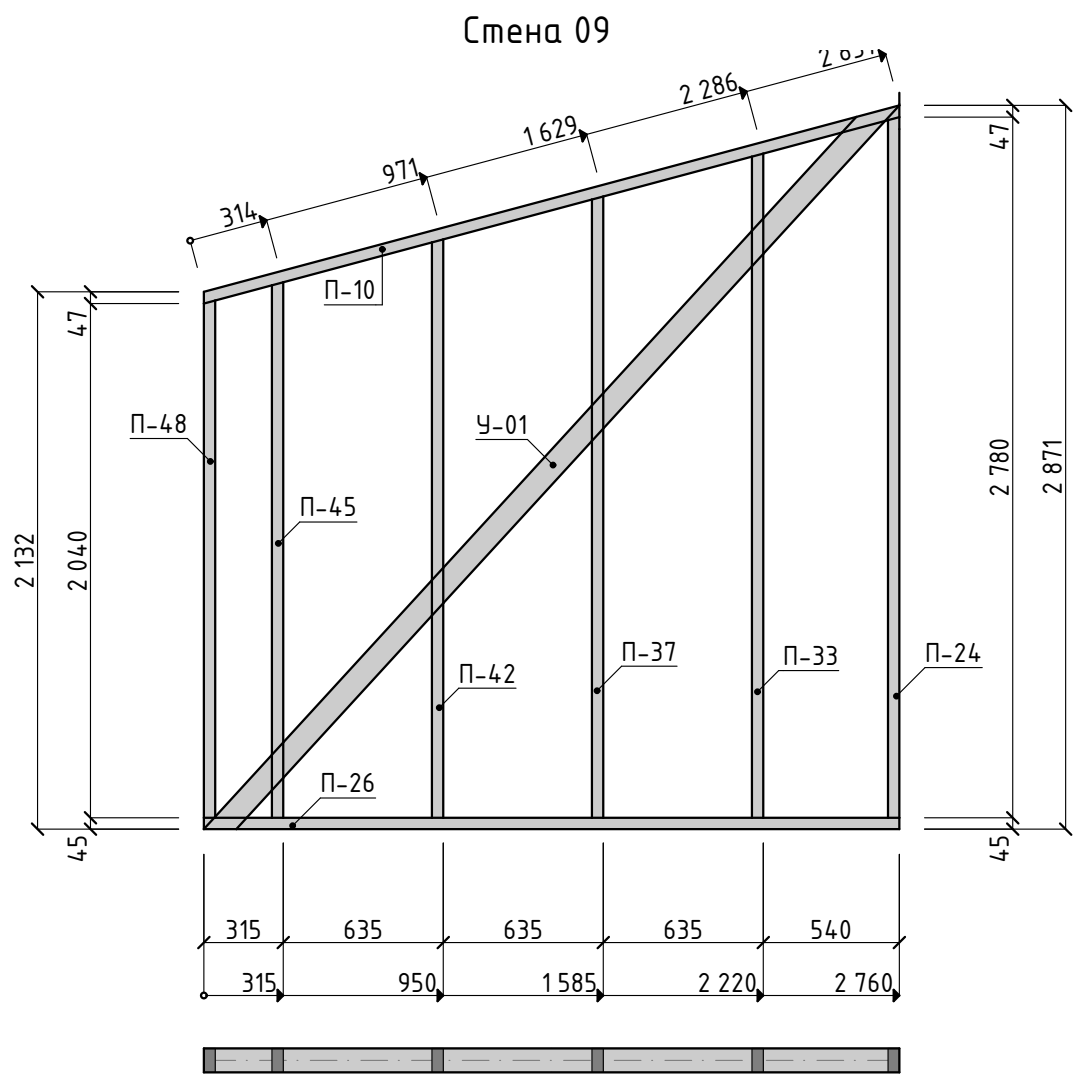


Спецификация элементов Стены 09				
Поз.	Ширина, мм	Высота, мм	Длина, мм	Кол-во
П-10	95	45	2 869	1
П-24	95	45	2 780	1
П-26	95	45	2 760	1
П-33	95	45	2 635	1
П-37	95	45	2 465	1
П-42	95	45	2 295	1
П-45	95	45	2 124	1
П-48	95	45	2 052	1
Ч-01	20	95	3 982	1

Спецификация элементов Стены 10				
Поз.	Ширина, мм	Высота, мм	Длина, мм	Кол-во
П-17	95	45	2 831	4
П-27	95	45	2 732	1
П-59	95	45	1 493	1
П-60	95	45	1 448	1

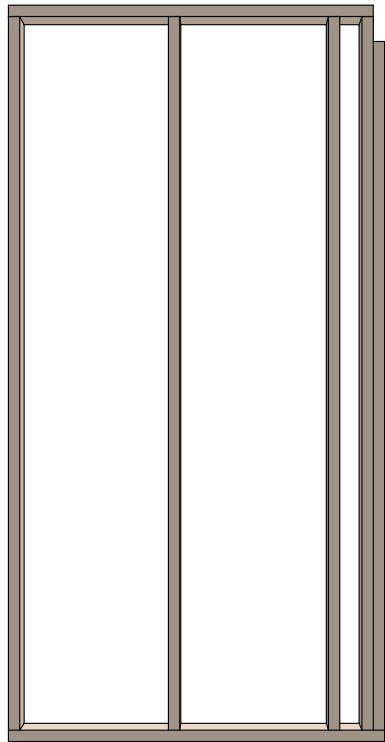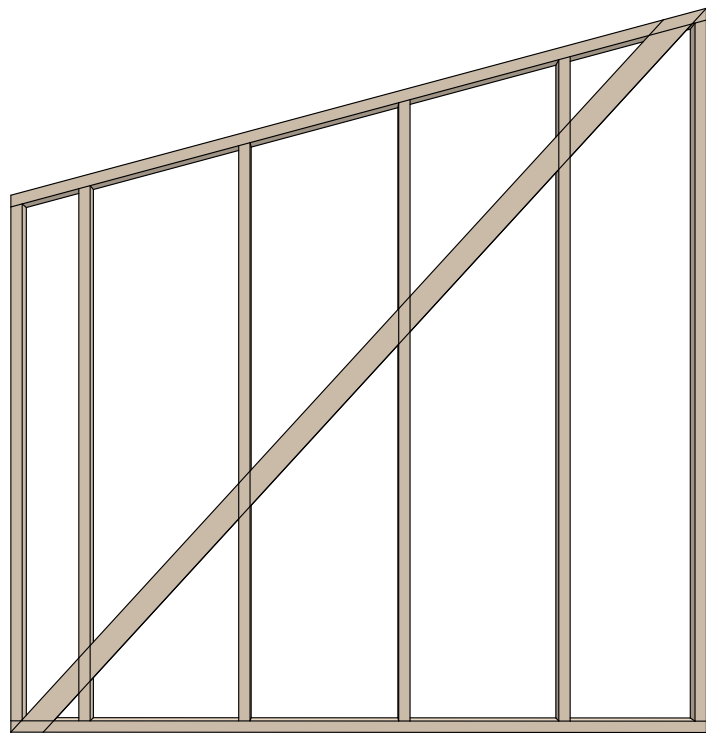


Стропильная система модуля 3

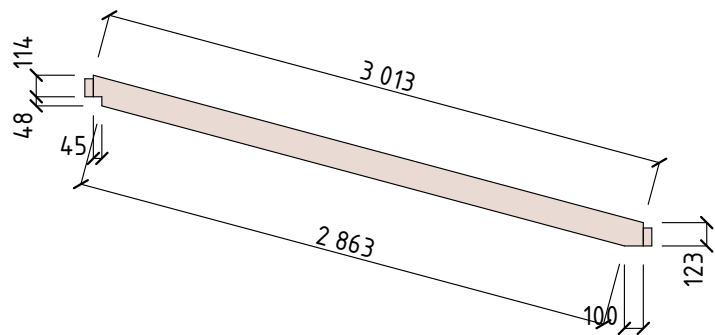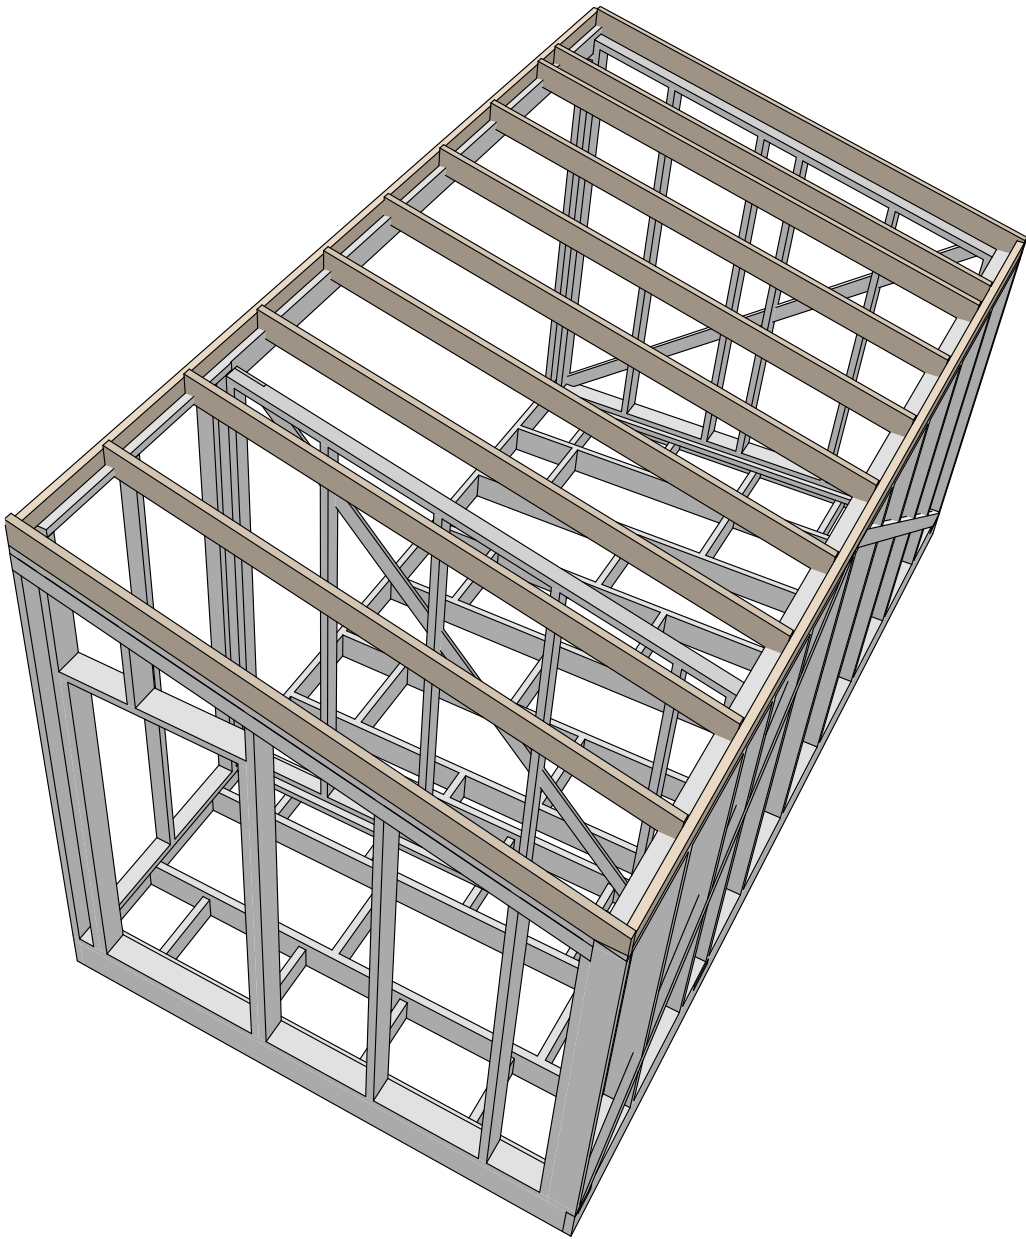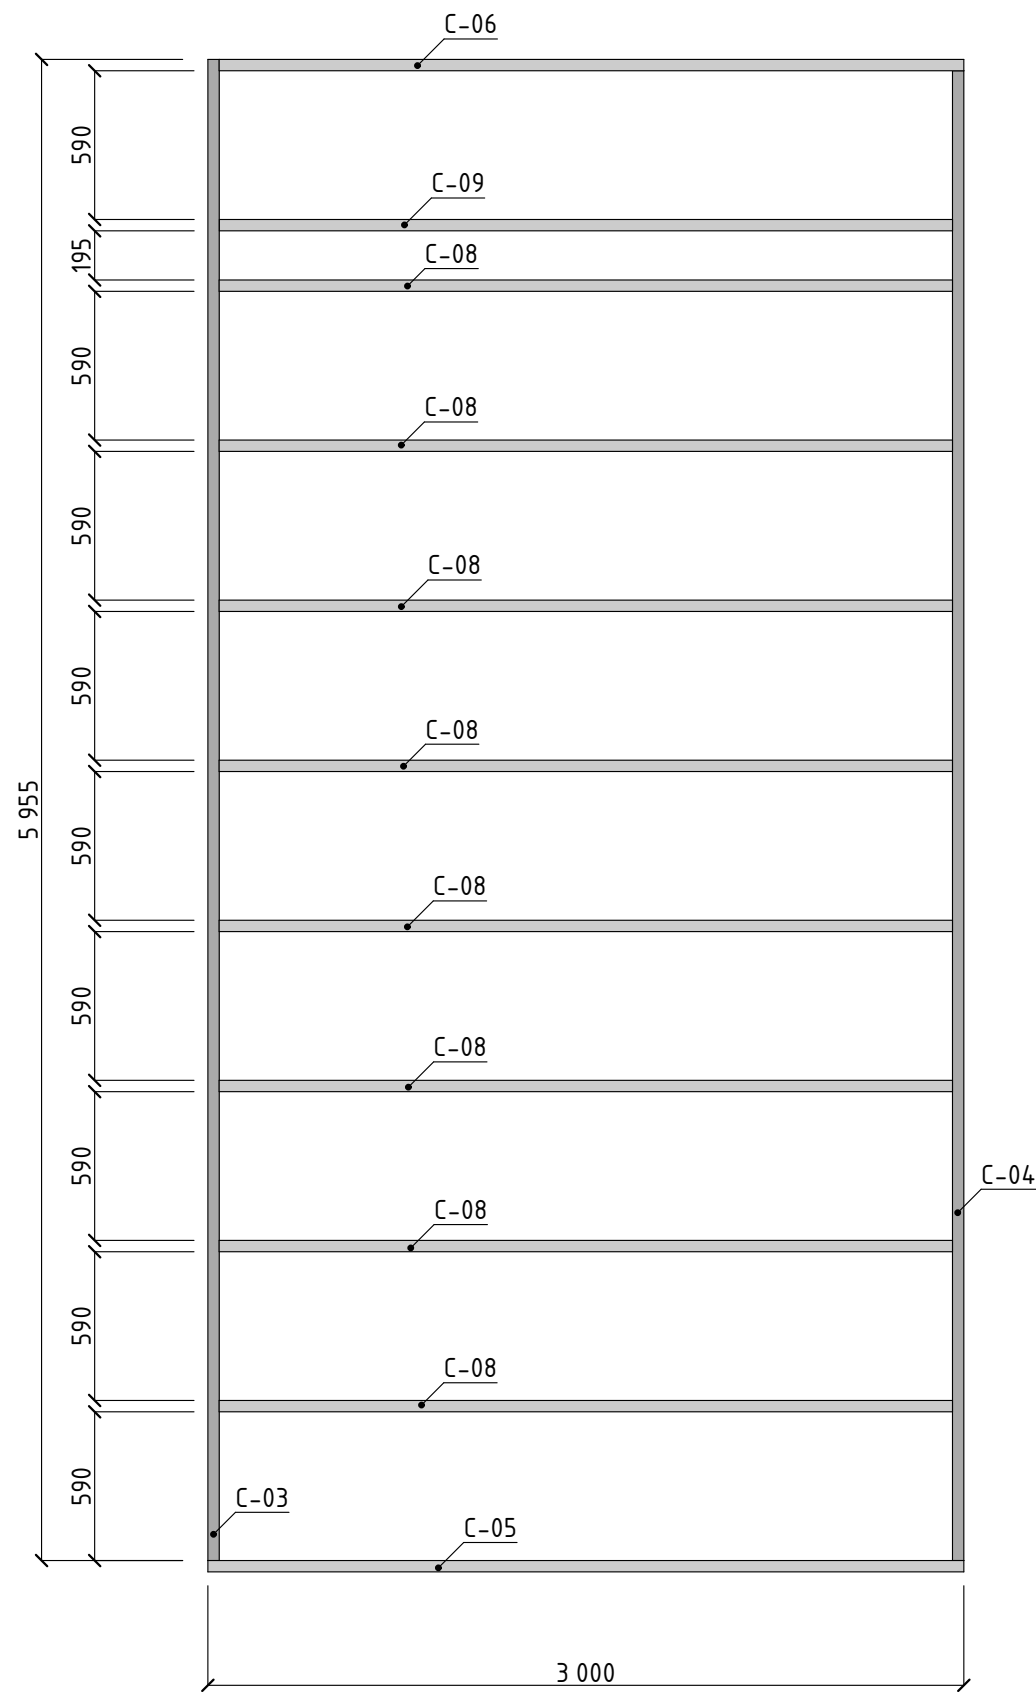


Спецификация элементов стропильной системы Модуля 3				
Поз.	Ширина, мм	Высота, мм	Длина, мм	Кол-во
С-03	45	95	5 955	1
С-04	45	95	5 910	1
С-05	45	145	3 145	1
С-06	45	145	3 098	1
С-08	45	145	3 052	8
С-09	45	145	3 051	1


Модуль 4

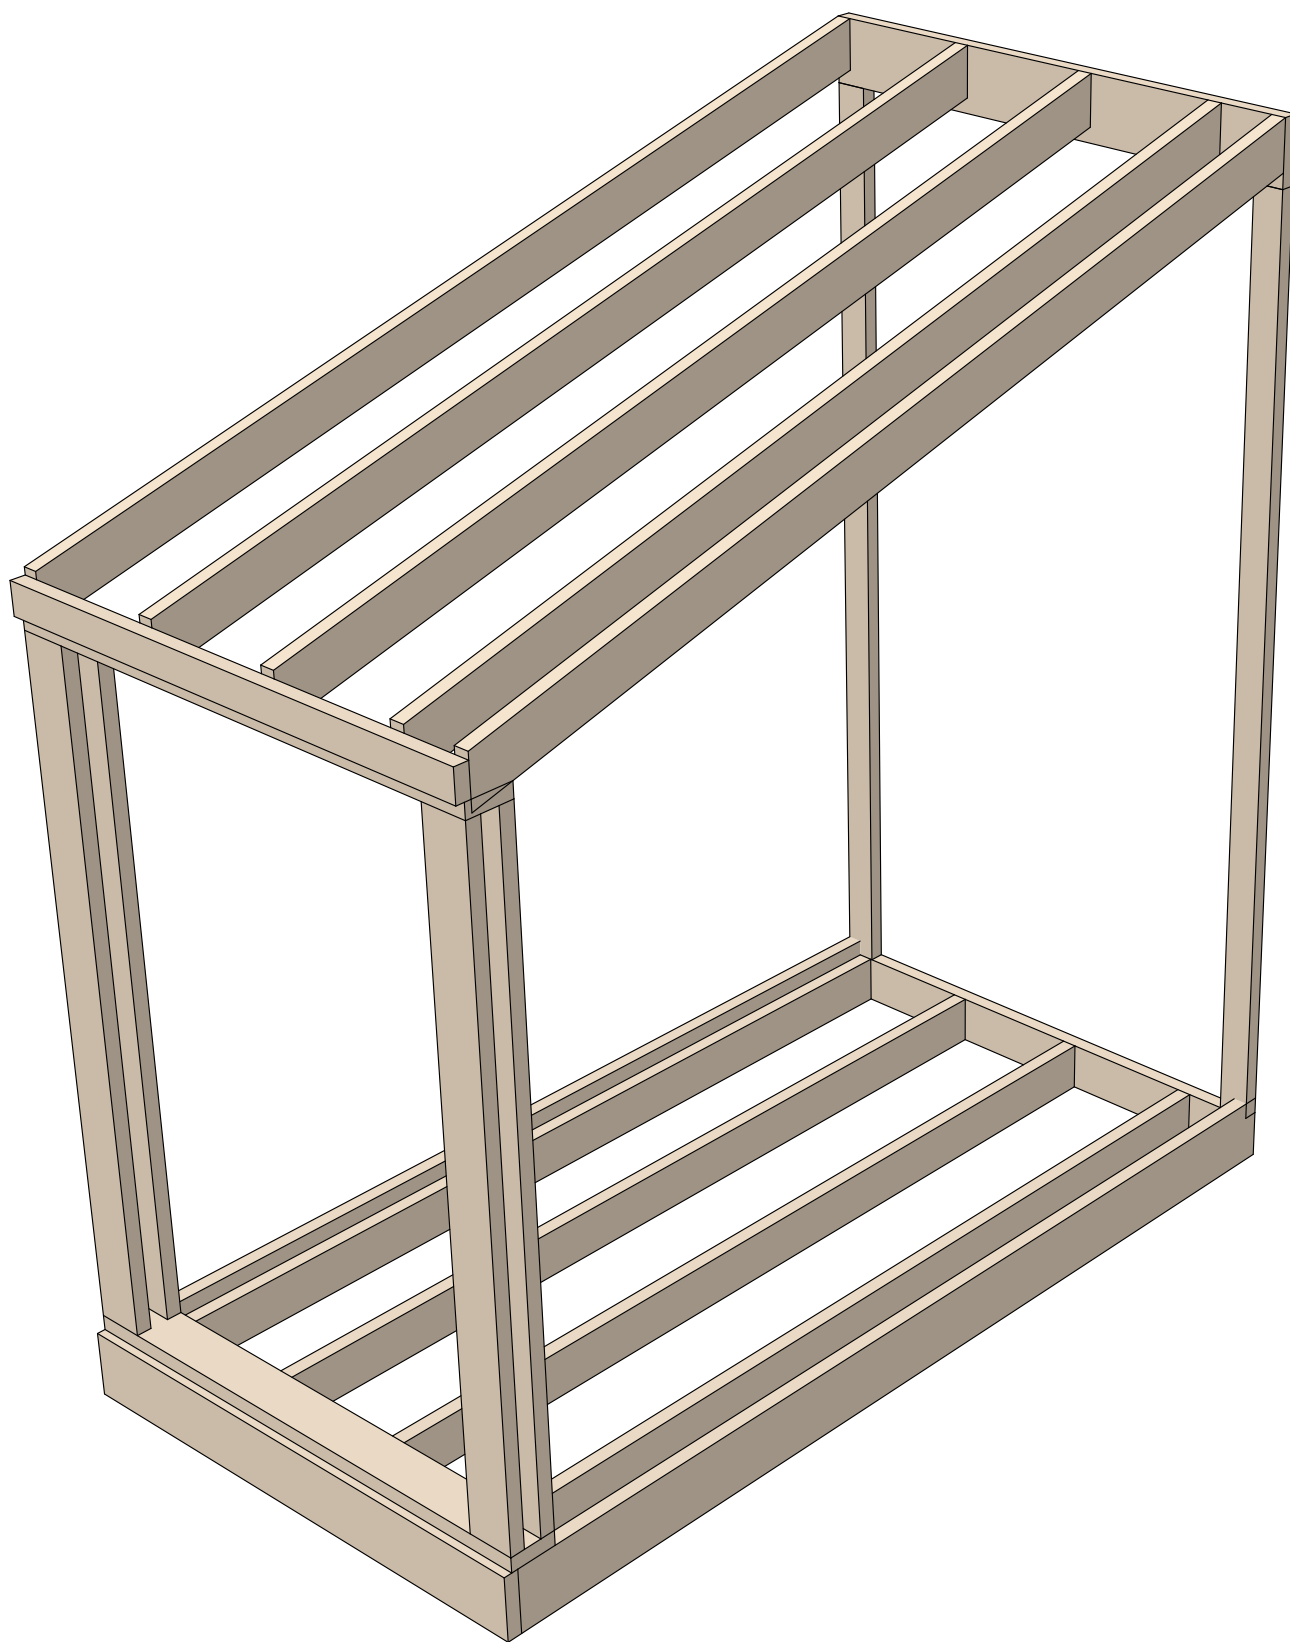

План расположения элементов перекрытия Модуля 4



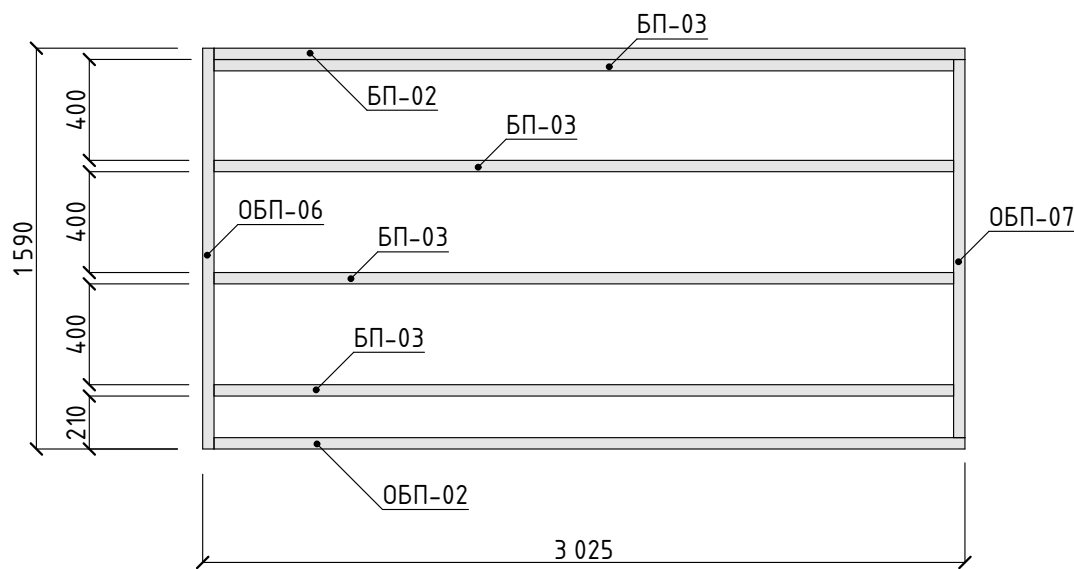


Спецификация элементов перекрытия 1 этажа М4				
Поз.	Ширина, мм	Высота, мм	Длина, мм	Кол-во
БП-02	45	195	2 980	1
БП-03	45	145	2 935	4
ОБП-02	45	195	2 980	1
ОБП-06	45	195	1 590	1
ОБП-07	45	145	1 500	1

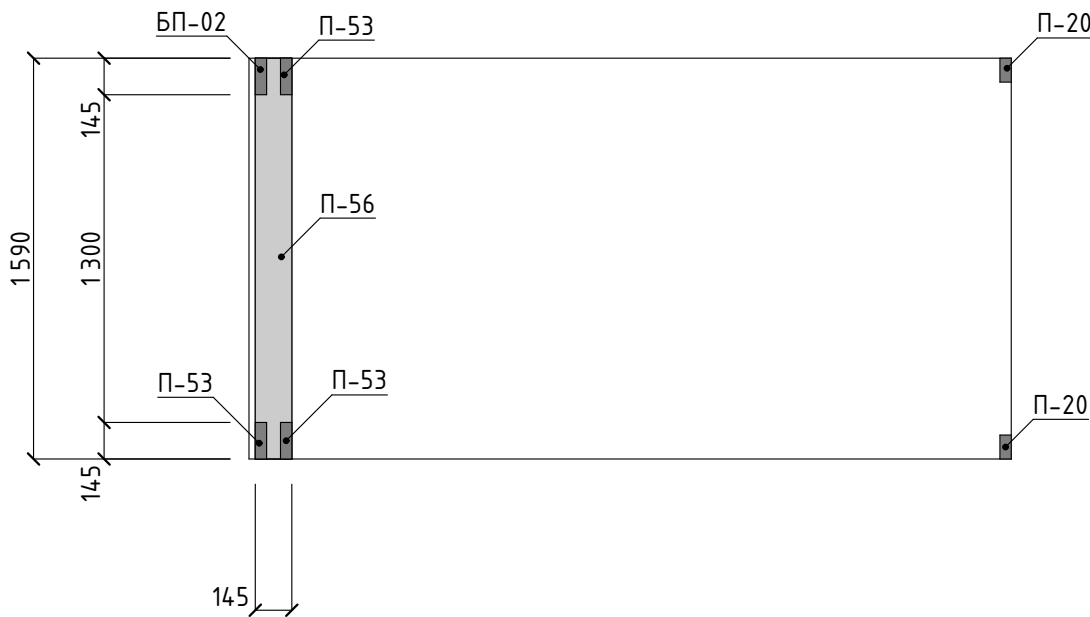


Спецификация элементов стен Модуля 4				
Поз.	Ширина, мм	Высота, мм	Длина, мм	Кол-во
П-20	95	45	2 845	2
П-53	145	45	1 997	4
П-56	145	45	1 590	2

Стропильная система Модуля 4

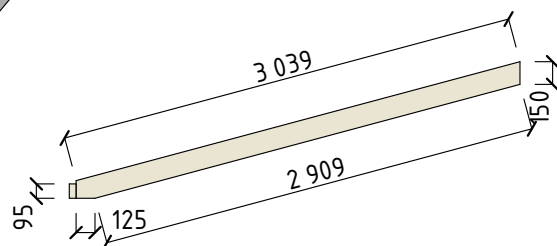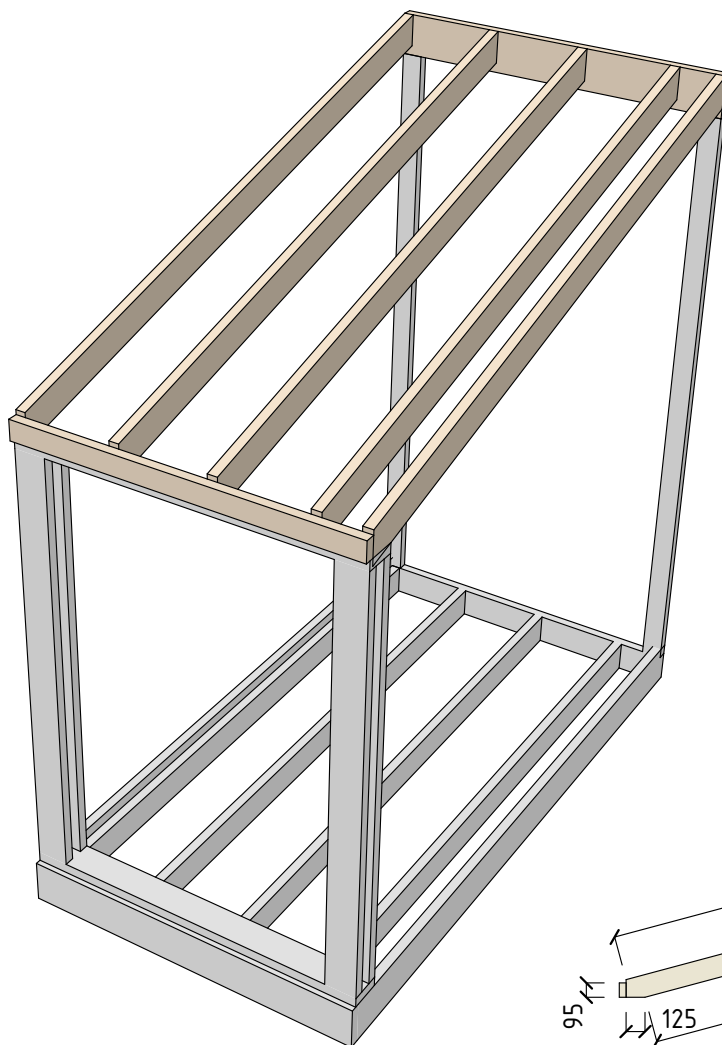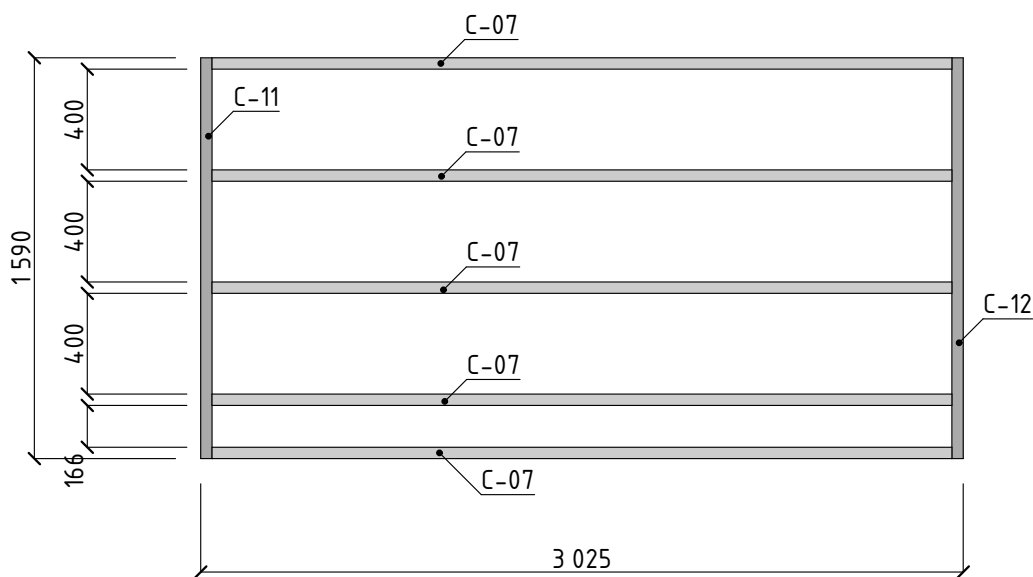

Спецификация элементов стропильной системы Модуля 4				
Поз.	Ширина, мм	Высота, мм	Длина, мм	Кол-во
C-07	45	145	3 077	5
C-11	45	95	1 590	1
C-12	45	195	1 590	1


Модуль 5

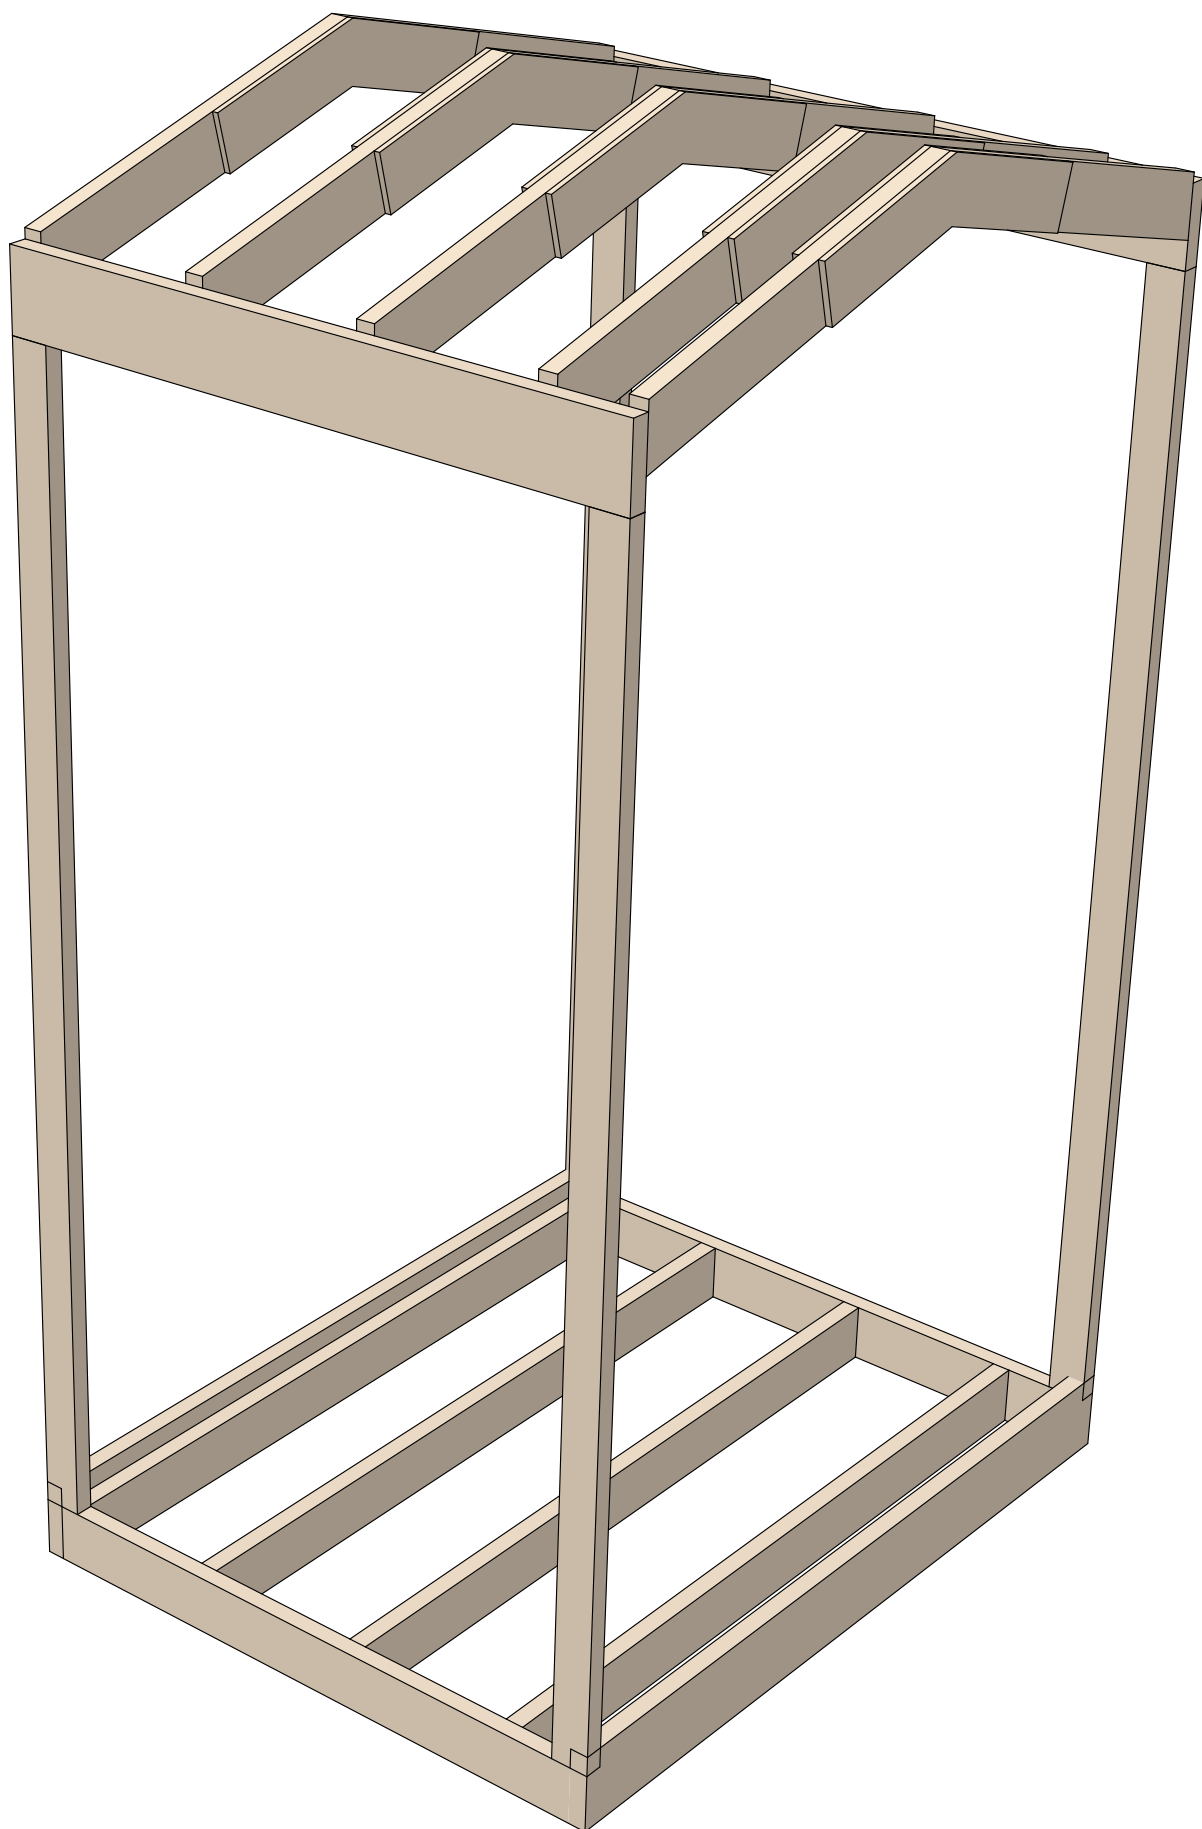


Модуль 5

Стадія	Лист	Листов
КР	36	43

План расположения элементов перекрытия Модуля 5



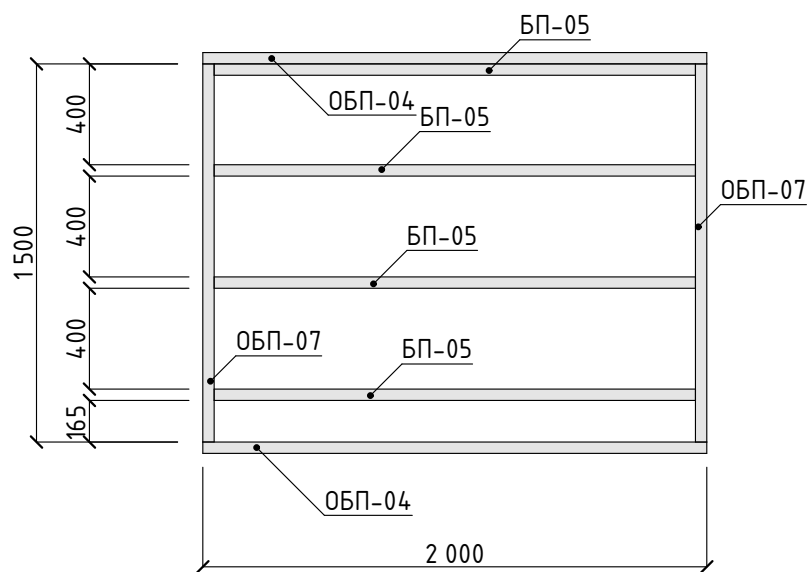


Спецификация элементов перекрытия 1 этажа М5				
Поз.	Ширина, мм	Высота, мм	Длина, мм	Кол-во
БП-05	45	145	1 910	4
ОБП-04	45	195	2 000	2
ОБП-07	45	145	1 500	2

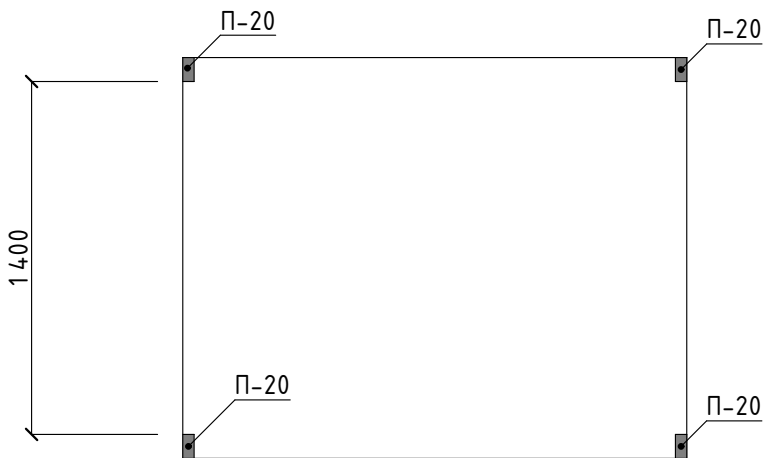


Спецификация элементов стен Модуля 5				
Поз.	Ширина, мм	Высота, мм	Длина, мм	Кол-во
П-20	95	45	2 845	4

План расположения элементов стропильной системы Модуля 5

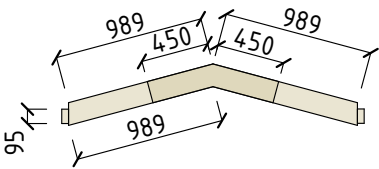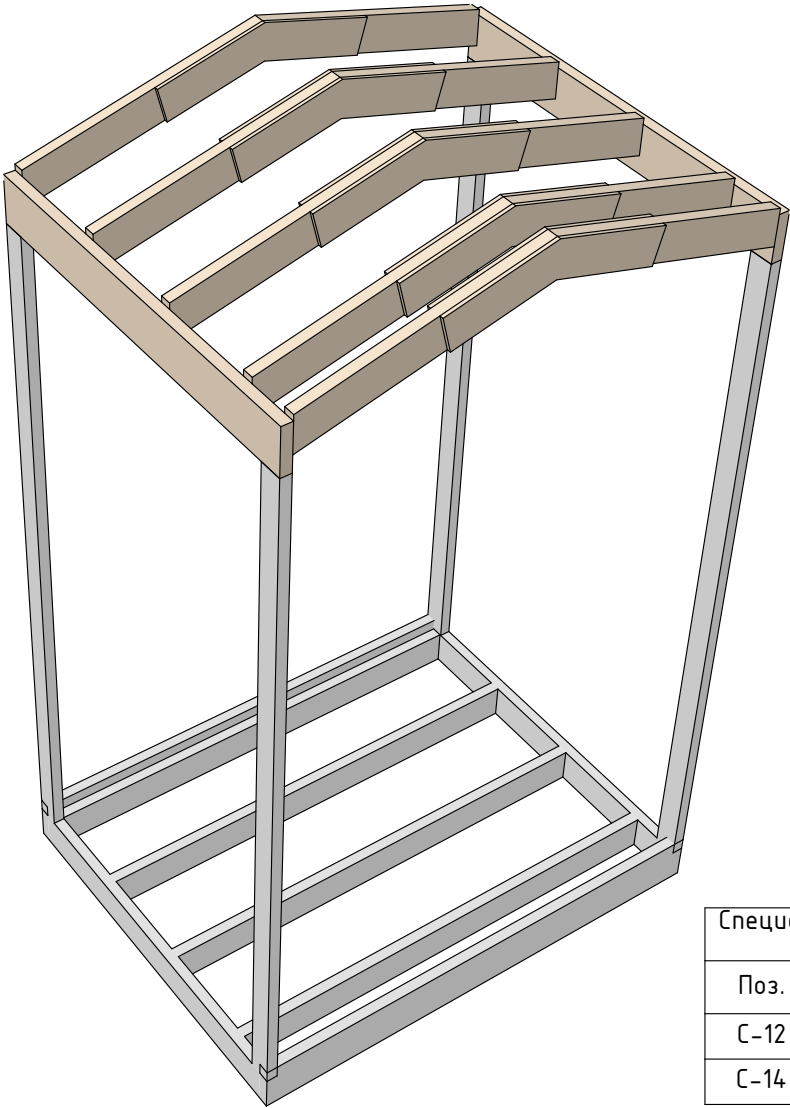
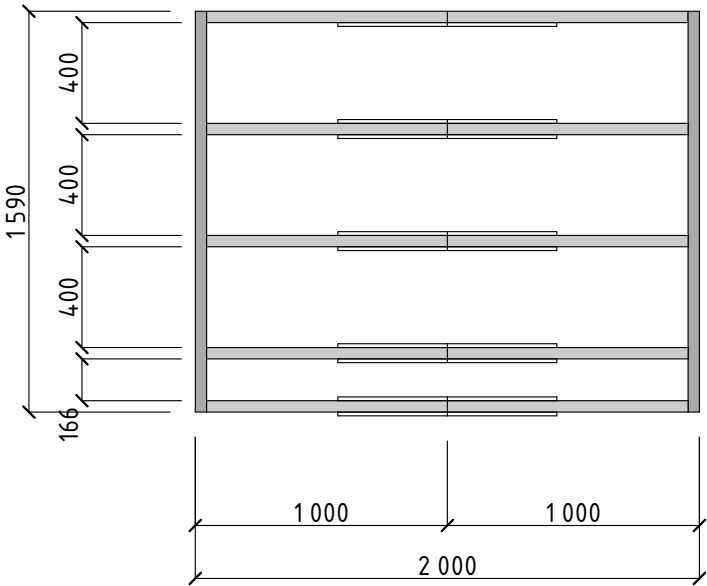


Спецификация элементов стропильной системы Модуля 5				
Поз.	Ширина, мм	Высота, мм	Длина, мм	Кол-во
С-12	45	195	1590	2
С-14	45	145	1028	10

Модуль 6

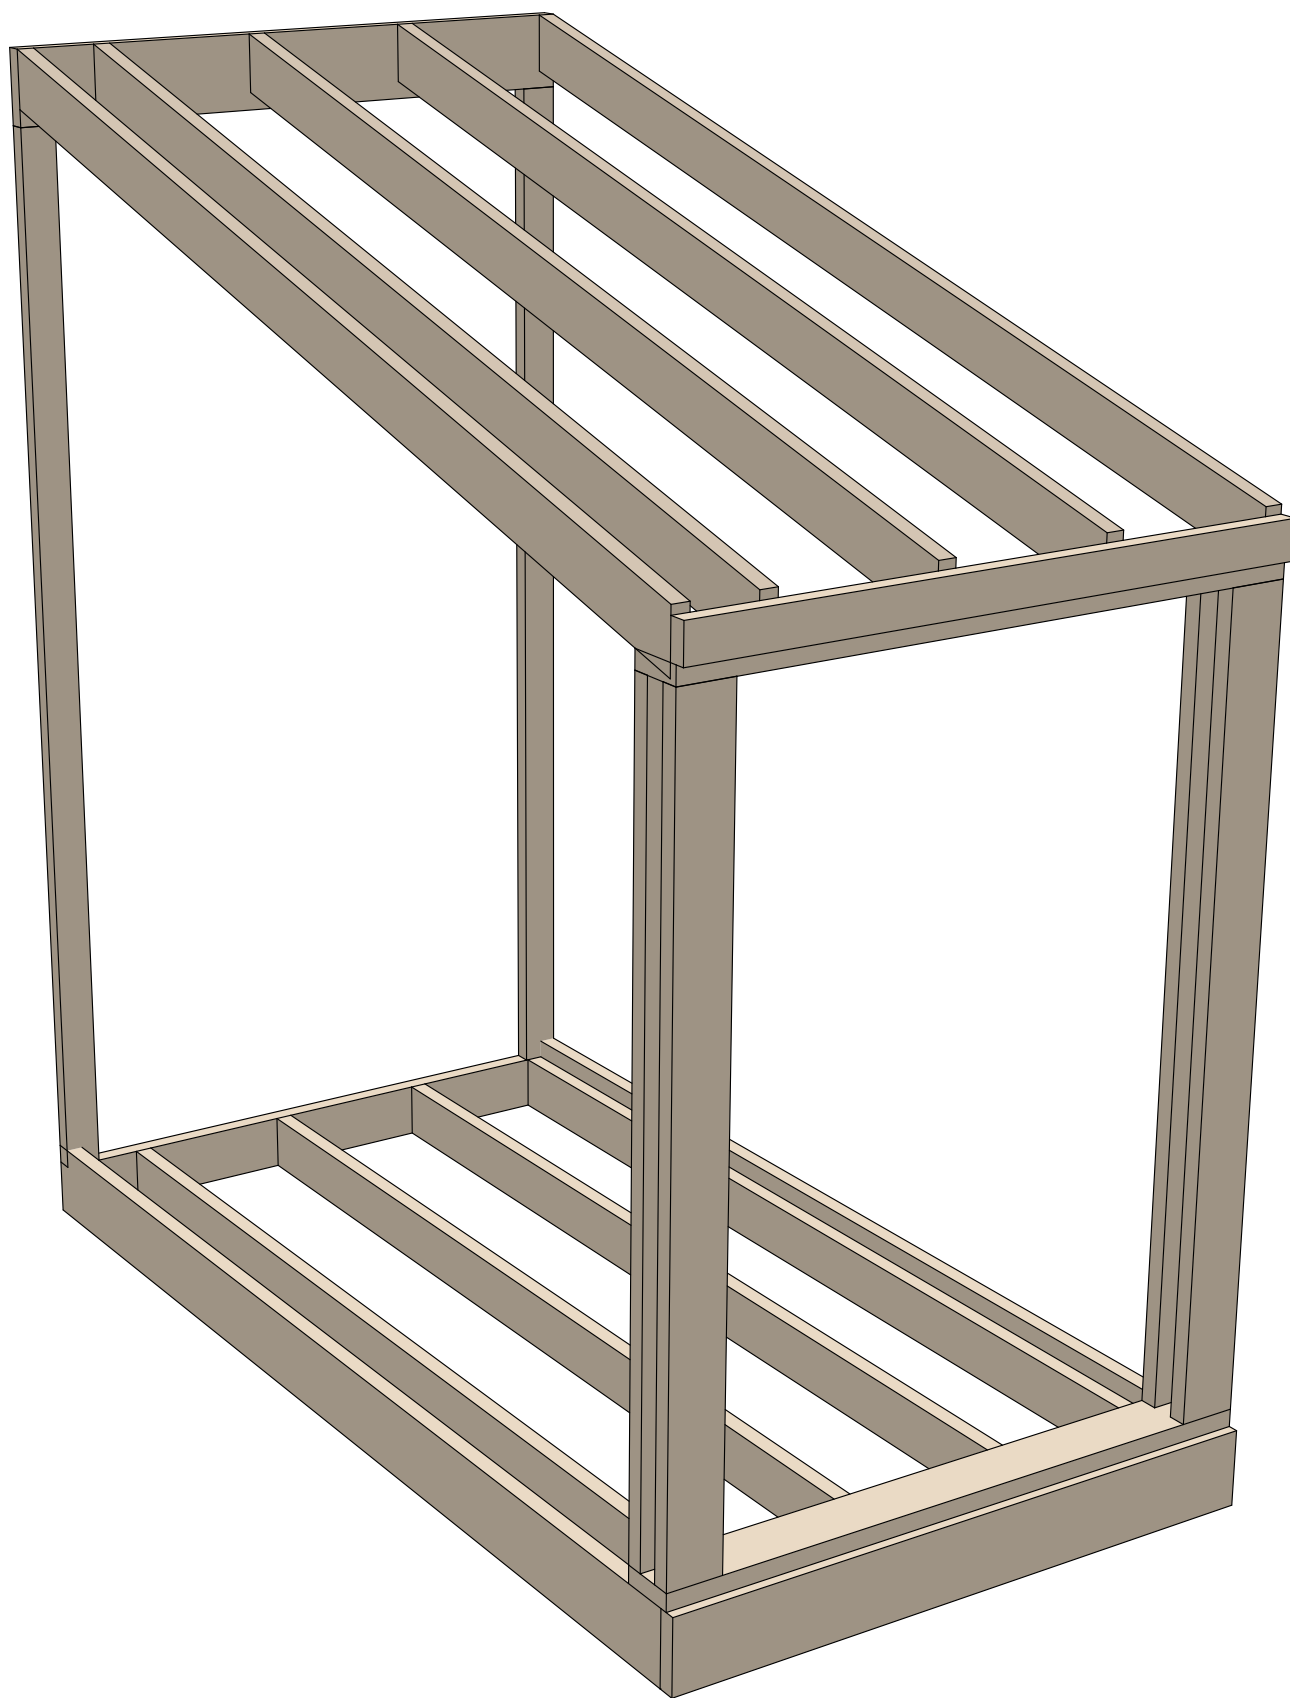




План расположения элементов перекрытия Модуля 6

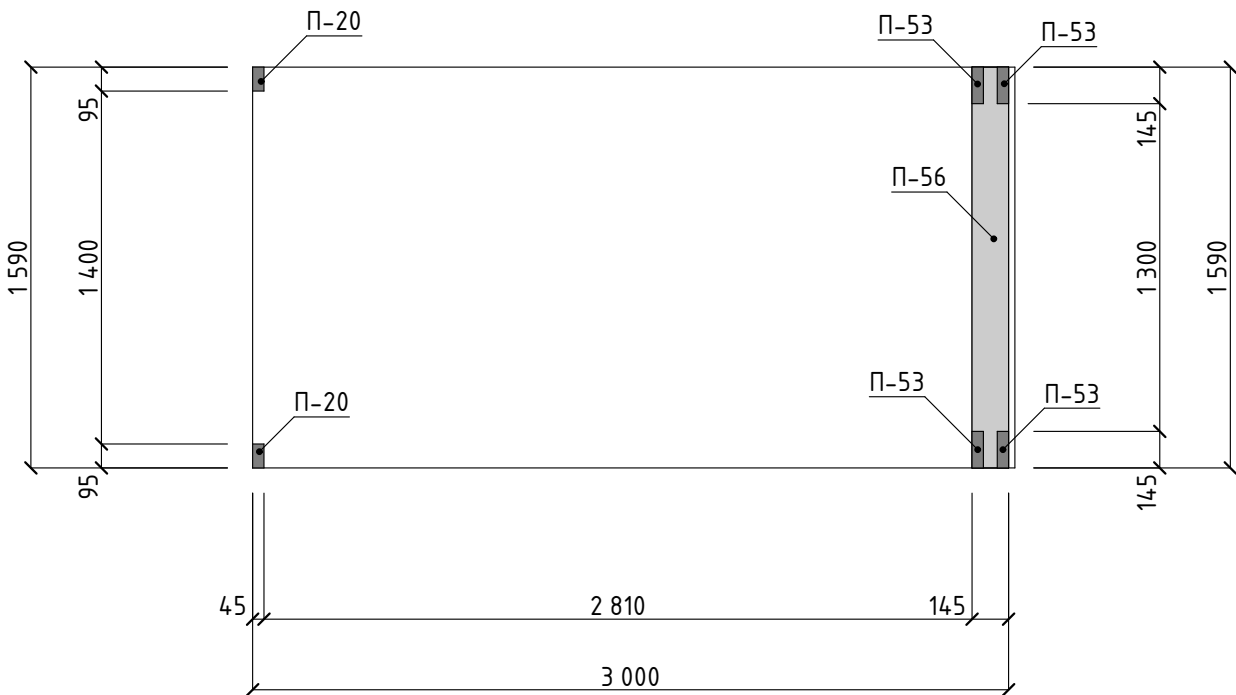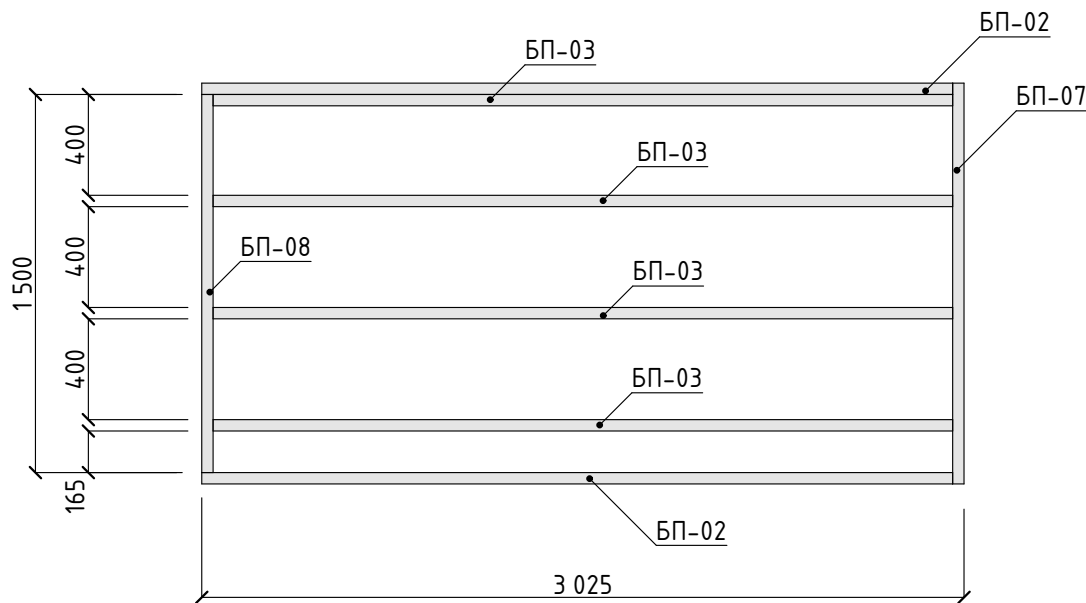

Спецификация элементов перекрытия 1 этажа М6				
Поз.	Ширина, мм	Высота, мм	Длина, мм	Кол-во
БП-02	45	195	2 980	2
БП-03	45	145	2 935	4
БП-07	45	195	1 590	1
БП-08	45	145	1 500	1

Спецификация элементов стен Модуля 6				
Поз.	Ширина, мм	Высота, мм	Длина, мм	Кол-во
П-20	95	45	2 845	2
П-53	145	45	1 997	4
П-56	145	45	1 590	2

План расположения элементов стропильной системы
Модуля 6

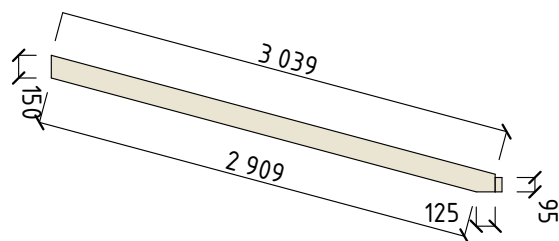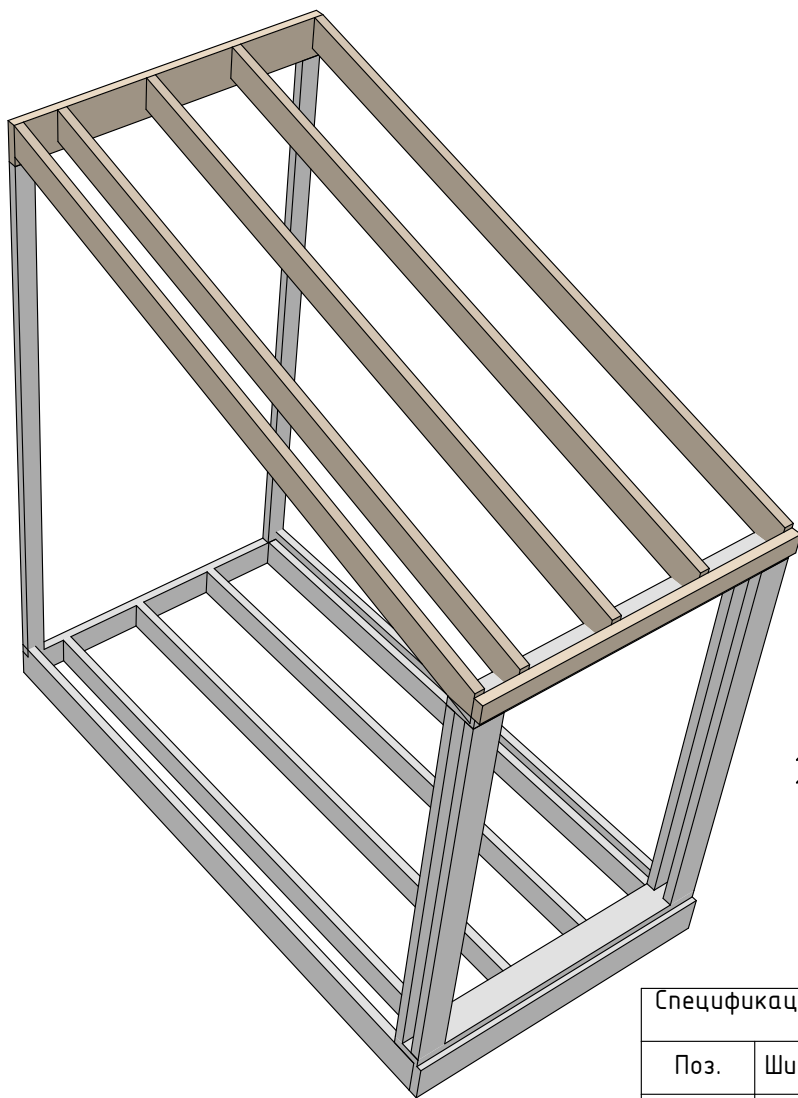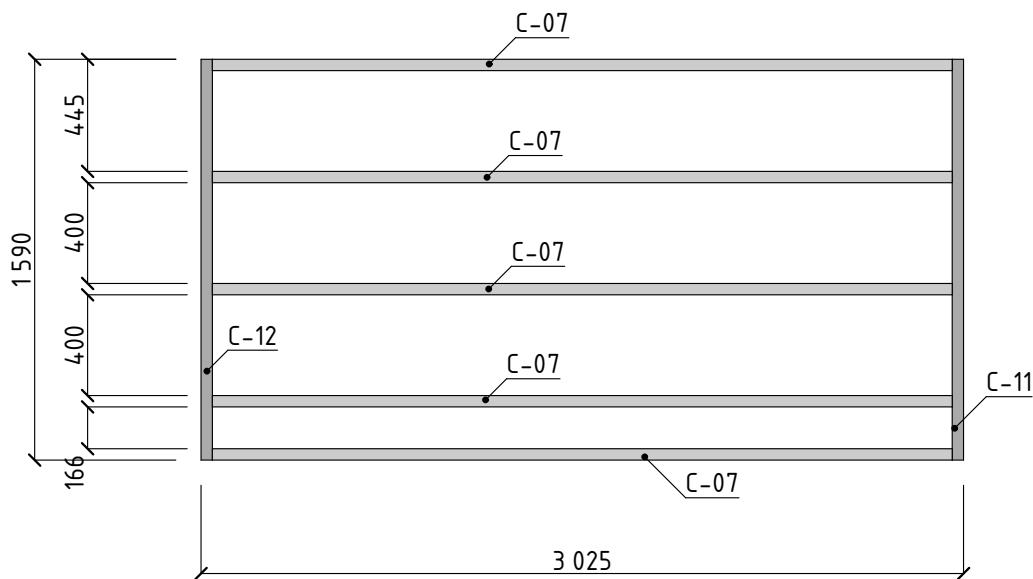

Спецификация элементов стропильной системы Модуля 6				
Поз.	Ширина, мм	Высота, мм	Длина, мм	Кол-во
С-07	45	145	3 077	5
С-11	45	95	1 590	1
С-12	45	195	1 590	1

Спецификация пиломатериала силового каркаса

Наименование	Поз.	Сеч., мм	Длина, мм	Кол-во
Брус, сечение 45х145 мм				
	БП-03	45х145	2 935	8
	БП-09	45х145	590	24
	БП-05	45х145	1 910	4
	БП-08	45х145	1 500	1
	ОБП-07	45х145	1 500	3
	П-02	45х145	4 362	2
	П-99	45х145	4 407	2
	С-15	45х145	996	11
	С-14	45х145	1 028	19
	С-13	45х145	1 074	2
	С-10	45х145	3 020	11
	С-09	45х145	3 051	1
	С-08	45х145	3 052	8
	С-07	45х145	3 077	10
	С-06	45х145	3 098	1
	С-05	45х145	3 145	1
	П-21	45х145	2 793	1
	П-12	45х145	2 843	1
	ШВ-02	45х145	---	4
	ШВ-01	45х145	---	3
	П-56	45х145	1 590	4
	ОС-08	45х145	5 850	2
	П-55	45х145	1 670	1
	П-11	45х145	2 855	4
	П-52	45х145	2 000	2
	ОС-13	45х145	2 855	3
	П-01	45х145	6 000	4
	П-72	45х145	75	4
	ОС-15	45х145	1 663	4
	П-40	45х145	2 330	2
	П-38	45х145	2 420	2
	ЗЛ-01	45х145	3 000	4
	ЗЛ-03	45х145	2 000	2
	П-63	45х145	1 020	2
	ОС-10	45х145	4 855	2
	БП-01	45х145	4 855	1
	ОС-16	45х145	1 543	4
	П-71	45х145	90	2
	П-57	45х145	1 580	1
	П-70	45х145	202	6
	П-66	45х145	954	1
	П-65	45х145	970	2
	П-69	45х145	273	1

	П-61	45х145	1 047	1
	П-68	45х145	392	1
	П-67	45х145	488	1
	П-09	45х145	2 875	1
	П-08	45х145	2 890	2
	П-05	45х145	2 968	1
	П-64	45х145	908	1
	П-62	45х145	1 045	6
	П-54	45х145	1 795	4
	П-53	45х145	1 997	8
	П-50	45х145	2 042	21
	П-49	45х145	2 052	1
	П-47	45х145	2 052	4
	П-46	45х145	2 075	2
	П-51	45х145	2 120	4
	П-44	45х145	2 141	1
	П-43	45х145	2 223	3
	П-41	45х145	2 311	1
	П-39	45х145	2 393	2
	П-36	45х145	2 465	1
	П-35	45х145	2 483	1
	П-34	45х145	2 563	1
	П-32	45х145	2 635	2
	П-31	45х145	2 637	2
	П-30	45х145	2 637	2
	П-29	45х145	2 682	1
	П-28	45х145	2 686	2
	П-25	45х145	2 768	1
	П-23	45х145	2 781	1
	П-22	45х145	2 785	2
	П-19	45х145	2 805	1
	П-18	45х145	2 817	1
	П-14	45х145	2 838	2
	П-13	45х145	2 842	1
	П-07	45х145	2 934	1
	П-06	45х145	2 939	1
	П-04	45х145	2 988	2
	П-03	45х145	3 073	1
Брус, сечение 45х195 мм				
	ОБП-05	45х195	1 910	2
	С-12	45х195	1 590	4
	БП-04	45х195	2 910	18
	ОБП-04	45х195	2 000	2

	ОБП-03	45х195	2 910	4
	ОБП-01	45х195	6 000	6
	БП-06	45х195	1 910	9
	БП-07	45х195	1 590	1
	БП-02	45х195	2 980	3
	ОБП-02	45х195	2 980	1
	ОБП-06	45х195	1 590	1
	БП-10	45х195	590	33
	БП-11	45х195	195	5
	ОС-14	45х195	2 000	1
	ОС-11	45х195	3 000	2
	ЗЛ-02	45х195	3 000	1
Брус, сечение 45х95 мм				
	С-04	45х95	5 910	2
	С-11	45х95	1 590	2
	С-03	45х95	5 955	1
	С-01	45х95	6 000	1
	Т-05	45х95	983	1
	Т-04	45х95	1 061	1
	Т-03	45х95	2 904	1
	Т-02	45х95	2 981	1
	У-03	45х95	3 501	1
	У-04	45х95	3 501	1
	У-05	45х95	3 497	1
	У-02	45х95	3 839	1
	С-02	45х95	6 000	2
	П-59	45х95	1 493	2
	П-60	45х95	1 448	1
	ОС-12	45х95	3 000	1
	П-26	45х95	2 760	1
	ОС-09	45х95	5 000	1
	П-58	45х95	1 538	1
	П-10	45х95	2 869	1
	П-48	45х95	2 052	1
	П-45	45х95	2 124	1
	П-42	45х95	2 295	1
	П-37	45х95	2 465	1
	П-33	45х95	2 635	1
	П-27	45х95	2 732	2
	П-24	45х95	2 780	1
	П-17	45х95	2 831	4
	П-16	45х95	2 832	3
	П-15	45х95	2 832	1
	П-20	45х95	2 845	8

Сводные данные	
----------------	--

Тип пиломатериала	Сечение, мм	Объем ед, м³
Сухой строганный ПМ		
	145x45	3,48
	195x45	1,64
	95x45	0,69
	95x20	0,62
	45x45	0,63

Наименование	Объем, м³
Объем утеплителя наружных стен	9,0
Объем утеплителя внутренних стен	1,54
Объем утеплителя стропильной системы	7,6
Объем утеплителя цокольного перекрытия	9,8
	27,94

Наименование	Объем, м³
Свая винтовая диам. 108 мм с оголовком 150х150 мм	20
	16

Тип	Наименование	Площадь, м ²
Крыша		
	Ветро-влагозащитная мембрана	62,81
	Внутр. отделка потолка – Имитация бруса	45,03
	Кровельное покрытие профлист	69,0
	Пароизоляция	45,58
Перекрытие		
	Ветро-влагозащитная мембрана	60,76
	Напольное покрытие – ПВХ плитка	38,48
	Напольное покрытие – Керамогранит	3,32
	Пароизоляция	48,0
Стена		
	Ветро-влагозащитная мембрана	67,18
	Внутр. отделка стен – Имитация бруса	61,26
	Внутр. отделка стен – Керам. плитка	35,1
	Нар. отделка – Планкен	36,4
	Нар. отделка – Профлист	24,8
	Пароизоляция	87,1

№	Наименование	Площадь, м ²
5	Терраса	12,8
	Свесы кровли над террасой – Планкен	13,2

Наименование	Площадь, м ²
Основная крыша	64,0
	64,0

№	Наименование	Площадь, м ²
1	Комната приема пищи	61,26
2	Тех помещение	35,1

№	Наименование	Площадь, м ²
1	Комната приема пищи	38,48
2	Тех помещение	3,32